


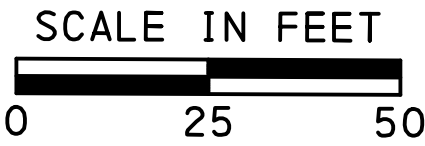
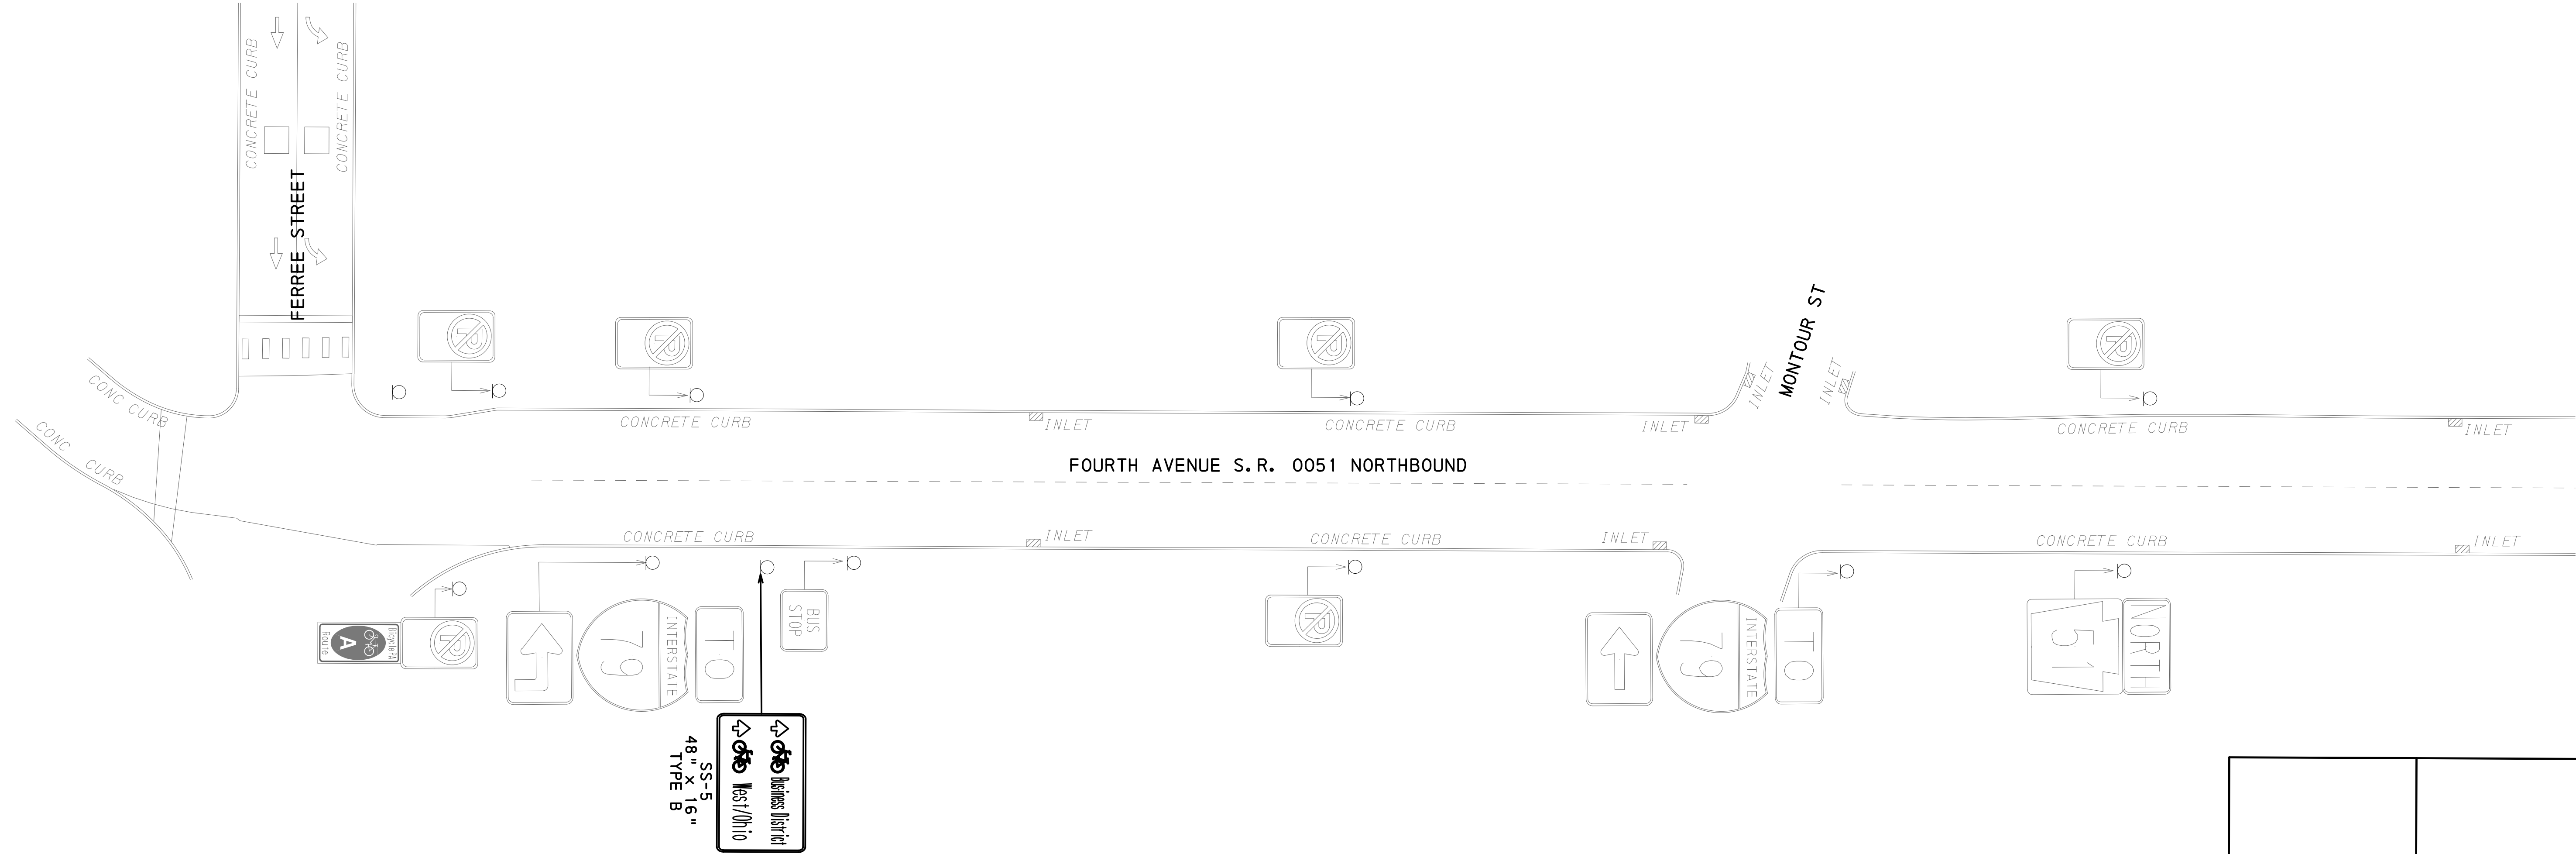
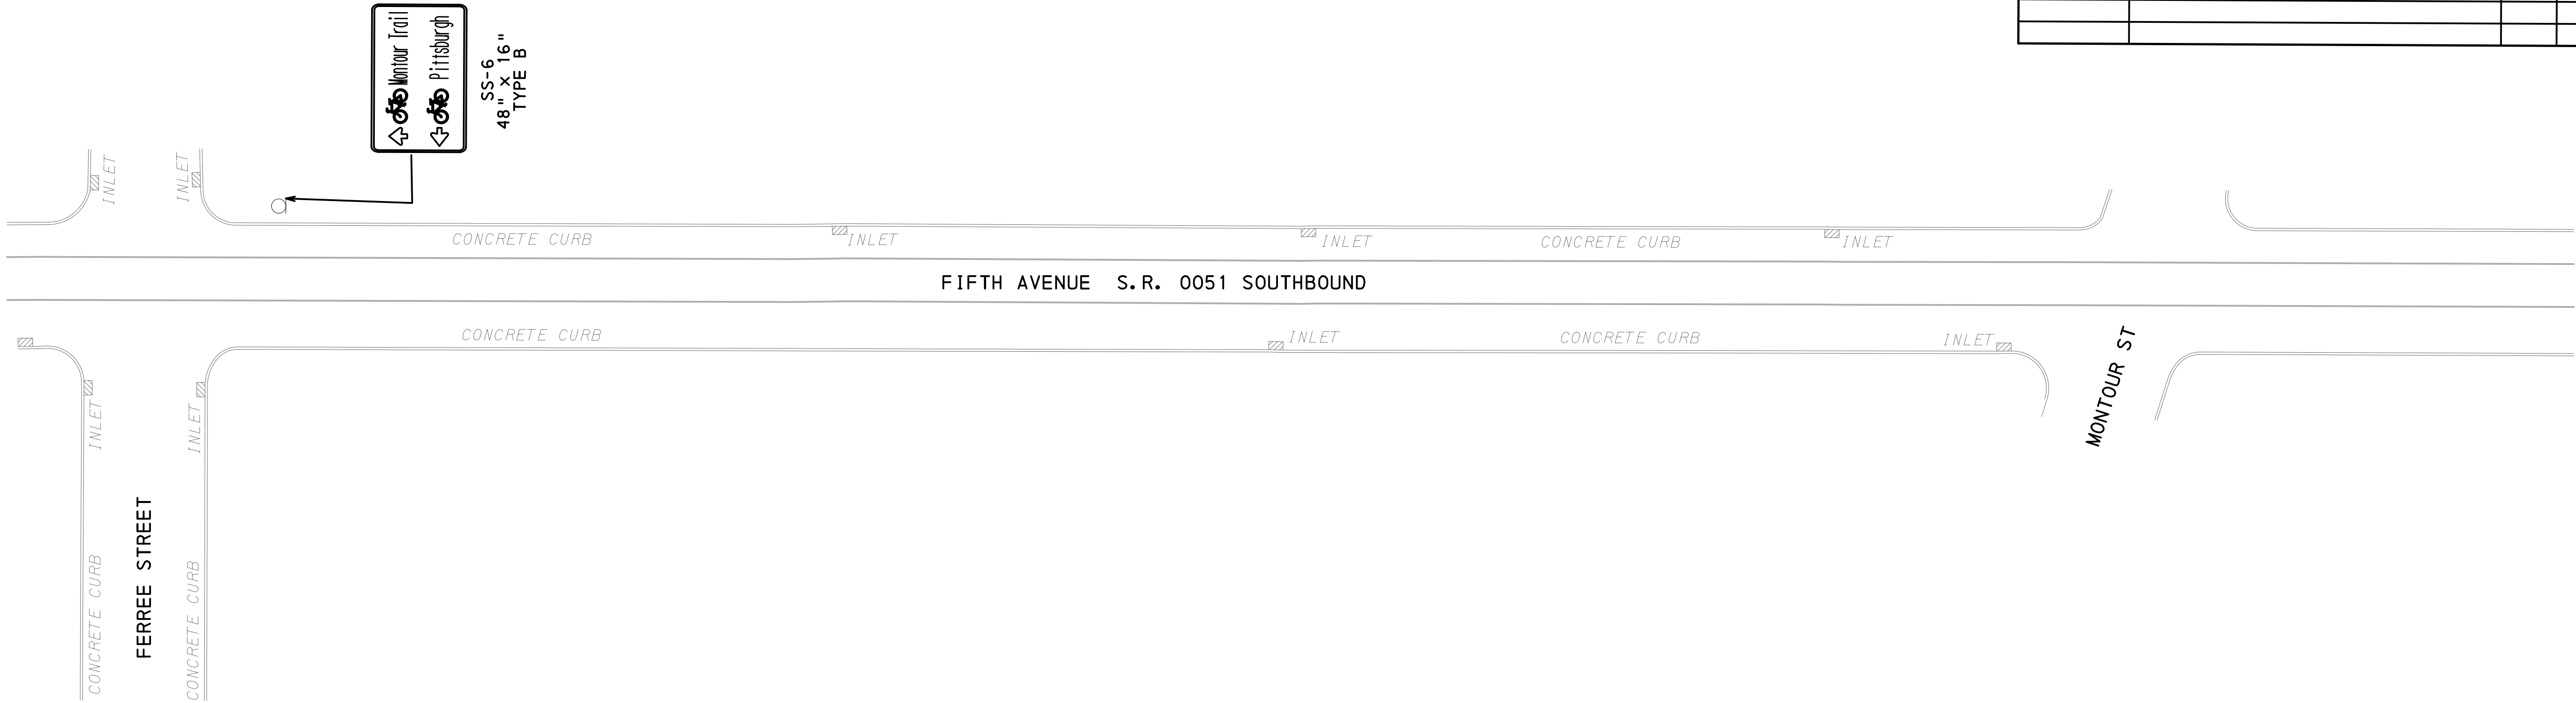
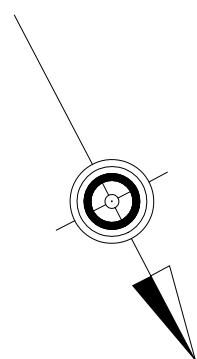


DISTRICT	COUNTY	ROUTE	SECTION	SHEET	
REVISION NUMBER	REVISIONS			DATE	BY

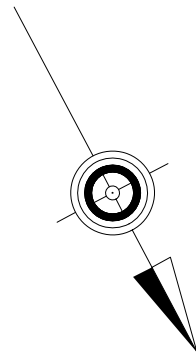

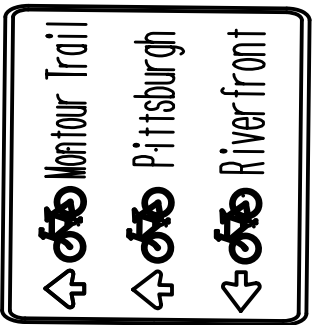


DISTRICT	COUNTY	ROUTE	SECTION	SHEET	
REVISION NUMBER	REVISIONS			DATE	BY

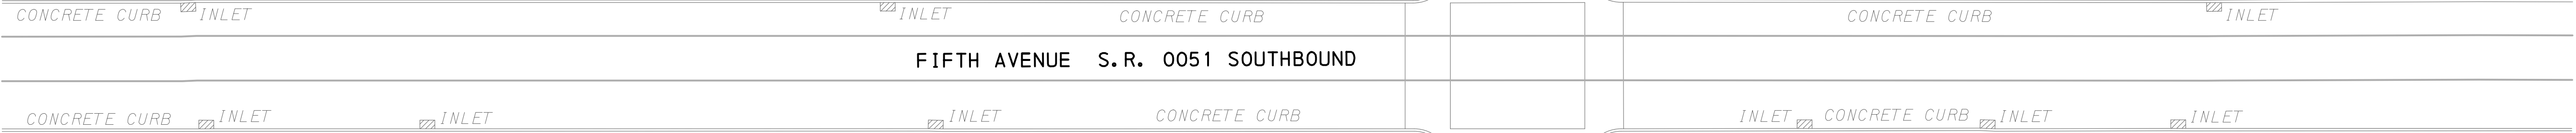

SS-7
48" x 24"
TYPE B




SS-14
48" x 16"
TYPE B

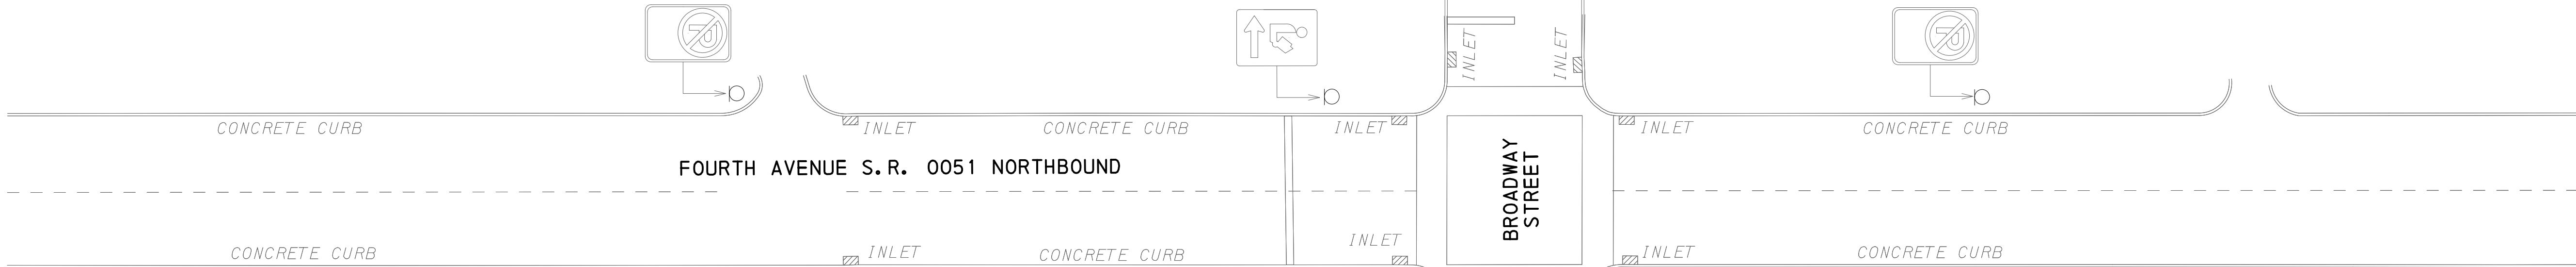



SS-4
48" x 8"
TYPE B





SS-13
48" x 24"
TYPE B

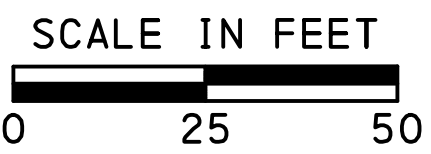




DISTRICT	COUNTY	ROUTE	SECTION	SHEET	
REVISION NUMBER	REVISIONS			DATE	BY

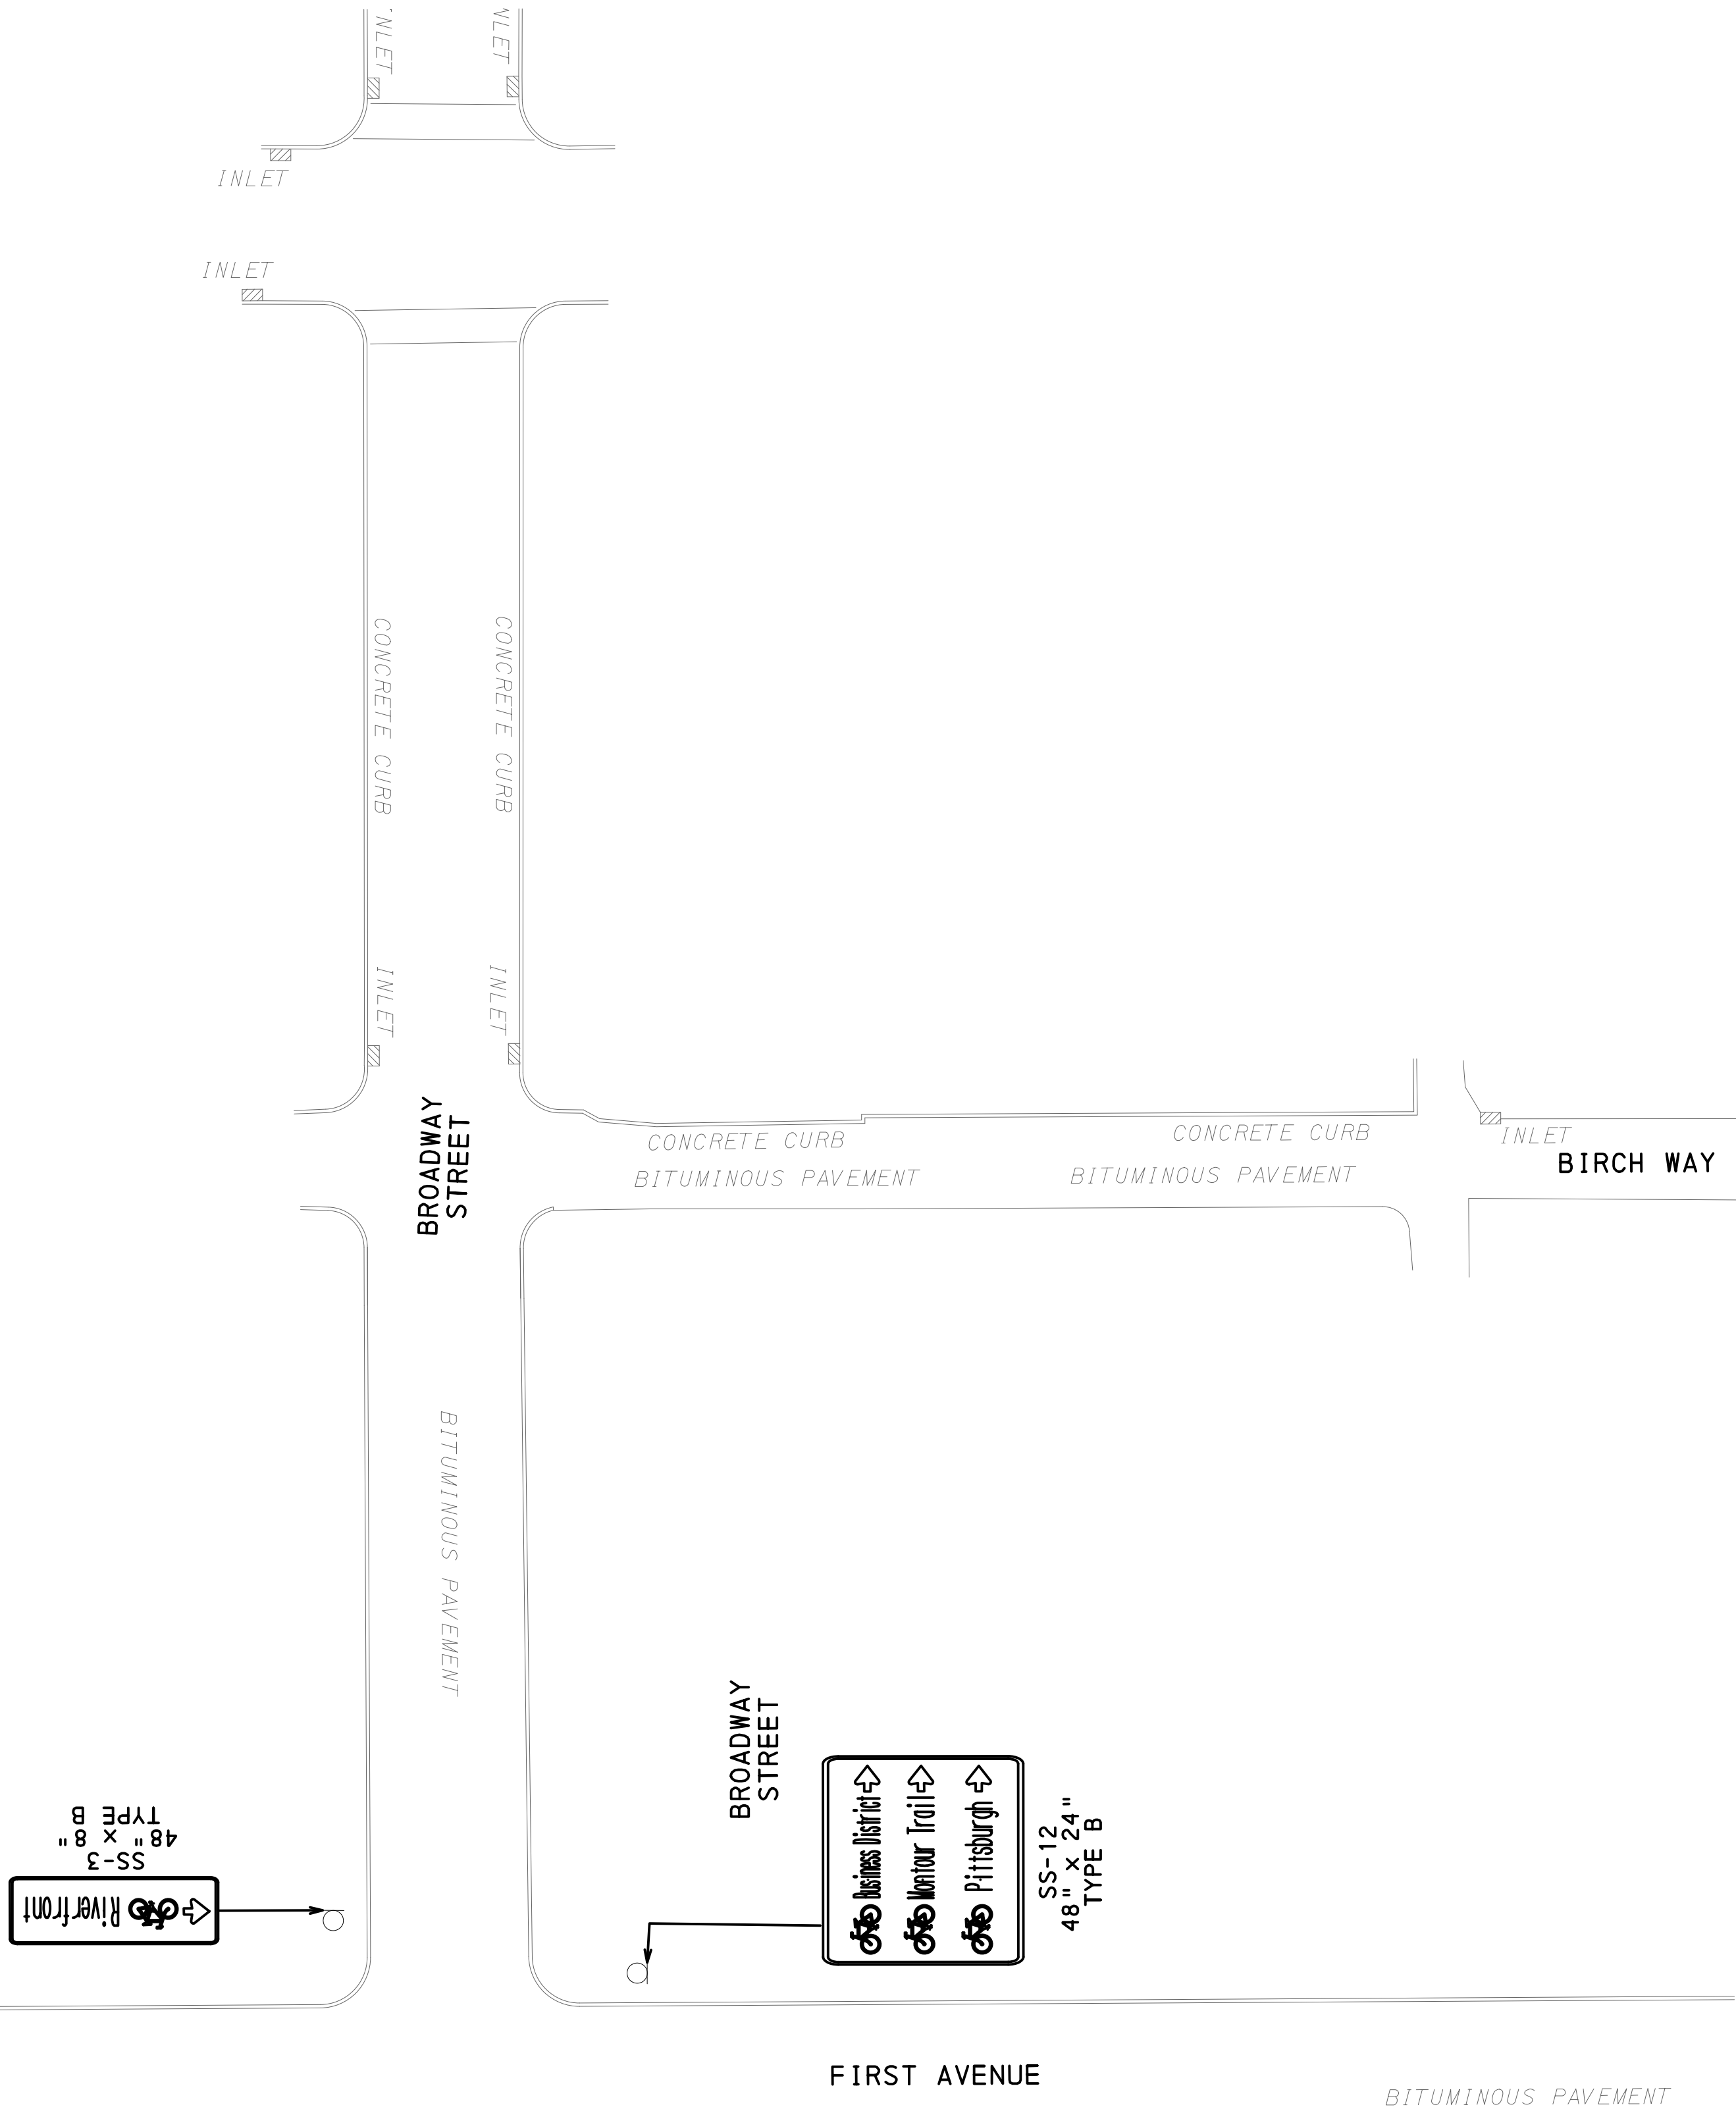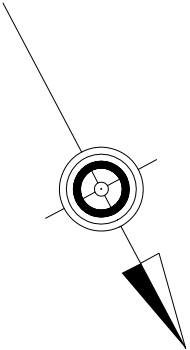



G:\06\N\IND\51xx\5152001\N\5152_SHEETS_WAVE\INDING.dgn 9/26/2016 11:05:46 PM

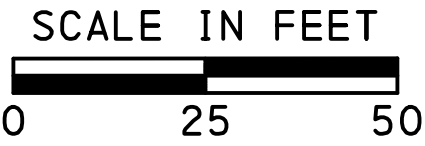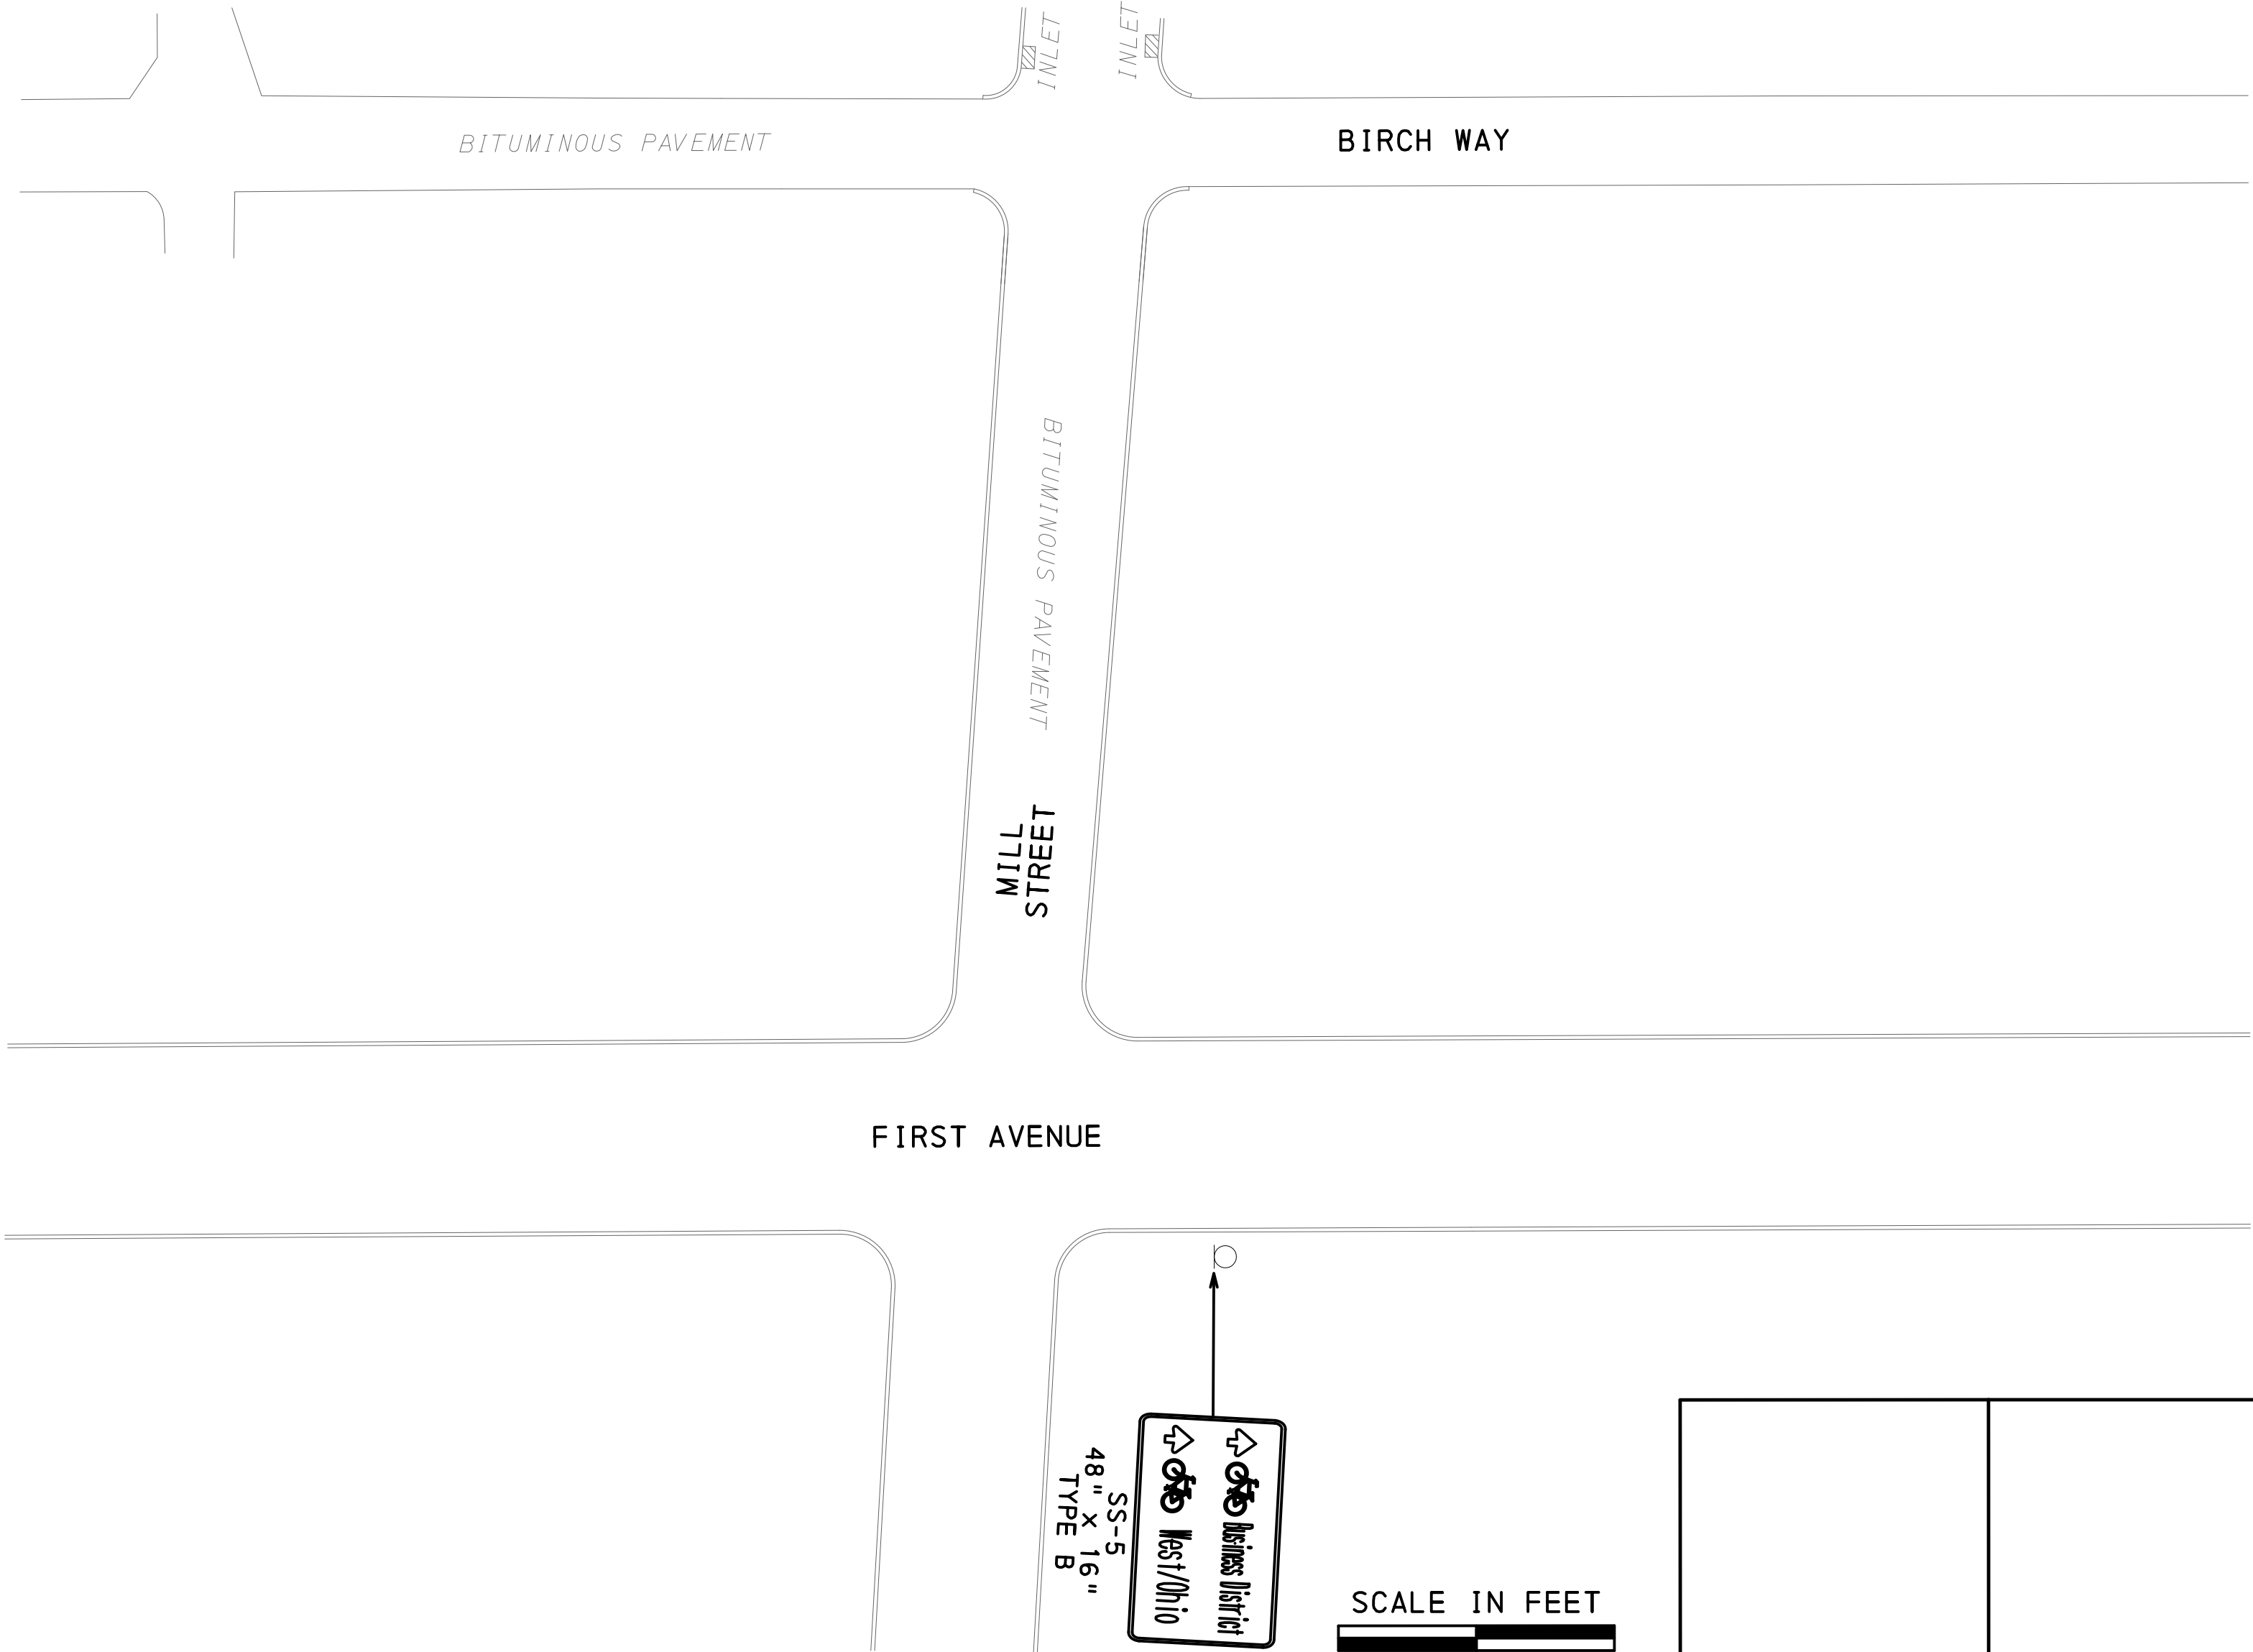

DISTRICT	COUNTY	ROUTE	SECTION	SHEET	
REVISION NUMBER	REVISIONS			DATE	BY

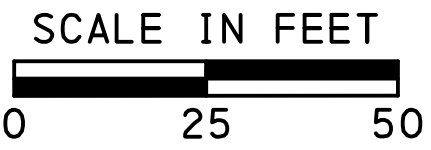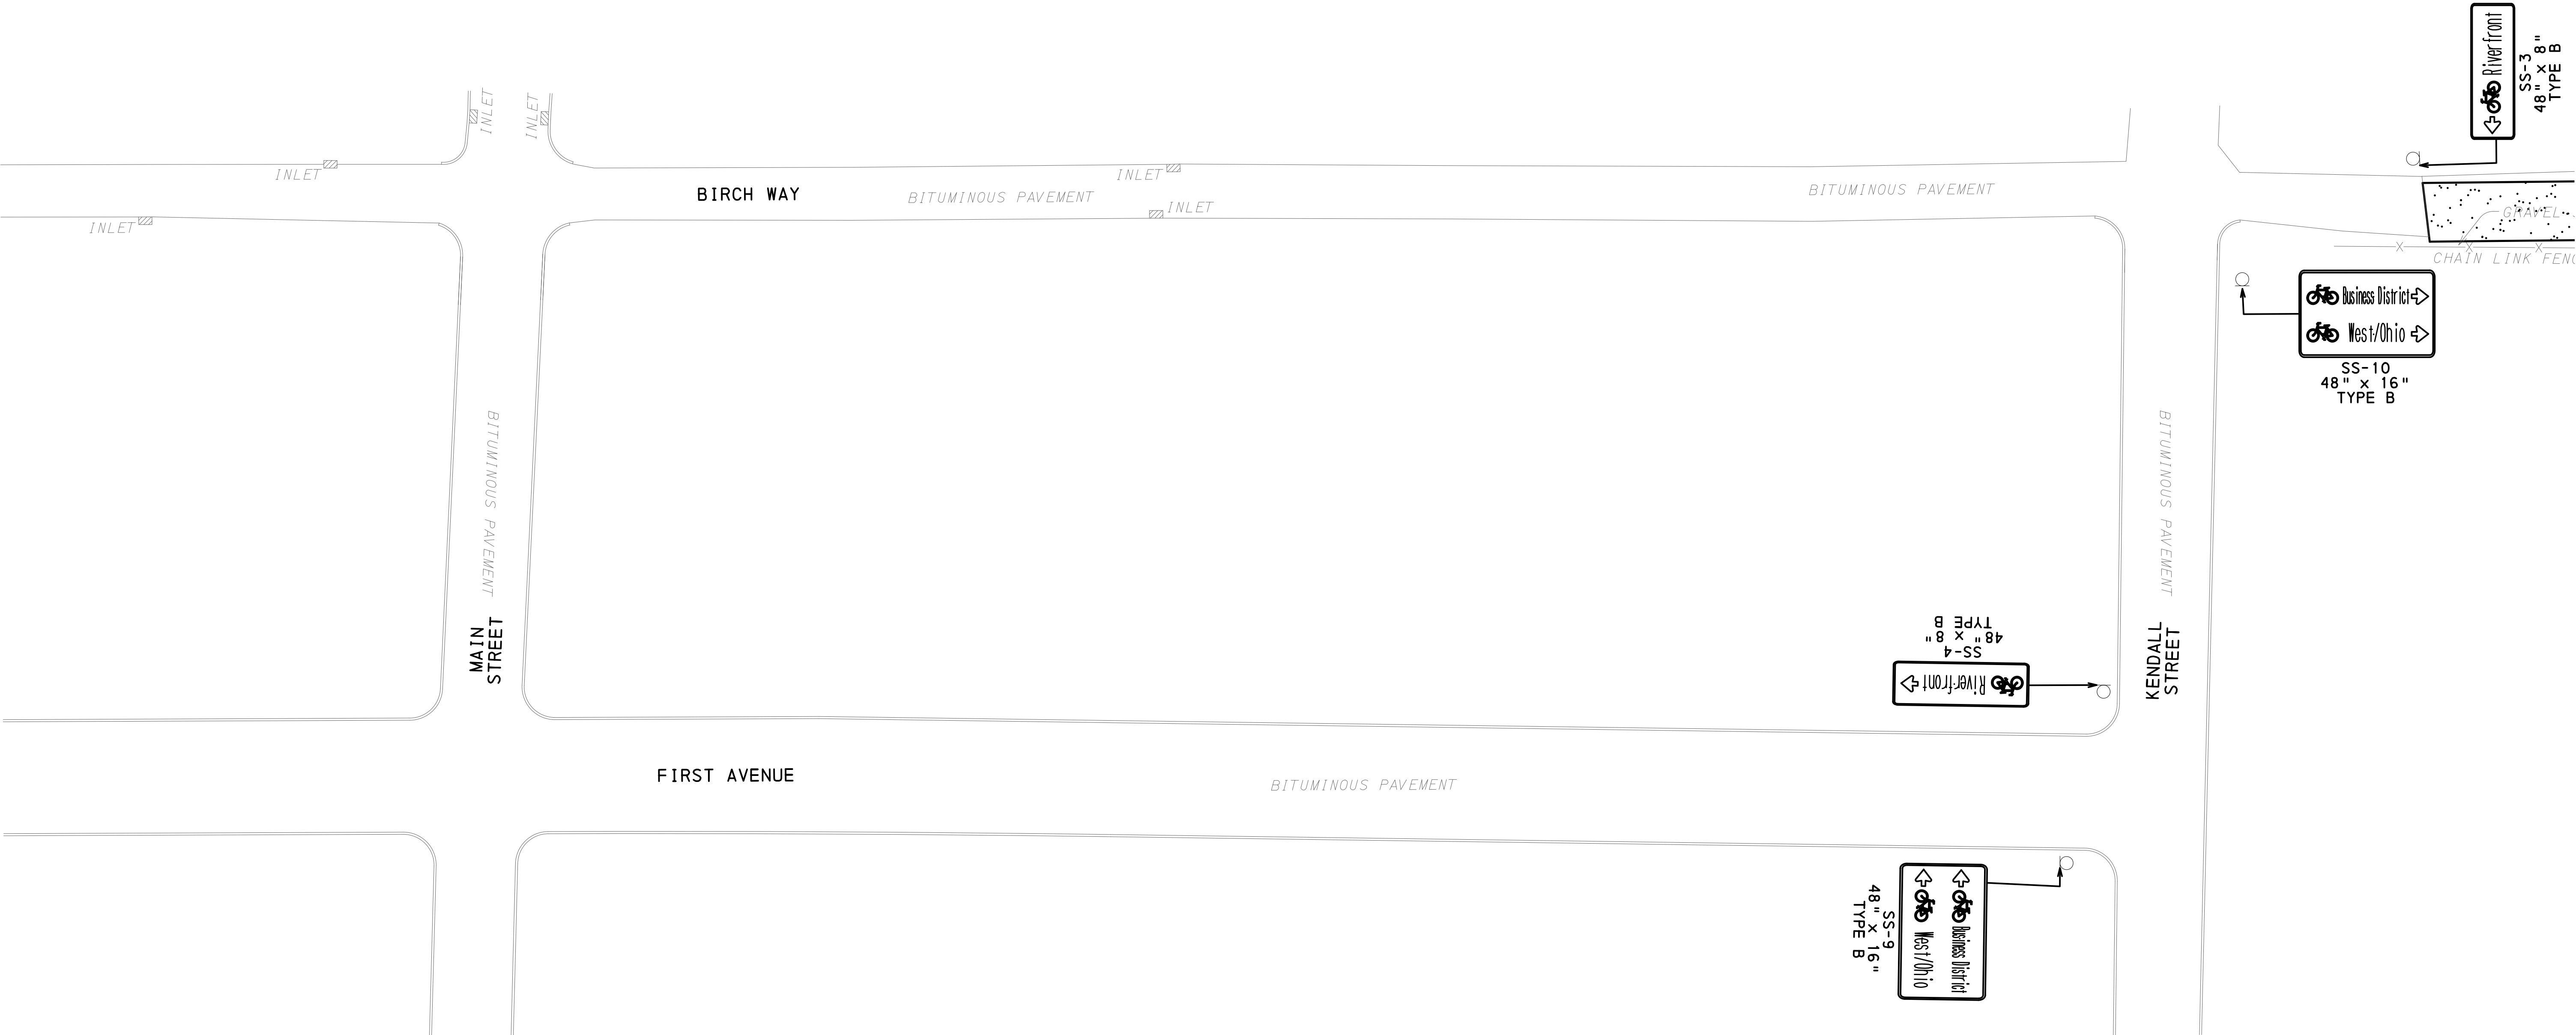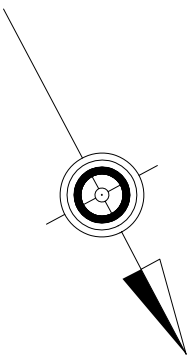

DISTRICT	COUNTY	ROUTE	SECTION	SHEET	
REVISION NUMBER	REVISIONS			DATE	BY

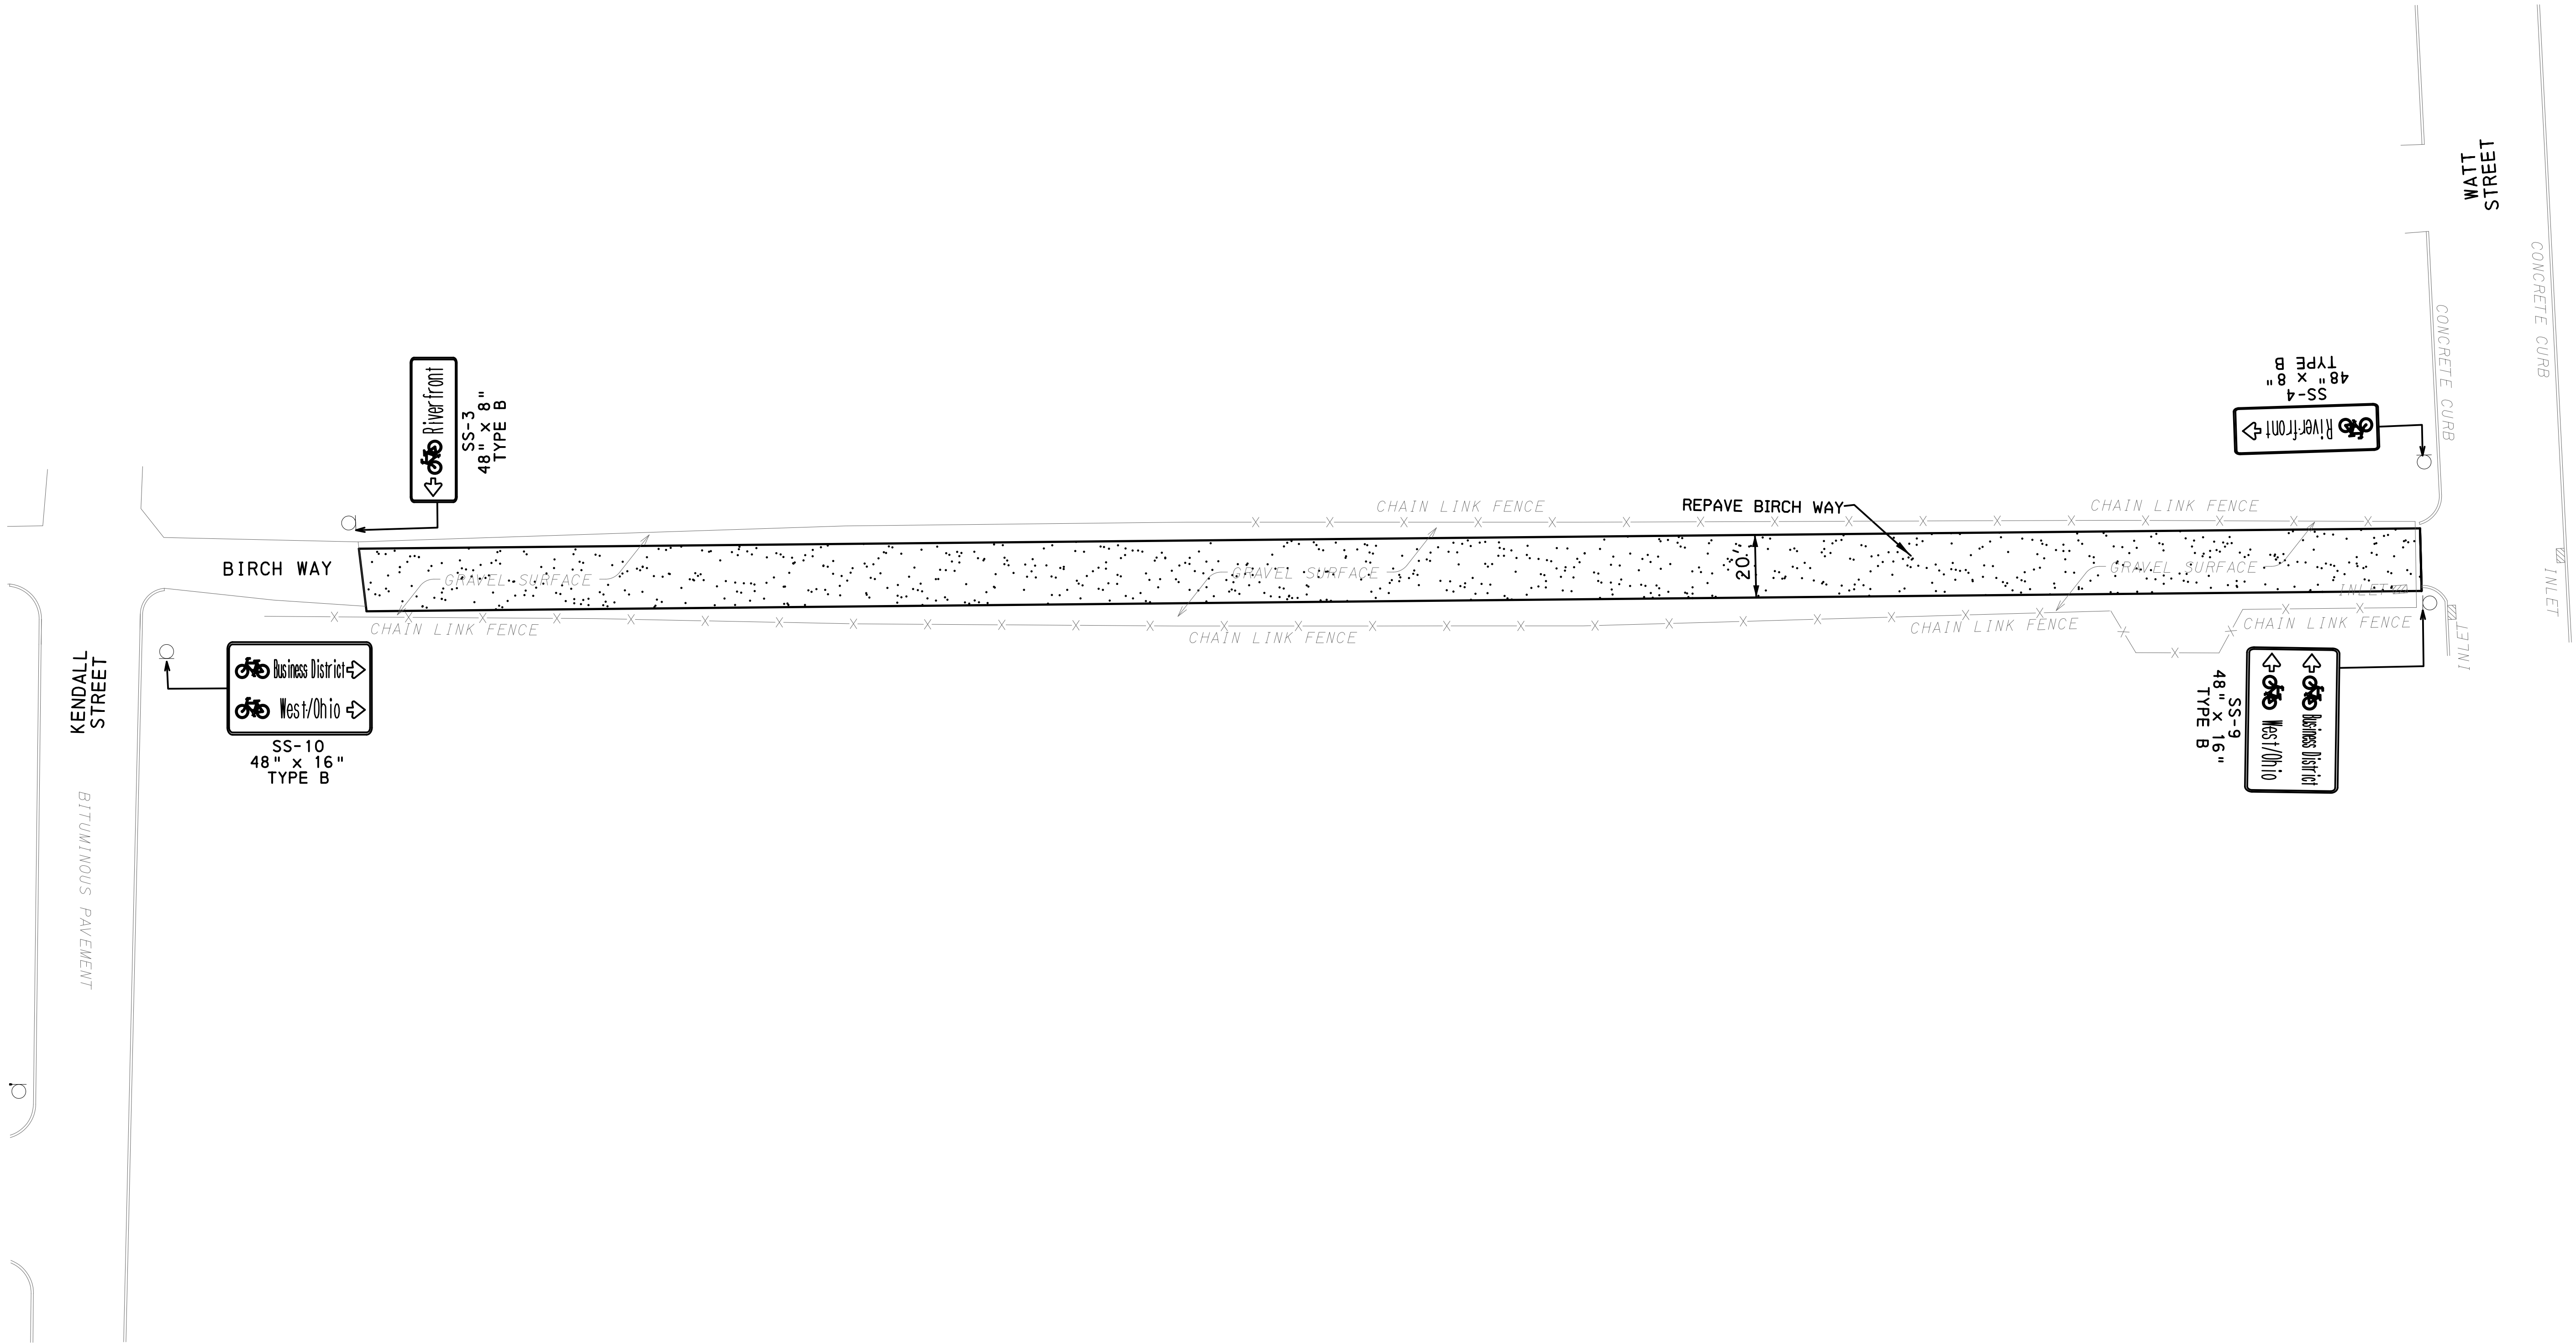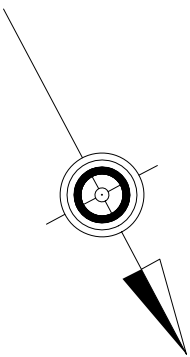

SCALE IN FEET
0 25 50

G:\VGN\IND\51xx\515200\NL5152-SHEETS\WAYFINDING.dgn 9/26/2016 2:49:57 PM

DISTRICT	COUNTY	ROUTE	SECTION	SHEET	
REVISION NUMBER	REVISIONS			DATE	BY



DISTRICT	COUNTY	ROUTE	SECTION	SHEET	
REVISION NUMBER	REVISIONS			DATE	BY

