



OPERATOR: G:\ds3\0051 A93 Fifth Ave. (Coraopolis)\Design\020051A93 (BICYCLE) Signing Pavement Marking.dgn

PLOTTED:06-MAY-2016 12:59


D-9012 CADD (02-90) REVISED (10-04)

SIGNING AND PAVEMENT MARKING PLAN

DISTRICT	COUNTY	ROUTE	SECTION	SHEET	
11-0	ALLEGHENY	0051	A93	6 OF 17	
MOON TOWNSHIP, CORAOPOLIS BOROUGH					
REV NO	REVISIONS			DATE	BY APPD

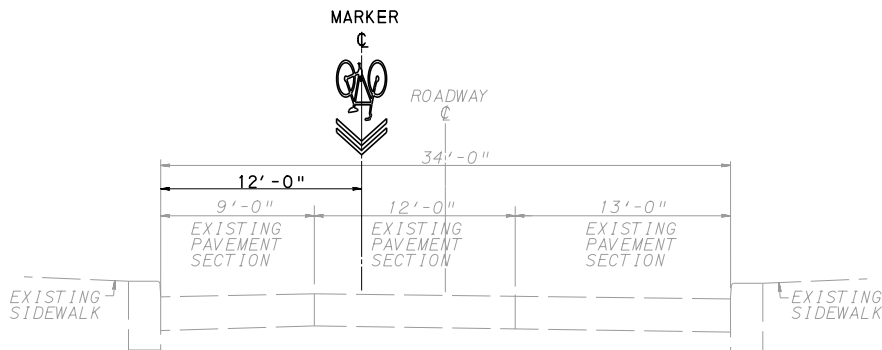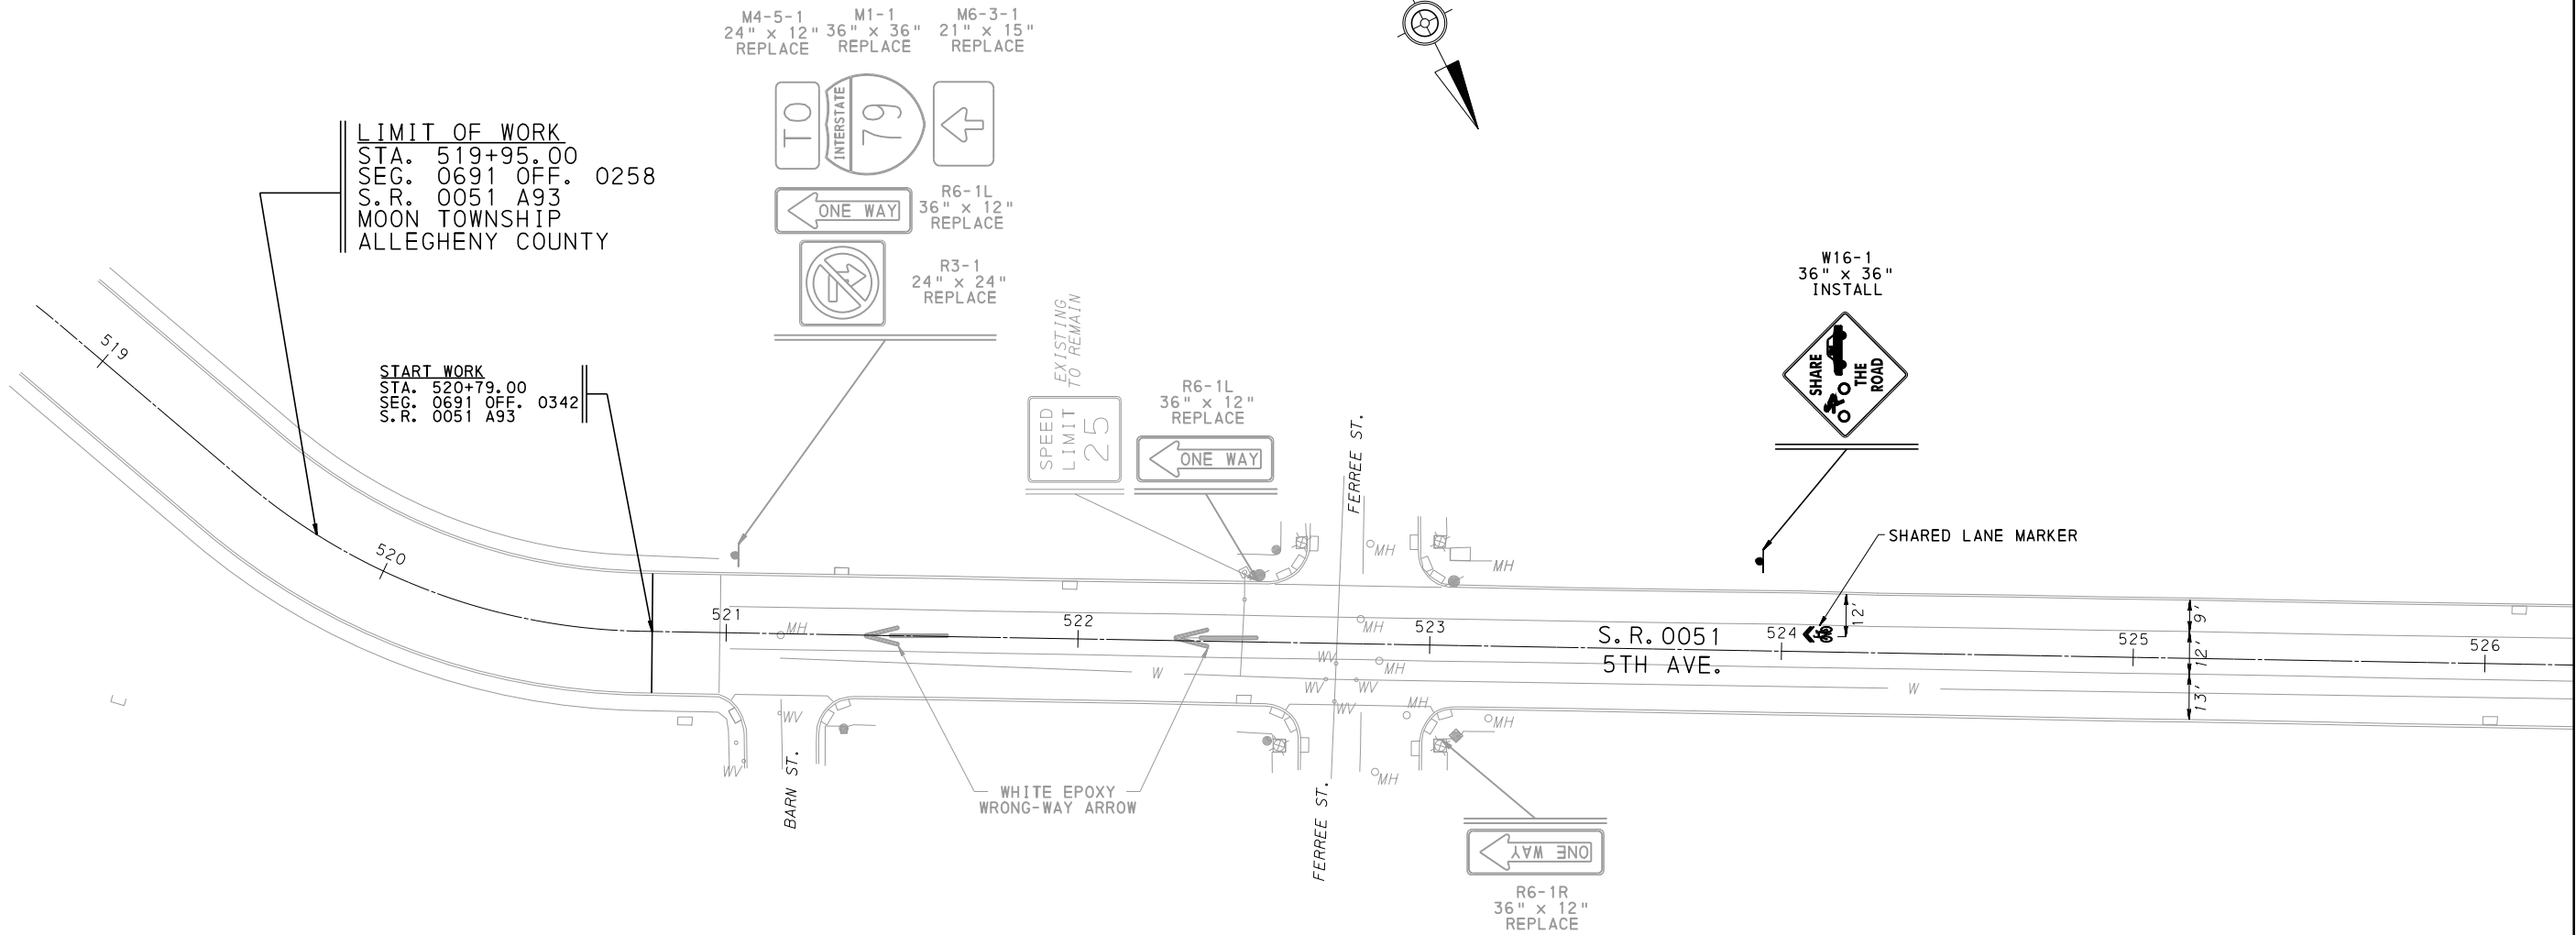

**SHARED LANE MARKER
LOCATION DETAIL**
SEE TC-8600 FOR MARKER DIMENSIONS
MARKER TO BE PLACED 12' INSIDE
RIGHT CURB SOUTHBOUND DIRECTION

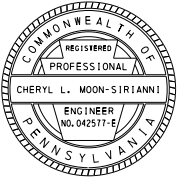

SIGNING AND PAVEMENT MARKING PLAN

DISTRICT	COUNTY	ROUTE	SECTION	SHEET	
11-0	ALLEGHENY	0051	A93	7 OF 17	
MOON TOWNSHIP, CORAOPOLIS BOROUGH					
REV NO	REVISIONS			DATE	BY APPD

W16-1
36" x 36"
INSTALL



M4-5-1 24" x 12" REPLACE
M1-1 36" x 36" REPLACE
M6-3-1 21" x 15" REPLACE



R6-1L
36" x 12"
REPLACE



EXISTING
TO REMAIN



SHARED LANE MARKER


SHARED LANE MARKER

SHARED LANE MARKER


R6-1R
36" x 12"
REPLACE



R1-1
24" x 24"
REPLACE

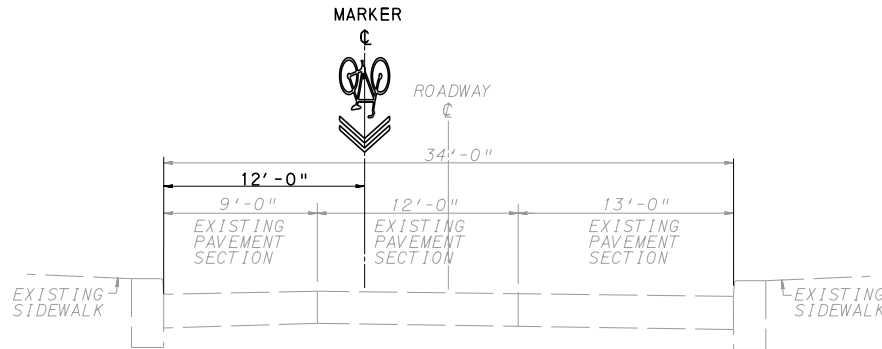

SHARED LANE MARKER
LOCATION DETAIL
SEE TC-8600 FOR MARKER DIMENSIONS
MARKER TO BE PLACED 12' INSIDE
RIGHT CURB SOUTHBOUND DIRECTION

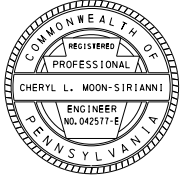

OPERATOR: G:\ds3\0051 A93 Fifth Ave. (Coraopolis)\Design\020051A93 (BICYCLE) Signing Pavement Marking.dgn
FILE NAME: G:\ds3\0051 A93 Fifth Ave. (Coraopolis)\Design\020051A93 (BICYCLE) Signing Pavement Marking.dgn
D-9012 CADD (02-90) REVISED (10-04) PLOTTED:06-MAY-2016 12:59



OPERATOR: G:\ds3\0051 A93 Fifth Ave. (Coraopolis)\Design\020051A93 (BICYCLE) Signing Pavement Marking.dgn

D-9012 CADD (02-90) REVISED (10-04)


PLOTTED:06-MAY-2016 12:59

SIGNING AND PAVEMENT MARKING PLAN

DISTRICT	COUNTY	ROUTE	SECTION	SHEET	
11-0	ALLEGHENY	0051	A93	8 OF 17	
MOON TOWNSHIP, CORAOPOLIS BOROUGH					
REV NO	REVISIONS			DATE	BY APPD

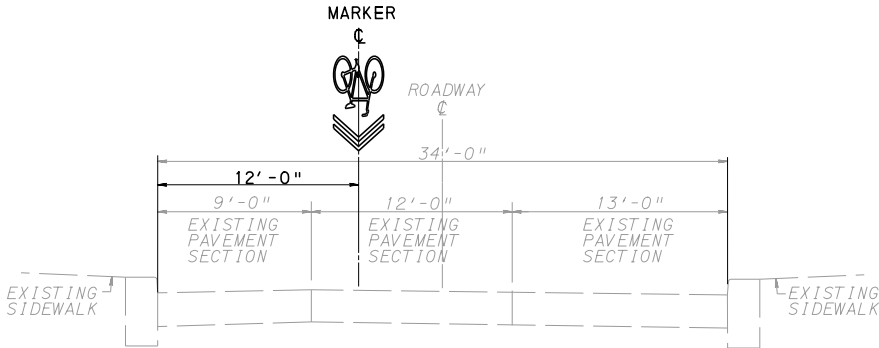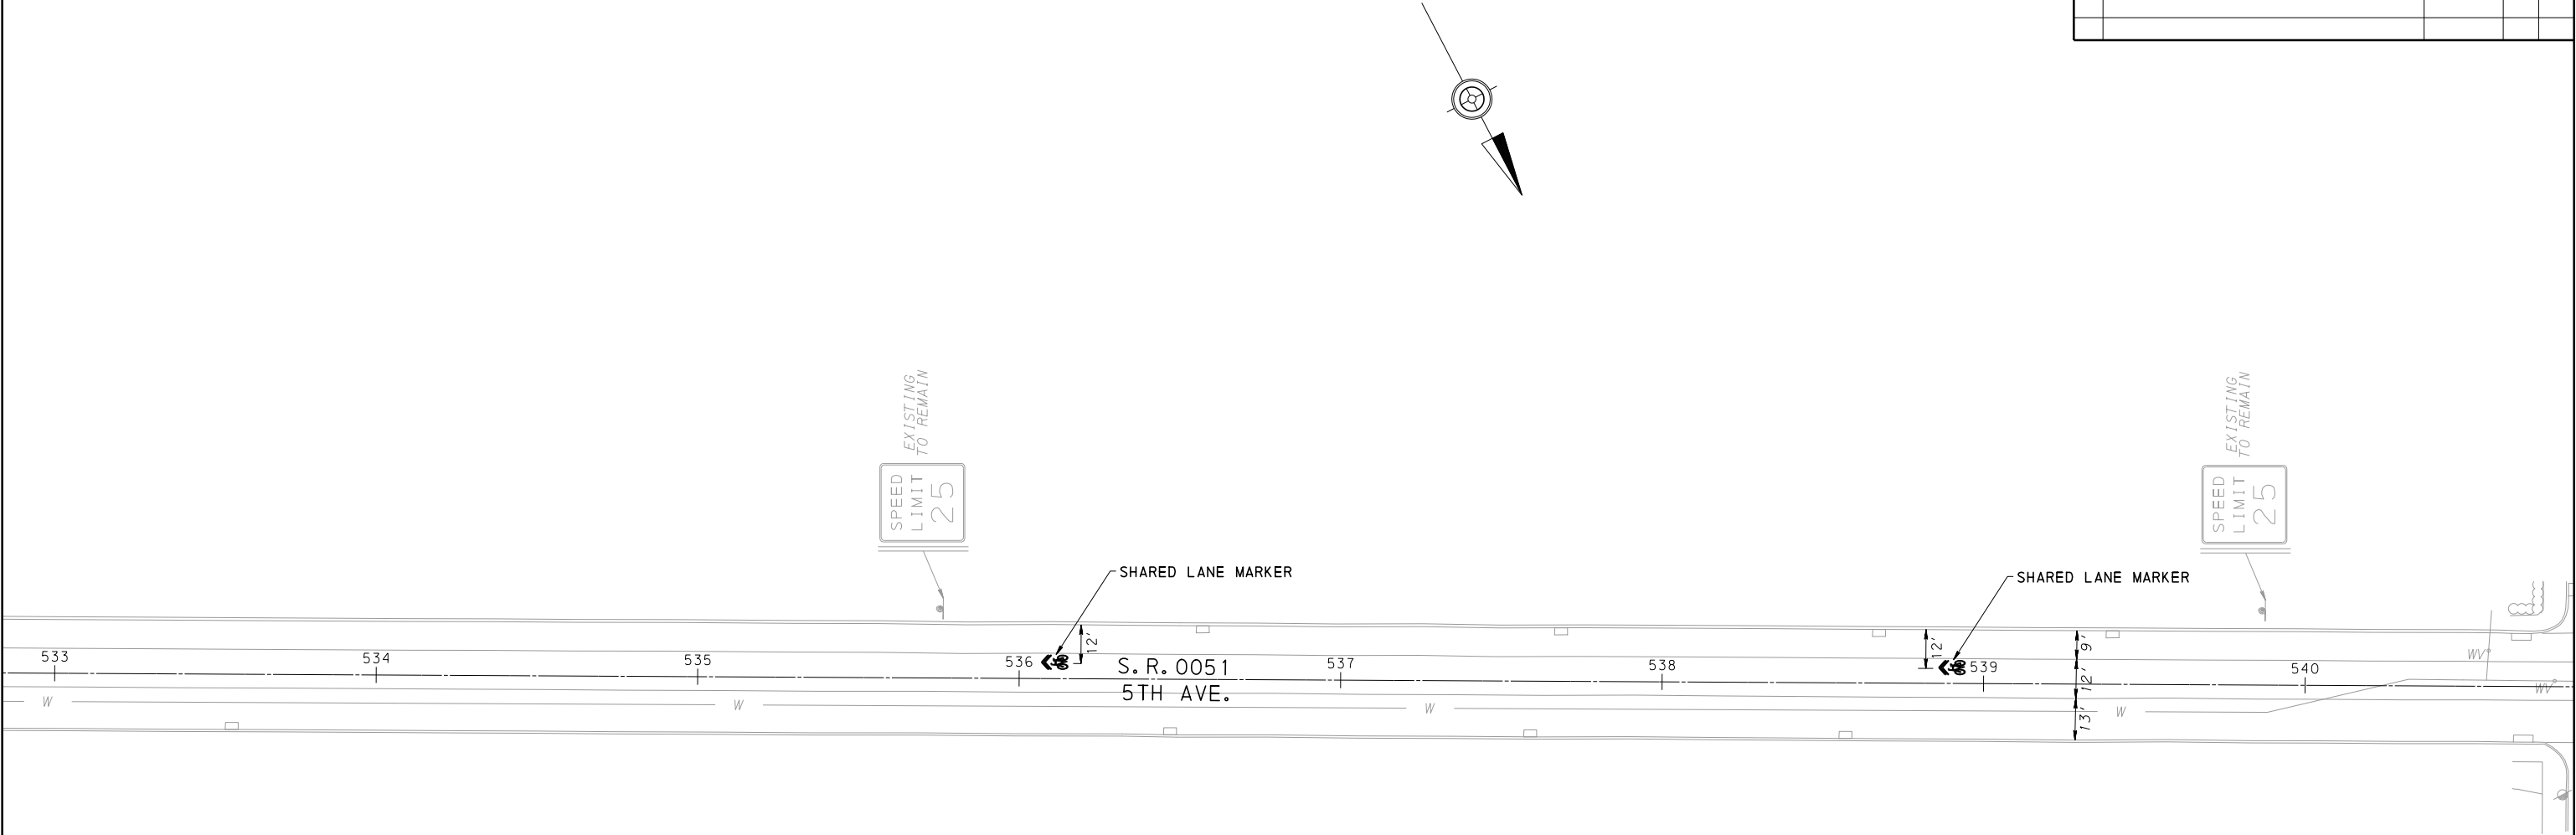

**SHARED LANE MARKER
LOCATION DETAIL**
SEE TC-8600 FOR MARKER DIMENSIONS
MARKER TO BE PLACED 12' INSIDE
RIGHT CURB SOUTHBOUND DIRECTION

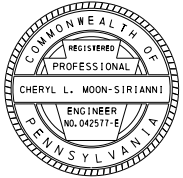



OPERATOR: G:\ds3\0051 A93 Fifth Ave. (Coraopolis)\Design\020051A93 (BICYCLE) Signing Pavement Marking.dgn

D-9012 CADD (02-90) REVISED (10-04)


PLOTTED:06-MAY-2016 12:59

SIGNING AND PAVEMENT MARKING PLAN

DISTRICT	COUNTY	ROUTE	SECTION	SHEET	
11-0	ALLEGHENY	0051	A93	9 OF 17	
MOON TOWNSHIP, CORAOPOLIS BOROUGH					
REV NO	REVISIONS			DATE	BY APPD

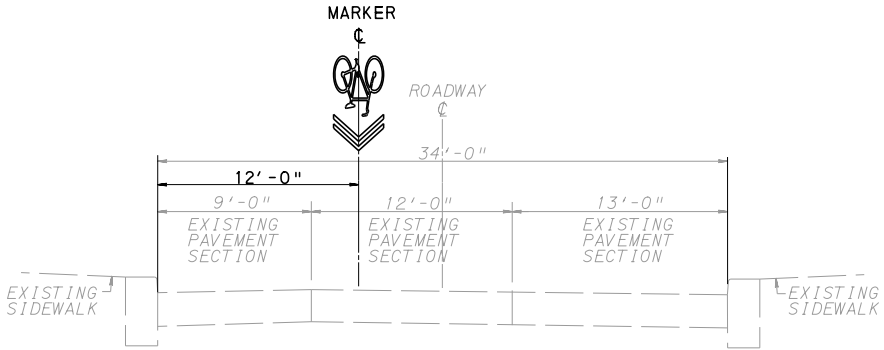
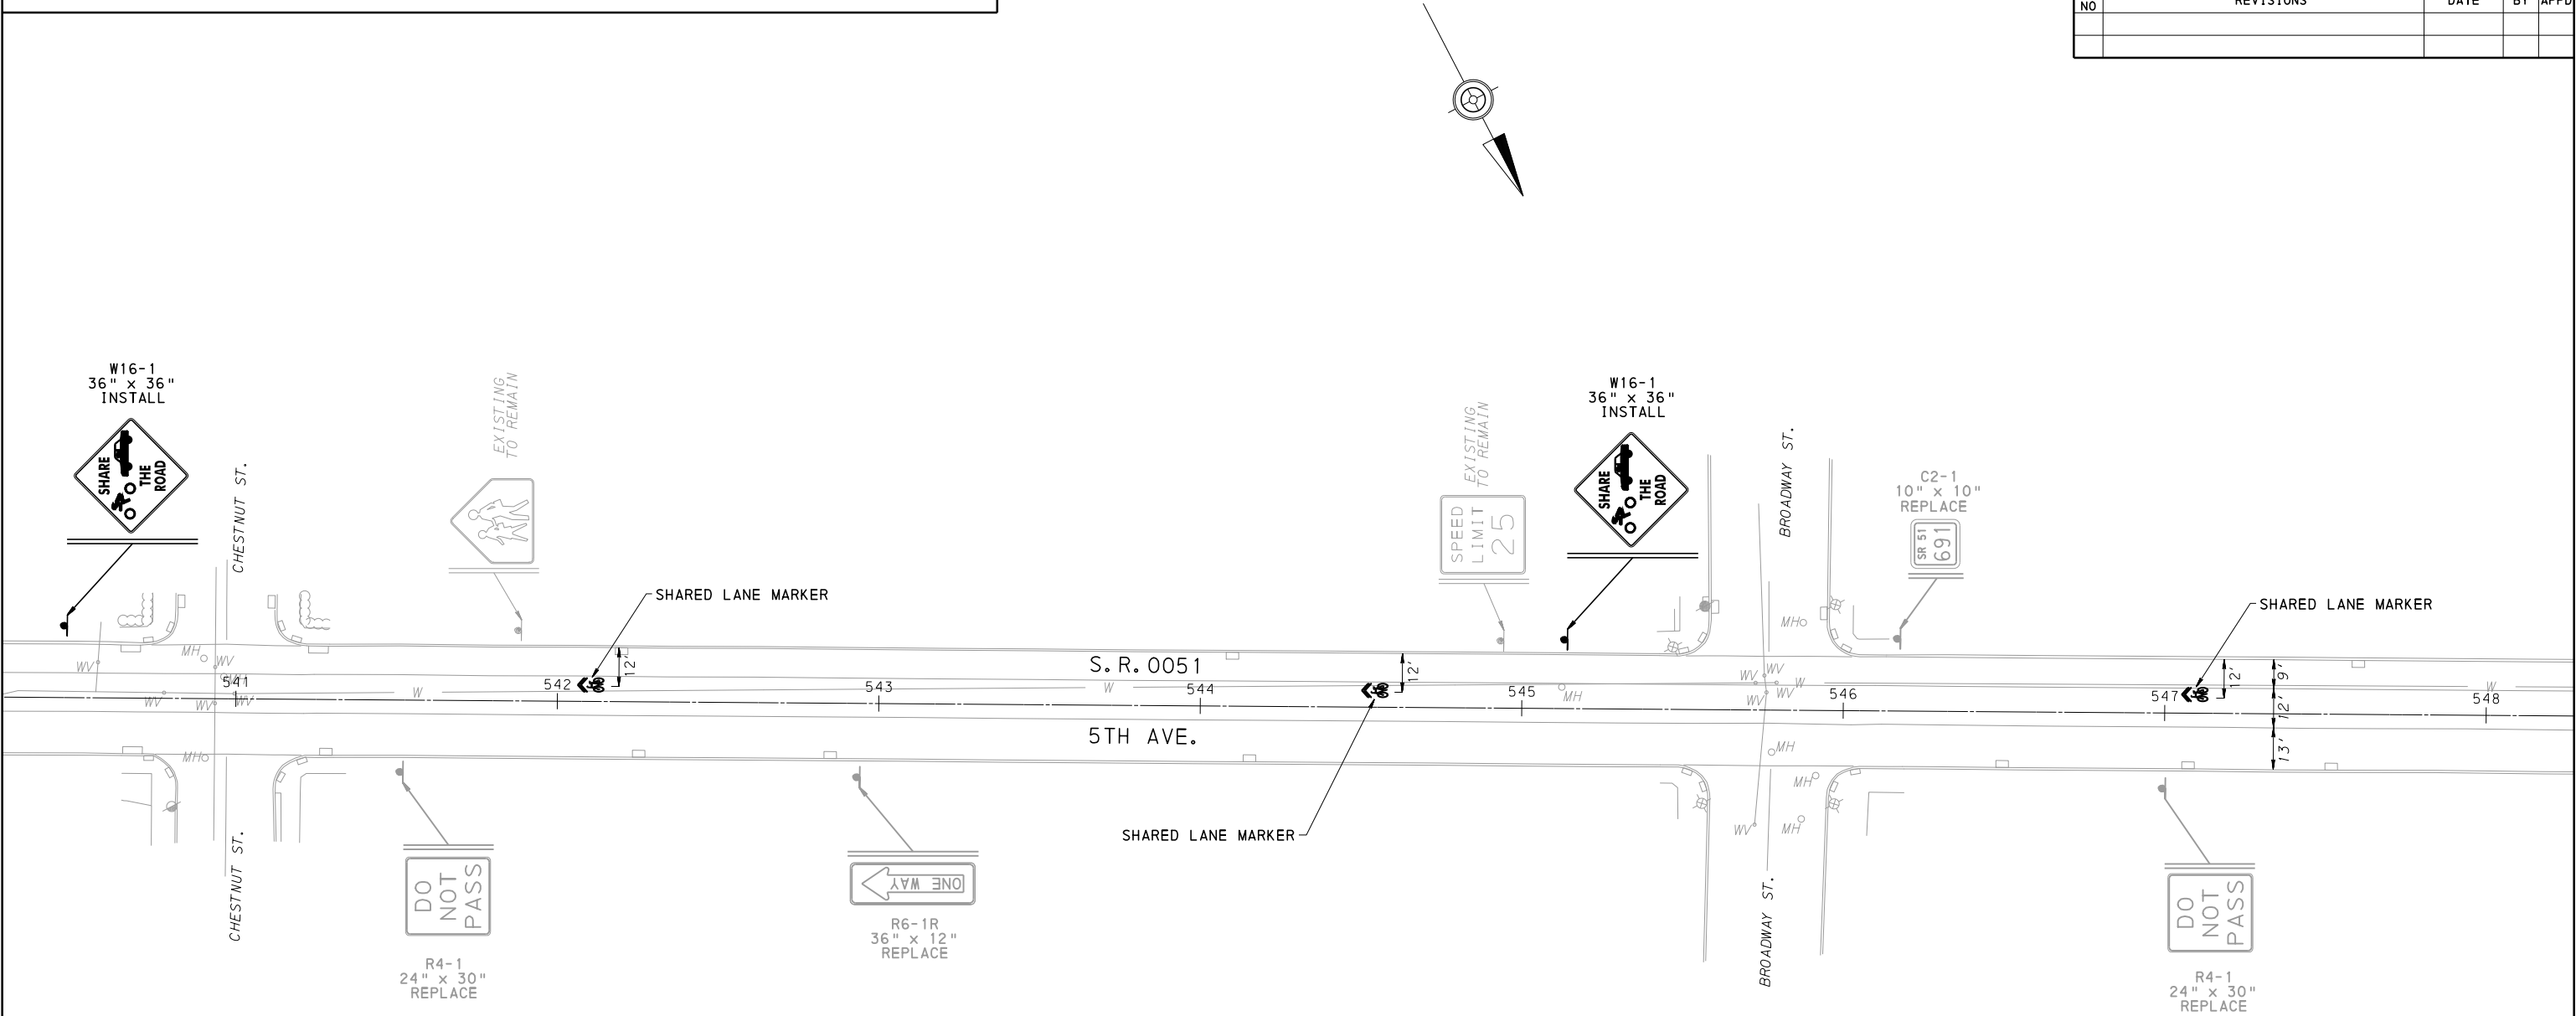


**SHARED LANE MARKER
LOCATION DETAIL**
SEE TC-8600 FOR MARKER DIMENSIONS
MARKER TO BE PLACED 12' INSIDE
RIGHT CURB SOUTHBOUND DIRECTION

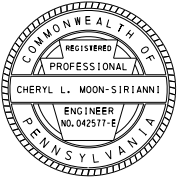


SIGNING AND PAVEMENT MARKING PLAN

DISTRICT	COUNTY	ROUTE	SECTION	SHEET	
11-0	ALLEGHENY	0051	A93	10 OF 17	
MOON TOWNSHIP, CORAOPOLIS BOROUGH					
REV NO	REVISIONS			DATE	BY APPD

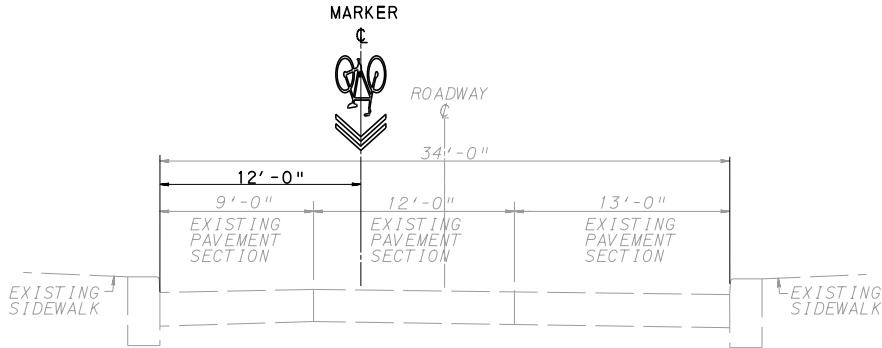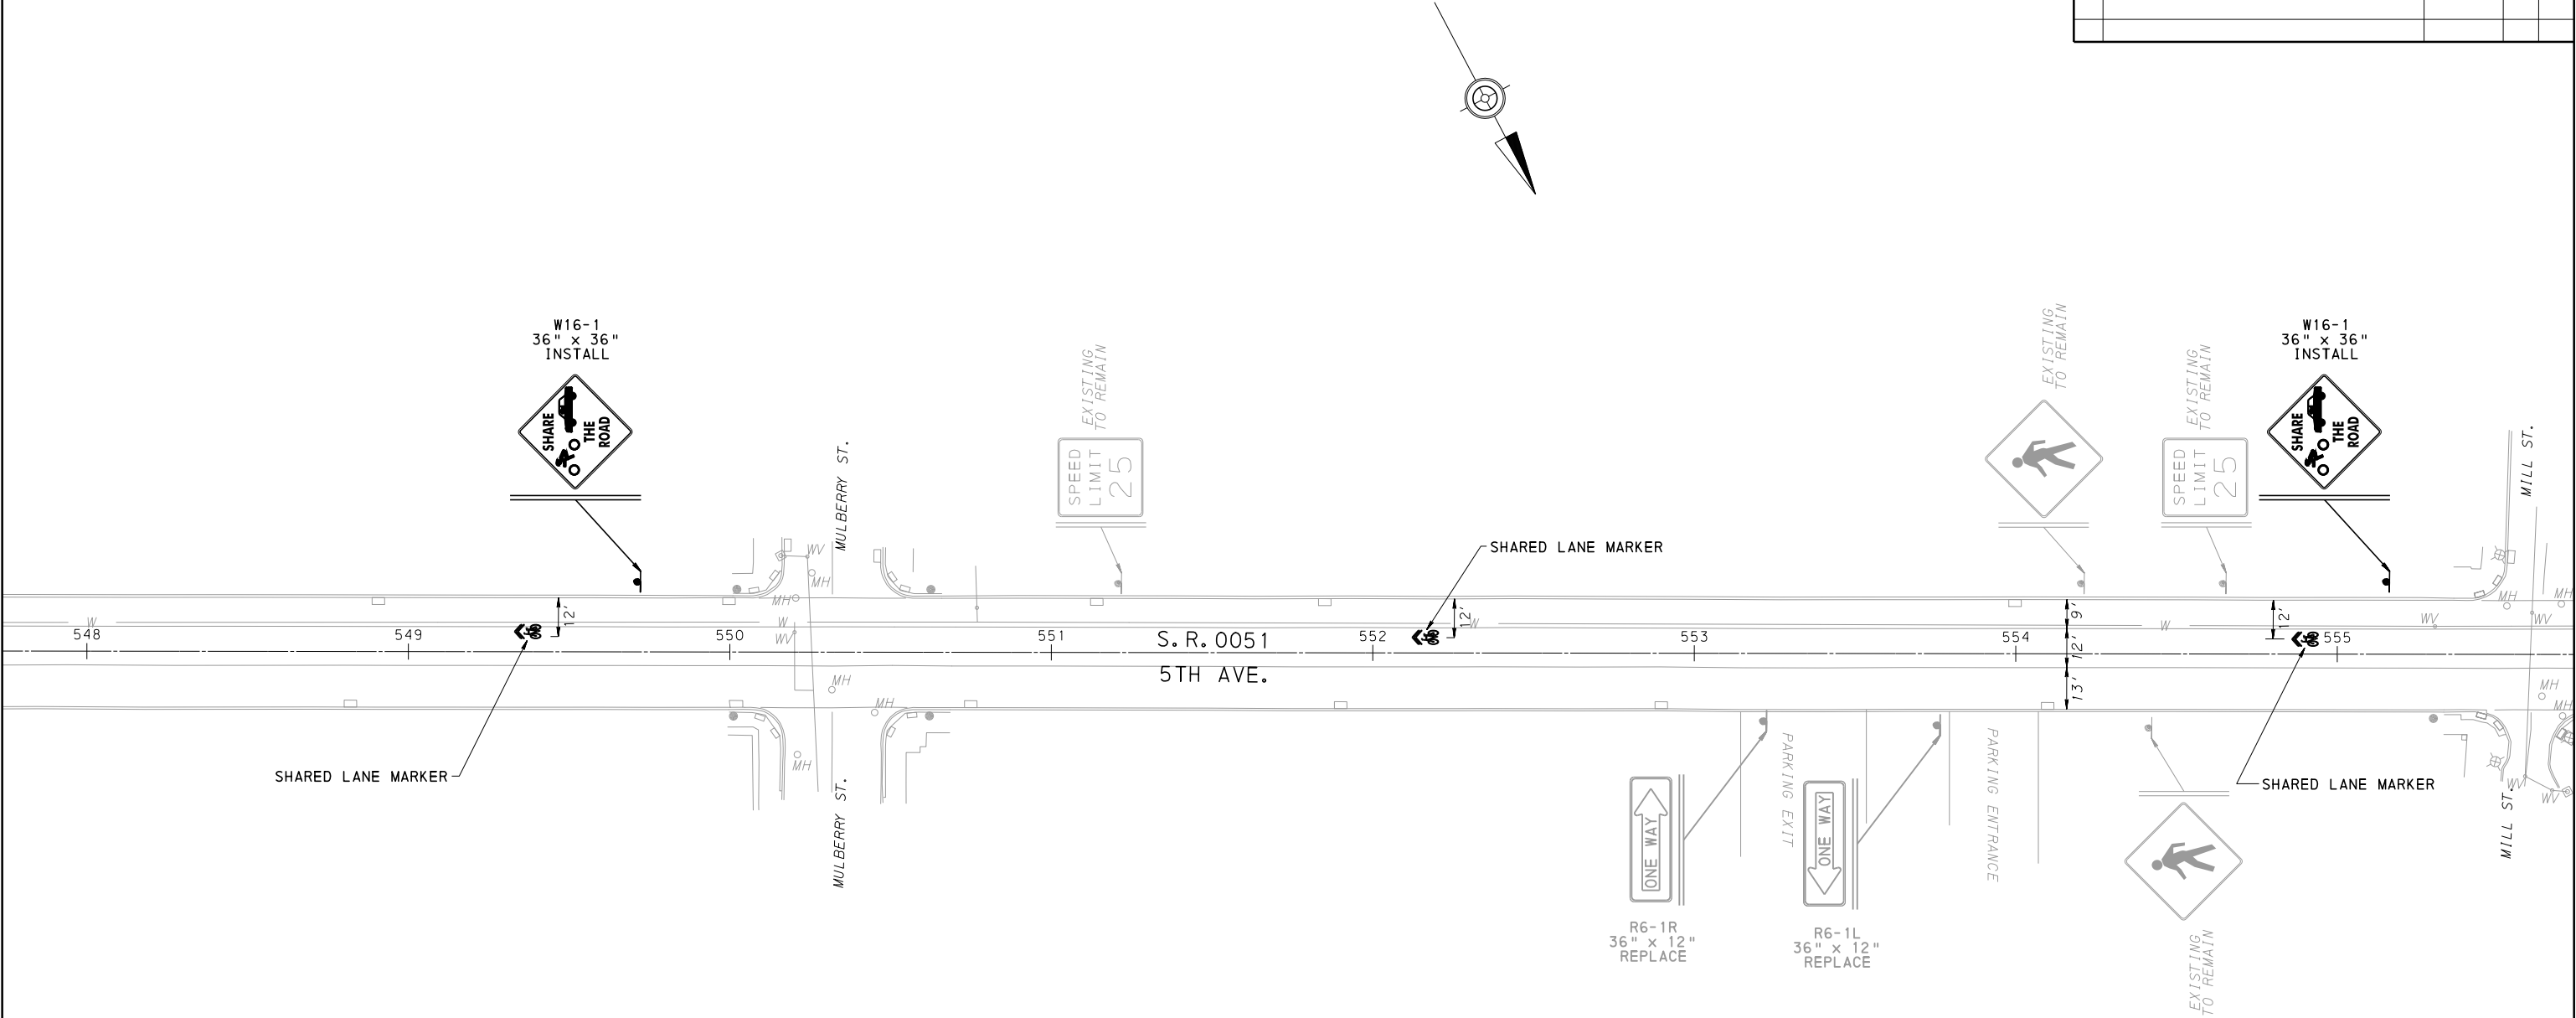

SHARED LANE MARKER
LOCATION DETAIL
SEE TC-8600 FOR MARKER DIMENSIONS
MARKER TO BE PLACED 12' INSIDE
RIGHT CURB SOUTHBOUND DIRECTION

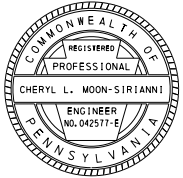

OPERATOR: G:\ds3\0051 A93 Fifth Ave. (Coraopolis)\Design\020051A93 (BICYCLE) Signing Pavement Marking.dgn

PLOTTED:06-MAY-2016 12:59

D-9012 CADD (02-90) REVISED (10-04)



OPERATOR: G:\ds3\0051 A93 Fifth Ave. (Coraopolis)\Design\020051A93 (BICYCLE) Signing Pavement Marking.dgn

D-9012 CADD (02-90) REVISED (10-04)


PLOTTED:06-MAY-2016 12:59

SIGNING AND PAVEMENT MARKING PLAN

DISTRICT	COUNTY	ROUTE	SECTION	SHEET
11-0	ALLEGHENY	0051	A93	11 OF 17
MOON TOWNSHIP, CORAOPOLIS BOROUGH				
REV NO	REVISIONS	DATE	BY	APPD

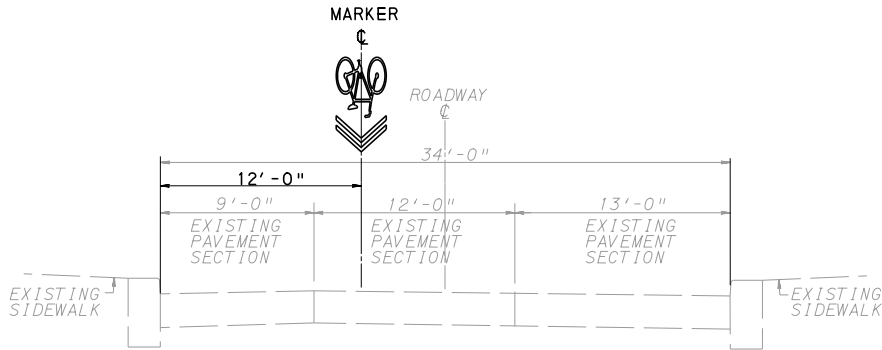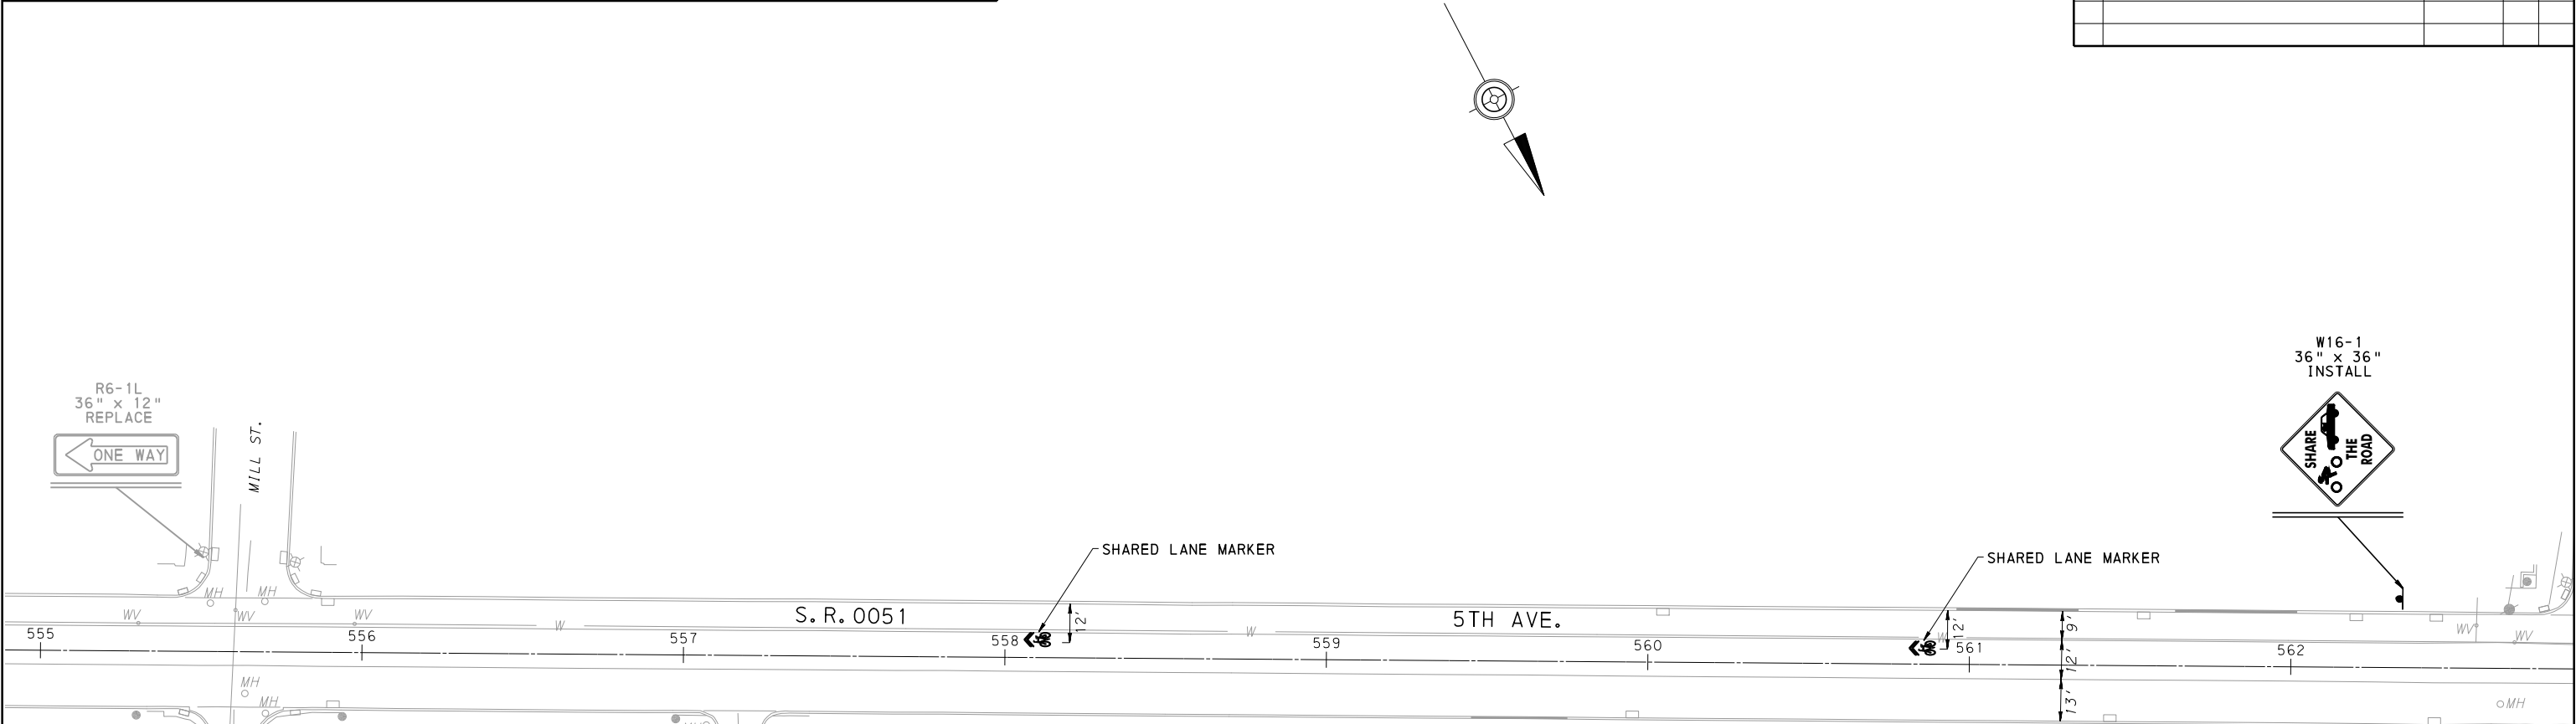

**SHARED LANE MARKER
LOCATION DETAIL**
SEE TC-8600 FOR MARKER DIMENSIONS
MARKER TO BE PLACED 12' INSIDE
RIGHT CURB SOUTHBOUND DIRECTION

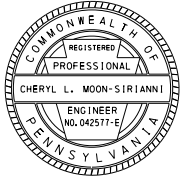



OPERATOR: G:\ds3\0051 A93 Fifth Ave. (Coraopolis)\Design\020051A93 (BICYCLE) Signing Pavement Marking.dgn

D-9012 CADD (02-90) REVISED (10-04)


PLOTTED:06-MAY-2016 12:59

SIGNING AND PAVEMENT MARKING PLAN

DISTRICT	COUNTY	ROUTE	SECTION	SHEET
11-0	ALLEGHENY	0051	A93	12 OF 17
MOON TOWNSHIP, CORAOPOLIS BOROUGH				
REV NO	REVISIONS	DATE	BY	APPD

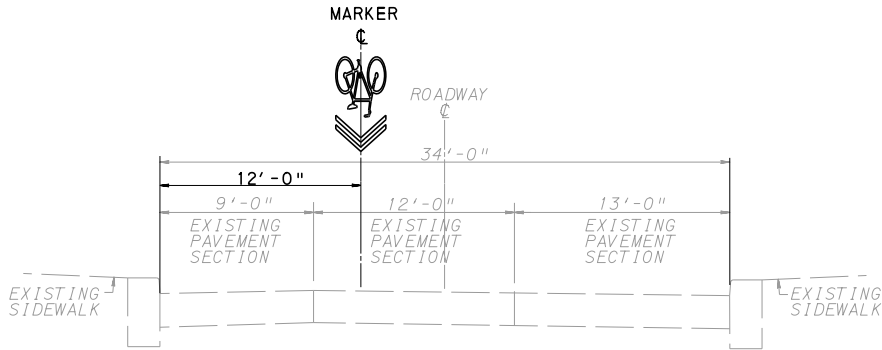
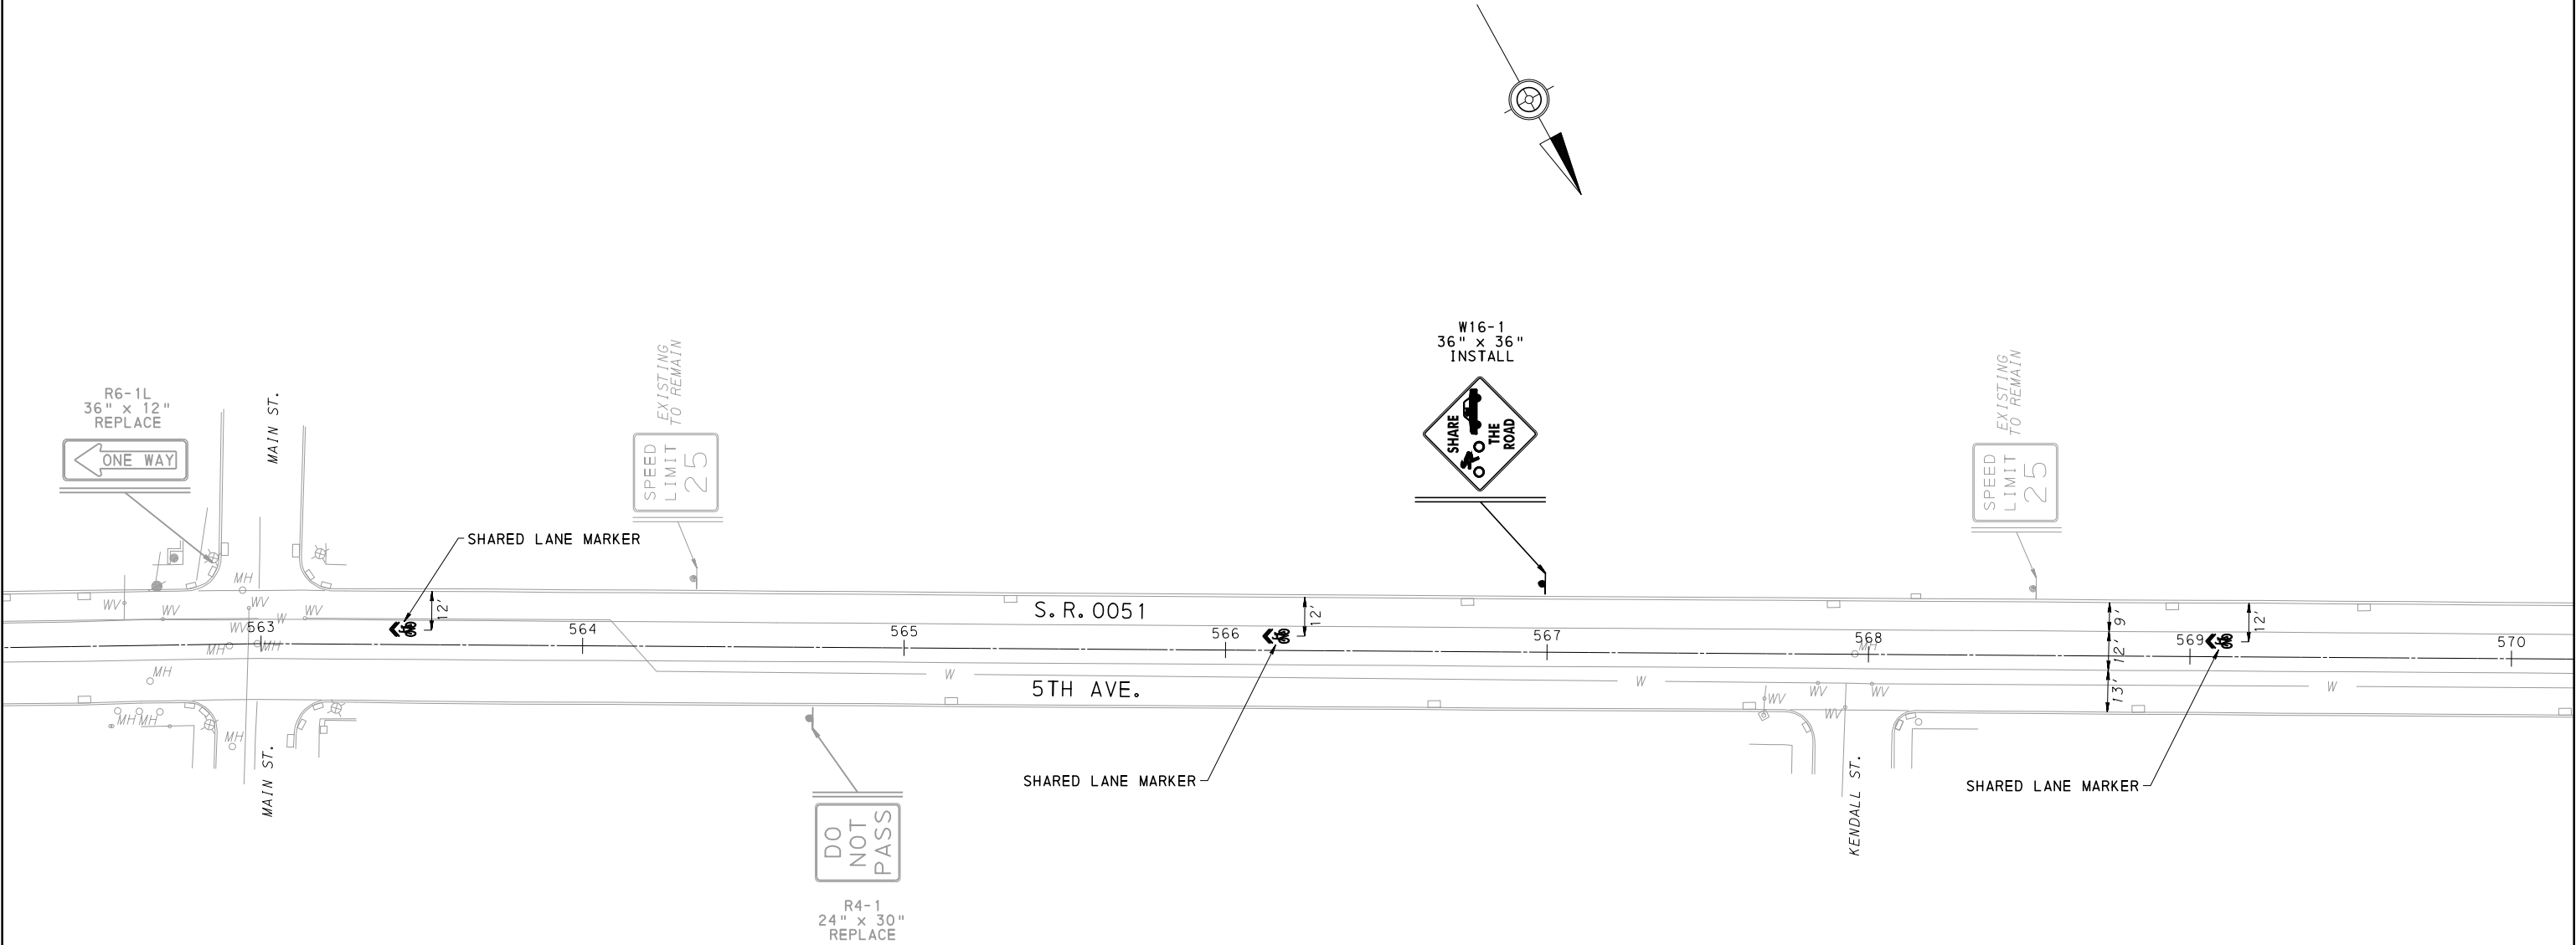


**SHARED LANE MARKER
LOCATION DETAIL**
SEE TC-8600 FOR MARKER DIMENSIONS
MARKER TO BE PLACED 12' INSIDE
RIGHT CURB SOUTHBOUND DIRECTION

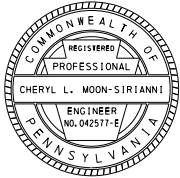


SIGNING AND PAVEMENT MARKING PLAN

DISTRICT	COUNTY	ROUTE	SECTION	SHEET
11-0	ALLEGHENY	0051	A93	13 OF 17
MOON TOWNSHIP, CORAOPOLIS BOROUGH				
REV NO	REVISIONS	DATE	BY	APPD

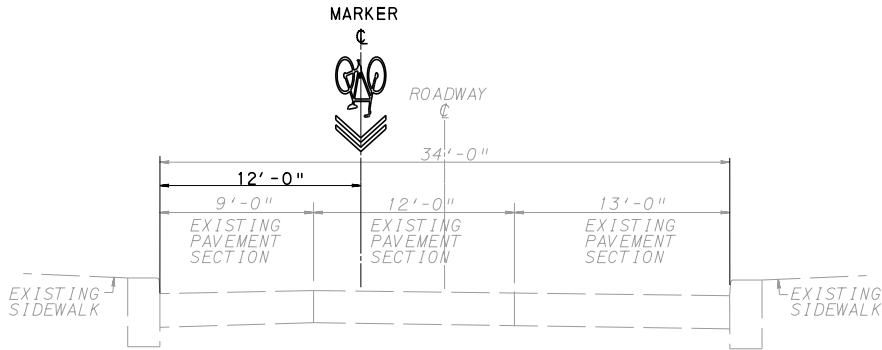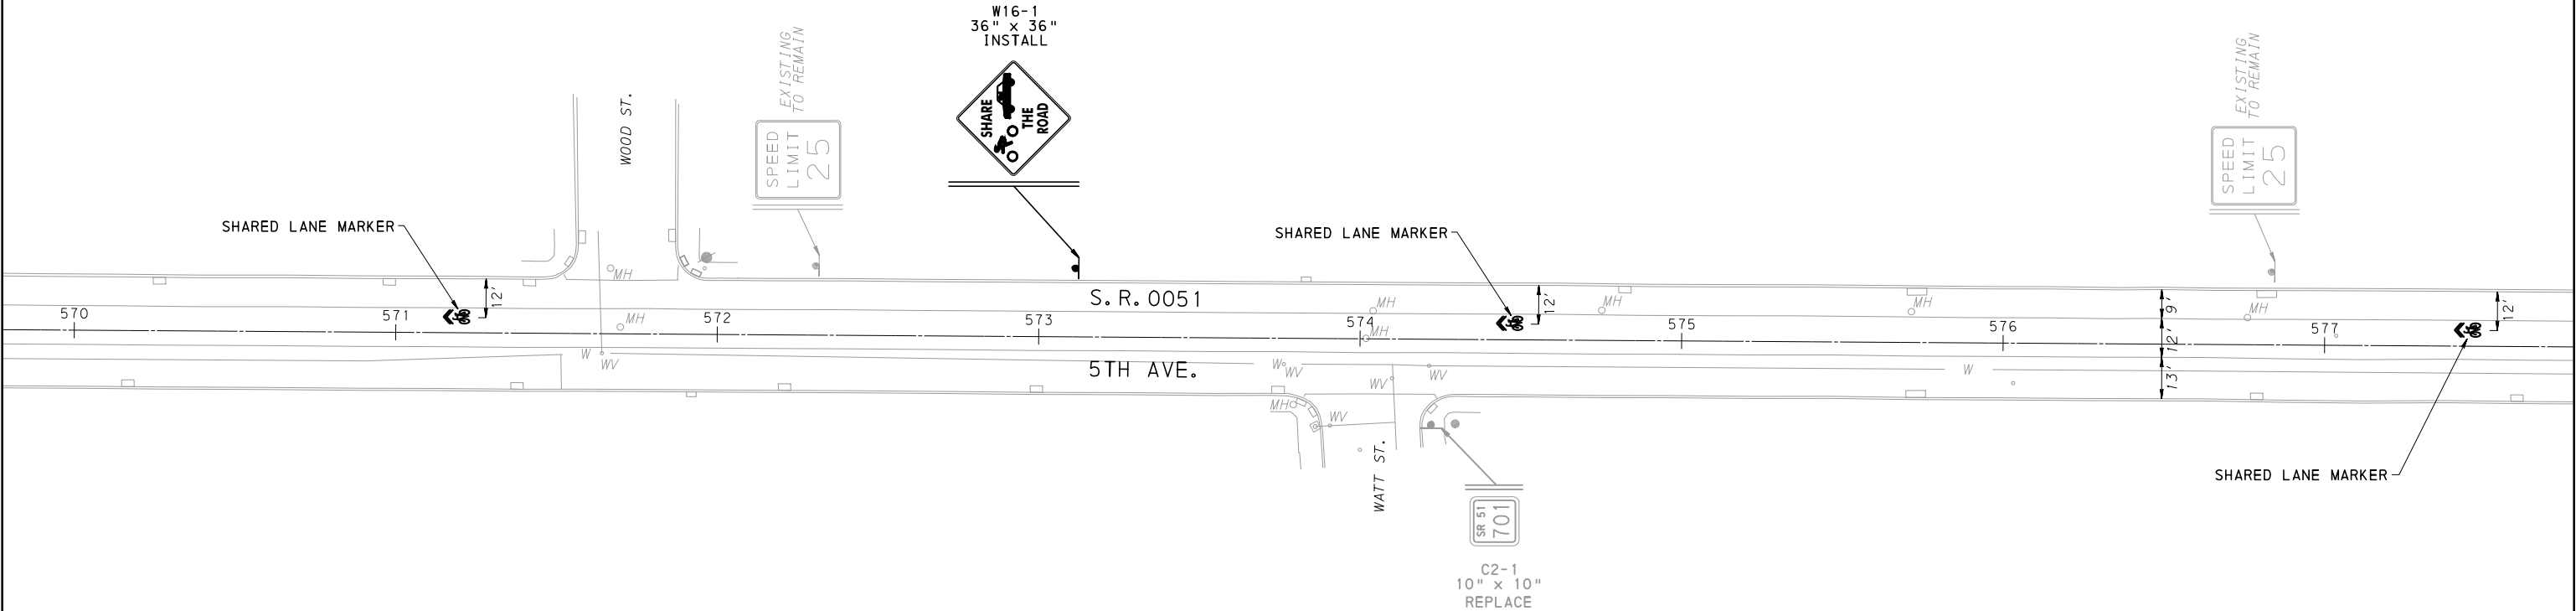

SHARED LANE MARKER
LOCATION DETAIL
SEE TC-8600 FOR MARKER DIMENSIONS
MARKER TO BE PLACED 12' INSIDE
RIGHT CURB SOUTHBOUND DIRECTION

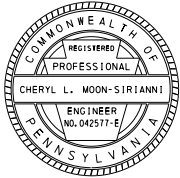

OPERATOR: G:\ds3\0051 A93 Fifth Ave. (Coraopolis)\Design\020051A93 (BICYCLE) Signing Pavement Marking.dgn
FILE NAME: G:\ds3\0051 A93 Fifth Ave. (Coraopolis)\Design\020051A93 (BICYCLE) Signing Pavement Marking.dgn

PLOTTED: 06-MAY-2016 12:59
D-9012 CADD (02-90) REVISED (10-04)



OPERATOR: G:\ds3\0051 A93 Fifth Ave. (Coraopolis)\Design\020051A93 (BICYCLE) Signing Pavement Marking.dgn

D-9012 CADD (02-90) REVISED (10-04)


PLOTTED:06-MAY-2016 12:59

SIGNING AND PAVEMENT MARKING PLAN

DISTRICT	COUNTY	ROUTE	SECTION	SHEET	
11-0	ALLEGHENY	0051	A93	14 OF 17	
MOON TOWNSHIP, CORAOPOLIS BOROUGH					
REV NO	REVISIONS			DATE	BY APPD

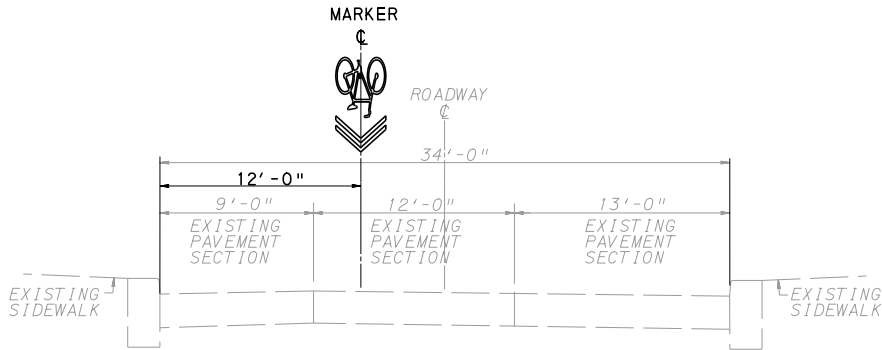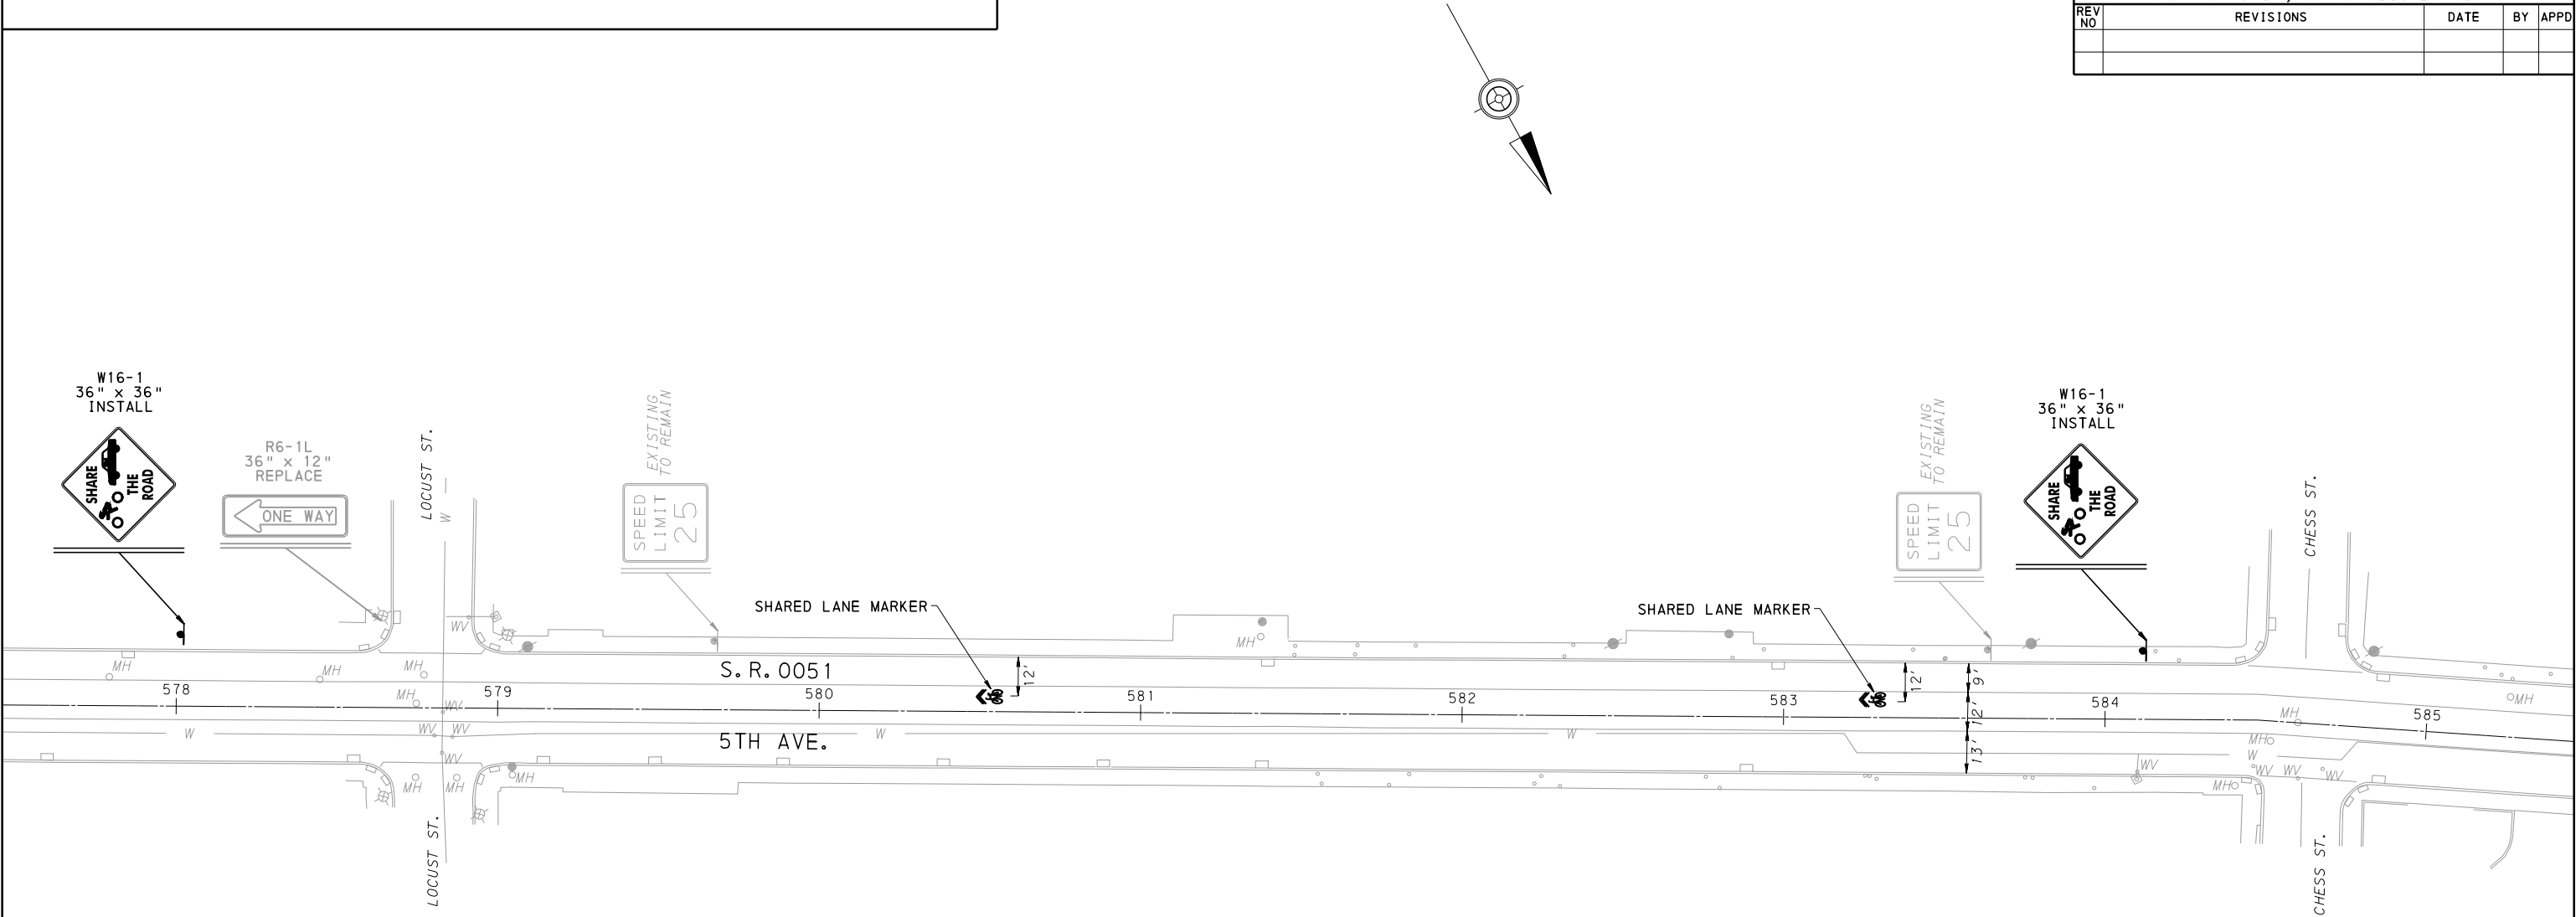

**SHARED LANE MARKER
LOCATION DETAIL**
SEE TC-8600 FOR MARKER DIMENSIONS
MARKER TO BE PLACED 12' INSIDE
RIGHT CURB SOUTHBOUND DIRECTION

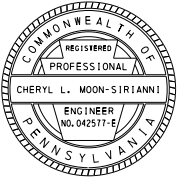


OPERATOR: G:\ds3\0051 A93 Fifth Ave. (Coraopolis)\DesIgn\020051A93 (BICYCLE) Signing Pavement Marking.dgn
FILE NAME: G:\ds3\0051 A93 Fifth Ave. (Coraopolis)\DesIgn\020051A93 (BICYCLE) Signing Pavement Marking.dgn

PLOTTED:06-MAY-2016 12:59

D-9012 CADD (02-90) REVISED (10-04)

SIGNING AND PAVEMENT MARKING PLAN

DISTRICT	COUNTY	ROUTE	SECTION	SHEET	
11-0	ALLEGHENY	0051	A93	15 OF 17	
MOON TOWNSHIP, CORAOPOLIS BOROUGH					
REV NO	REVISIONS			DATE	BY APPD

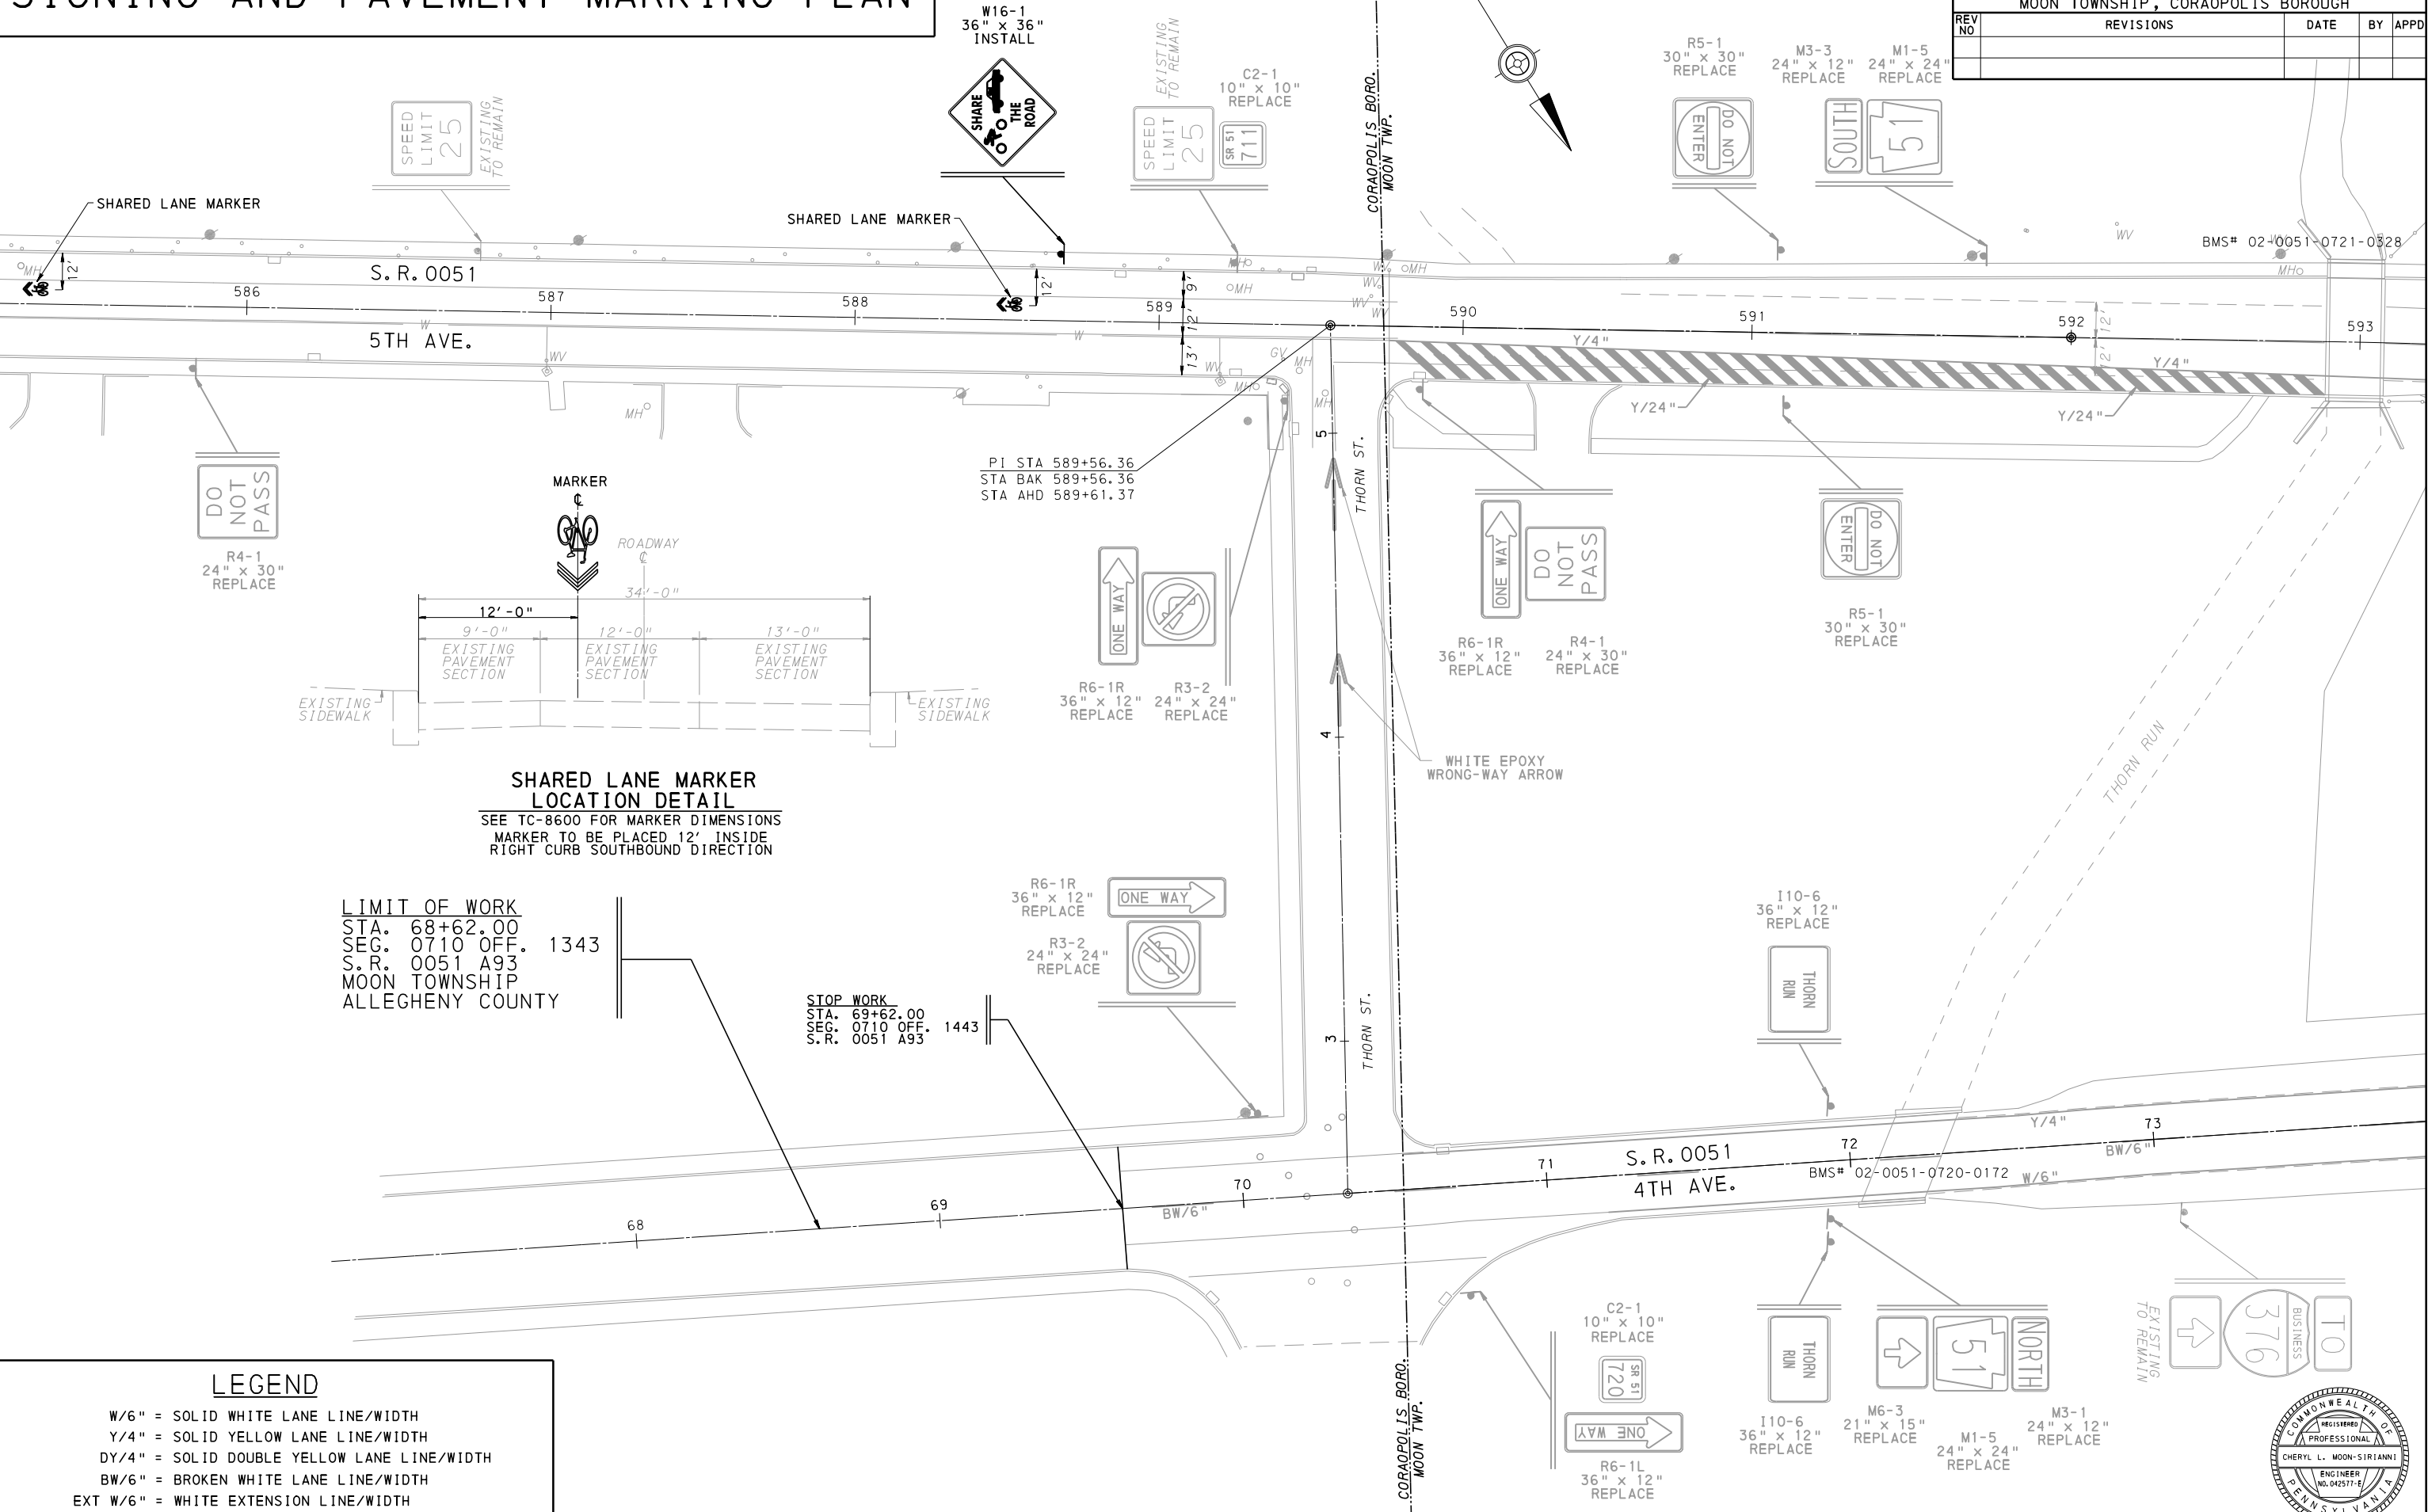


**SHARED LANE MARKER
LOCATION DETAIL**
SEE TC-8600 FOR MARKER DIMENSIONS
MARKER TO BE PLACED 12' INSIDE
RIGHT CURB SOUTHBOUND DIRECTION

LIMIT OF WORK
STA. 68+62.00
SEG. 0710 OFF. 1343
S.R. 0051 A93
MOON TOWNSHIP
ALLEGHENY COUNTY

STOP WORK
STA. 69+62.00
SEG. 0710 OFF. 1443
S.R. 0051 A93


LEGEND

W/6" = SOLID WHITE LANE LINE/WIDTH
Y/4" = SOLID YELLOW LANE LINE/WIDTH
DY/4" = SOLID DOUBLE YELLOW LANE LINE/WIDTH
BW/6" = BROKEN WHITE LANE LINE/WIDTH
EXT W/6" = WHITE EXTENSION LINE/WIDTH

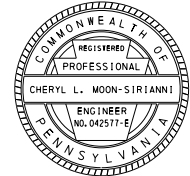


SIGNING AND PAVEMENT MARKING PLAN

DISTRICT	COUNTY	ROUTE	SECTION	SHEET	
11-0	ALLEGHENY	0051	A93	16 OF 17	
MOON TOWNSHIP, CORAOPOLIS BOROUGH					
REV NO	REVISIONS			DATE	BY APPD

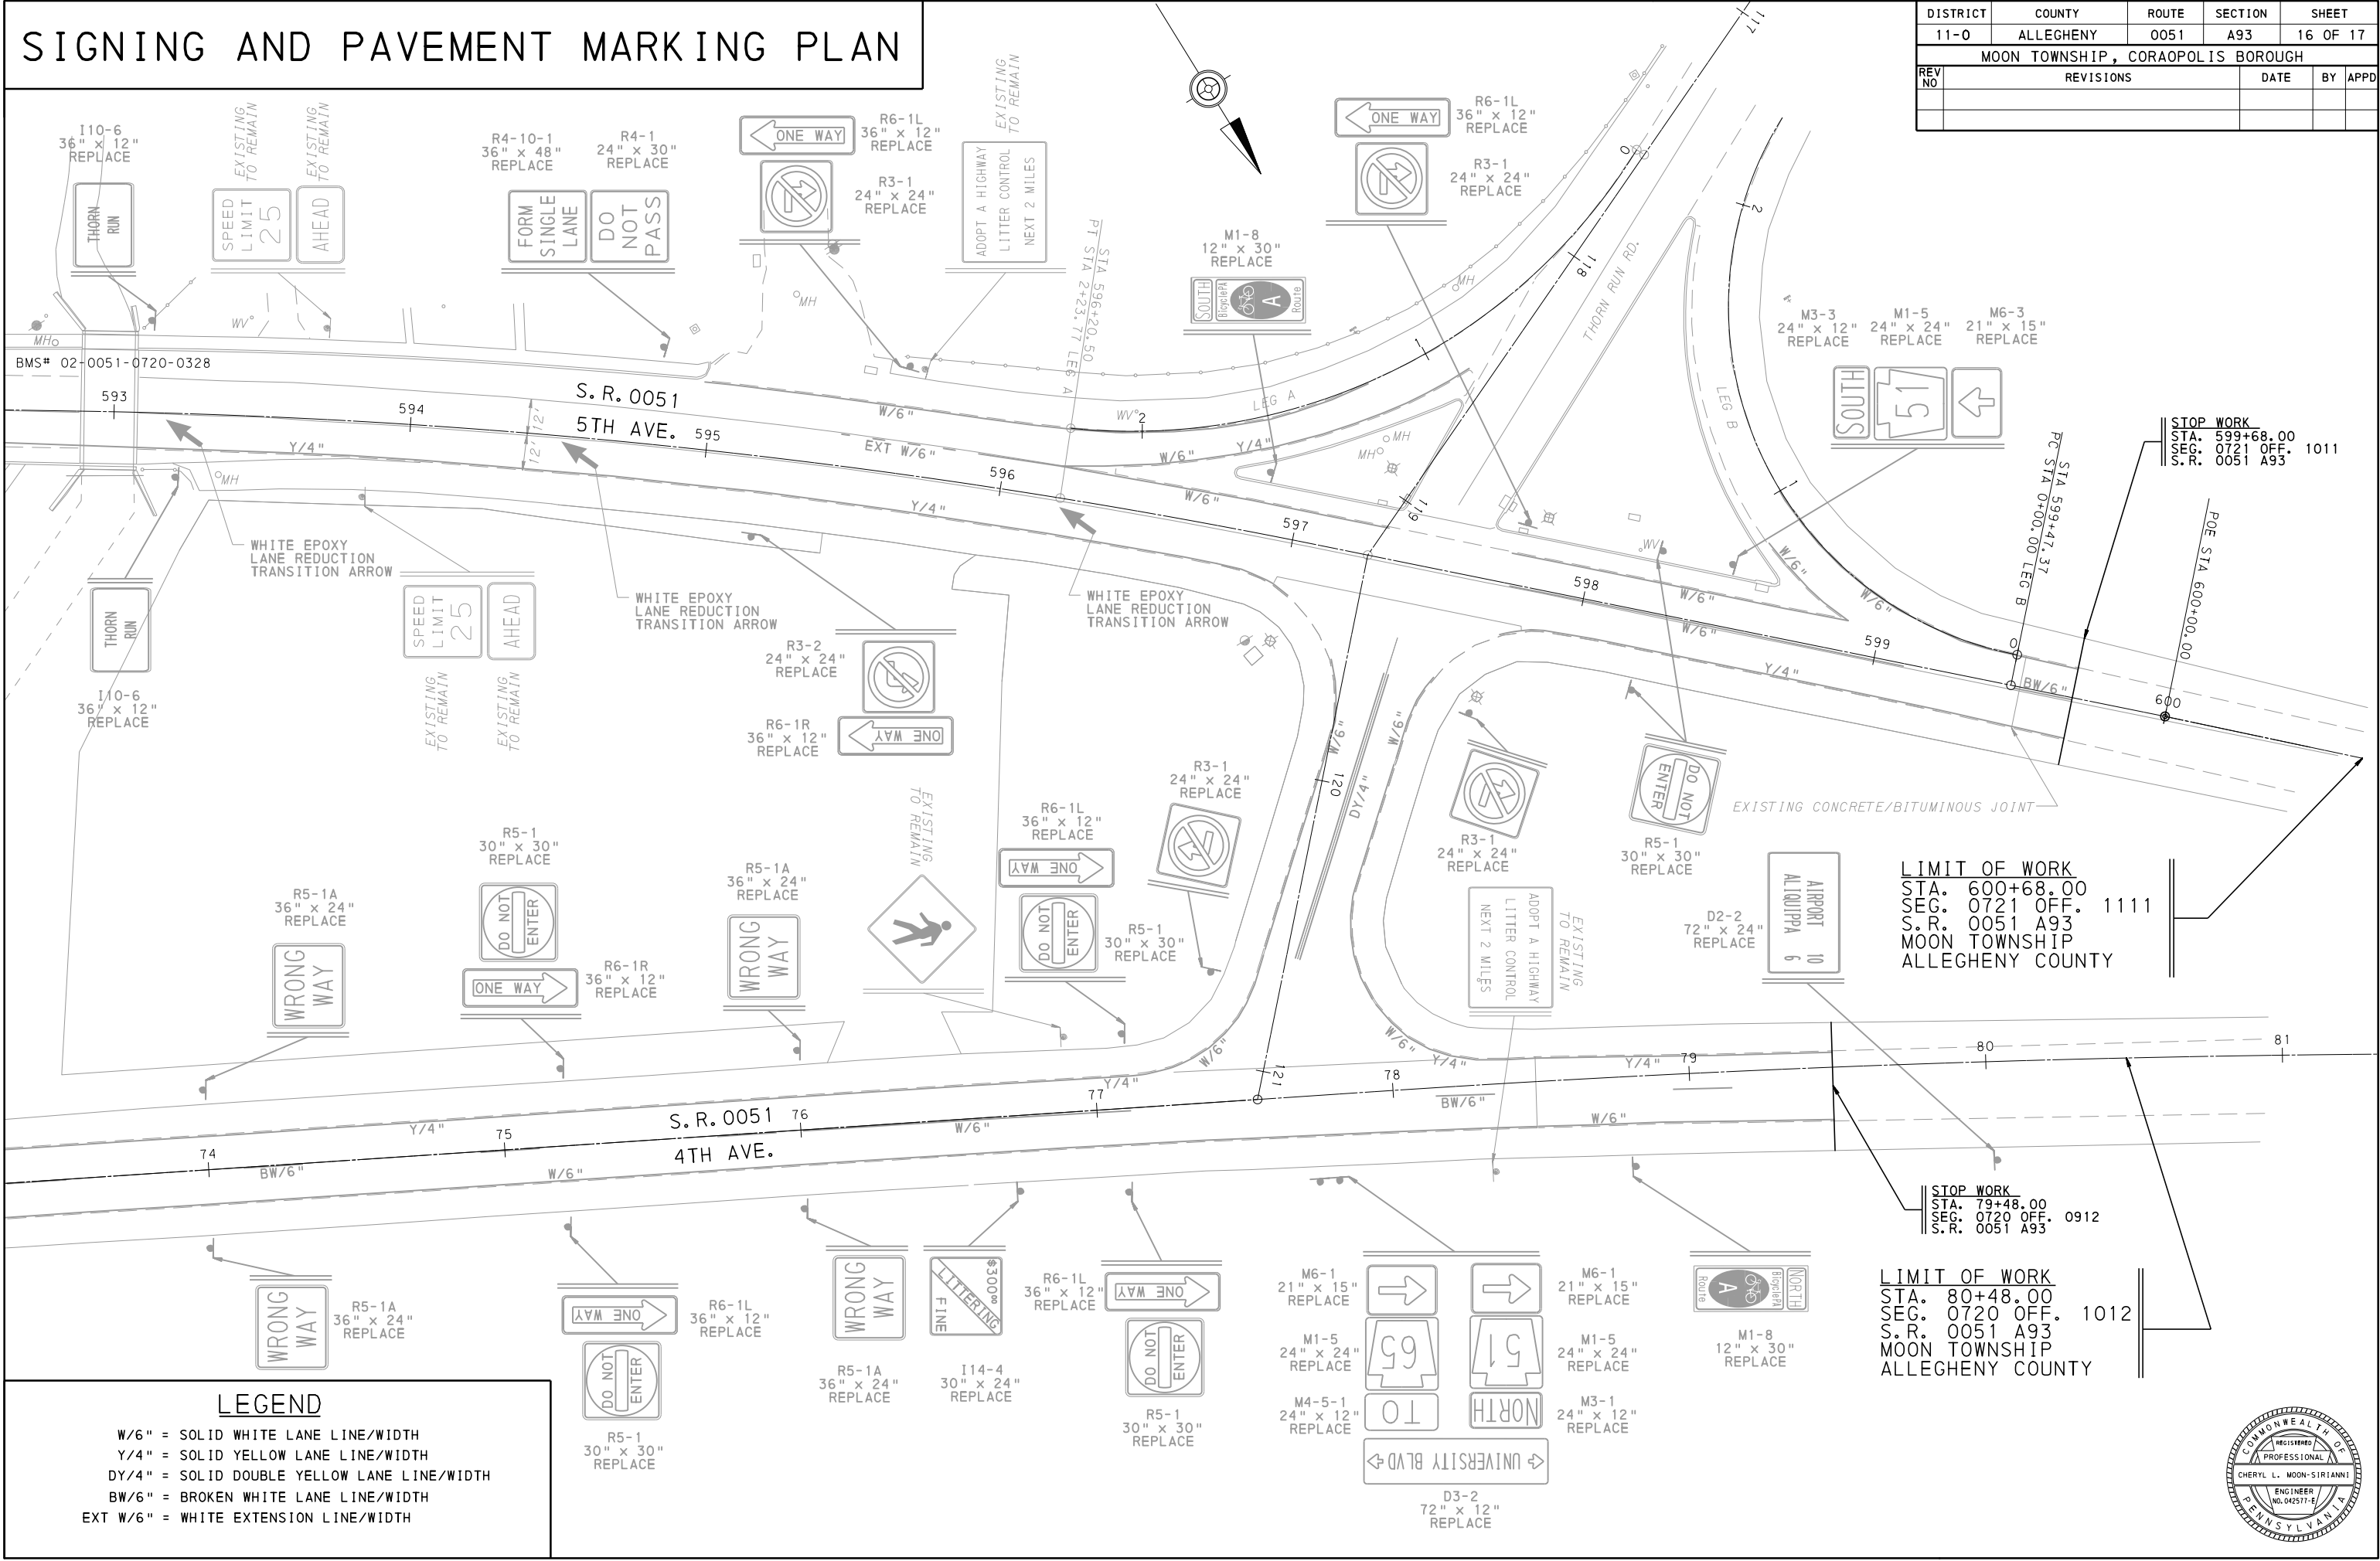


OPERATOR: G:\ds3\0051 A93 Fifth Ave. (Coraopolis)\Design\020051A93 (BICYCLE) Signing Pavement Marking.dgn
FILE NAME: G:\ds3\0051 A93 Fifth Ave. (Coraopolis)\Design\020051A93 (BICYCLE) Signing Pavement Marking.dgn
D-9012 CADD (02-90) REVISED (10-04)
PLOTED: 06-MAY-2016 12:59

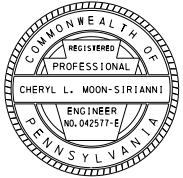


SIGNING AND PAVEMENT MARKING PLAN

DISTRICT	COUNTY	ROUTE	SECTION	SHEET	
11-0	ALLEGHENY	0051	A93	17 OF 17	
MOON TOWNSHIP, CORAOPOLIS BOROUGH					
REV NO	REVISIONS			DATE	BY APPD

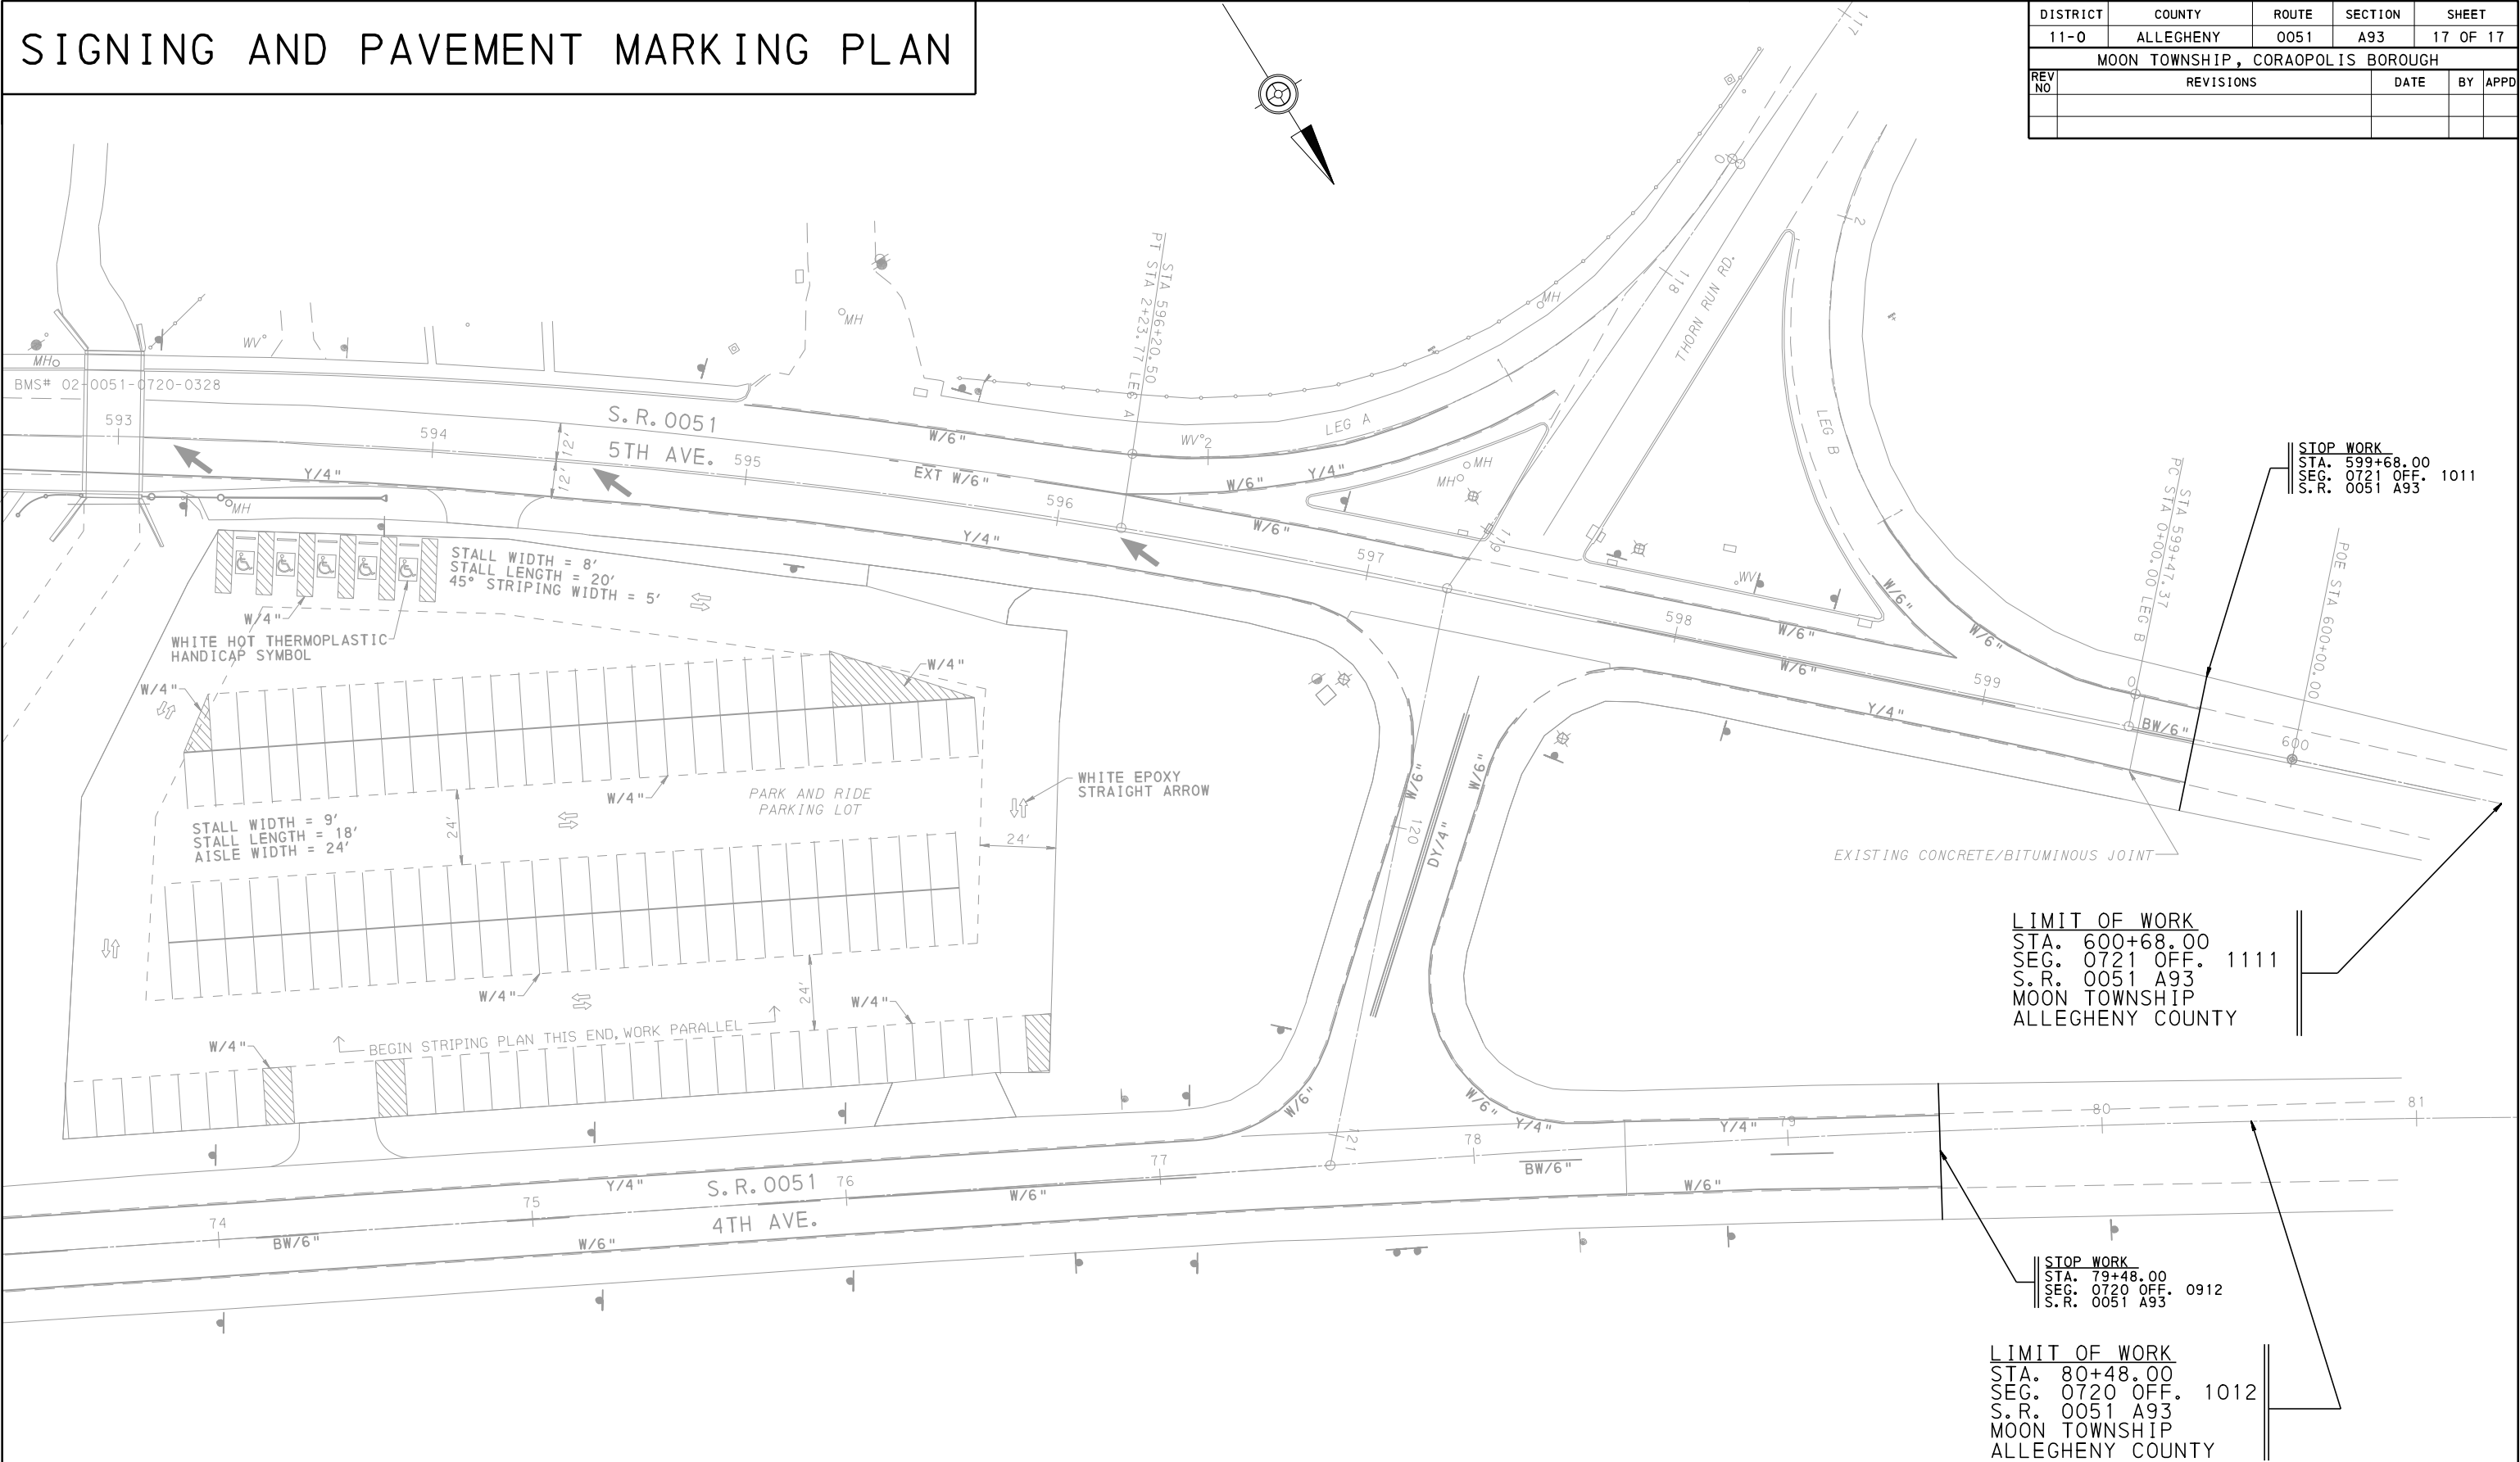

LEGEND

- W/4" = SOLID WHITE/WIDTH
- W/6" = SOLID WHITE LANE LINE/WIDTH
- Y/4" = SOLID YELLOW LANE LINE/WIDTH
- DY/4" = SOLID DOUBLE YELLOW LANE LINE/WIDTH
- BW/6" = BROKEN WHITE LANE LINE/WIDTH
- EXT W/6" = WHITE EXTENSION LINE/WIDTH

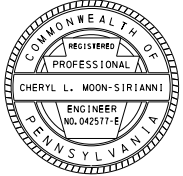

OPERATOR: G:\ds3\0051 A93 Fifth Ave. (Coraopolis)\Design\020051A93 (BICYCLE) Signing Pavement Marking.dgn
FILE NAME: G:\ds3\0051 A93 Fifth Ave. (Coraopolis)\Design\020051A93 (BICYCLE) Signing Pavement Marking.dgn
D-9012 CADD (02-90) REVISED (10-04) PLOTTED:06-MAY-2016 12:59