


DISTRICT	COUNTY	TOWNSHIP	BOROUGH	ROUTE	SECTION	TOTAL SHEETS				
11-0	ALLEGHENY	MOON	CORAOPOLIS	OHIO RIVER TRAIL PHASE I		14				
WBS ELEMENT										
T/P	SYS	SR OR WO	SP	PH	SECTION	ORG	PROG	P-C		
	0	0	R	T	P	1	0	3	1	5

MPMS# 95773

BOROUGH OF CORAOPOLIS
DRAWINGS AUTHORIZING ACQUISITION
OF
RIGHT-OF-WAY
FOR
OHIO RIVER TRAIL PHASE I

IN ALLEGHENY COUNTY
BY BOROUGH OF CORAOPOLIS
ON BEHALF OF
MOON TOWNSHIP

FROM STA. 200+00.00 TO STA. 227+67.55 LENGTH 2,767.55 FT. 0.524 MI.

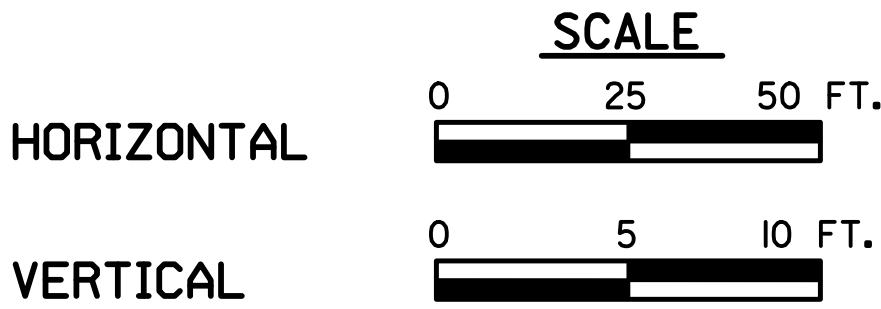

APPROVED
THIS PROJECT WAS AUTHORIZED FOR PROPERTY
AQISITION BY THE BOROUGH OF CORAOPOLIS

RESOLUTION NO. DATE

RECORDED IN THE OFFICE FOR THE
RECORDING OF DEEDS, ETC. IN
ALLEGHENY COUNTY, PA.

IN BOOK PAGE

WITNESS MY HAND AND SEAL OF OFFICE

DATE
RECORDER

COMMONWEALTH OF PENNSYLVANIA
COUNTY OF ALLEGHENY SS
BEFORE ME, A NOTARY PUBLIC, PERSONALLY CAME
KNOWN TO ME
OR SATISFATORILY PROVEN TO BE THE PERSON WHO
HAS BEEN AUTHORIZED BY WRITTEN DELEGATION TO
AFFIX THE FACSIMILE SIGNATURE OF LESLIE S. RICHARDS,
SECRETARY OF TRANSPORTATION, ON PLANS
AUTHORIZING ACQUISITION OF RIGHT-OF-WAY BY THE
DEPARTMENT OF TRANSPORTATION, AND AS SUCH
AUTHORIZED REPRESENTATIVE ACKNOWLEDGED THE
WITHIN PLAN, COMPRISING SHEETS, TO BE
AN OFFICIAL PLAN OF THE DEPARTMENT OF
TRANSPORTATION AND DESIRED THAT THE SAME BE
RECORDED AS SUCH.

WITNESS MY HAND AND NOTORIAL SEAL.

PREPARED BY:
MACKIN ENGINEERING COMPANY
RIDC PARK WEST
117 INDUSTRY DRIVE
PITTSBURGH, PA 15275

REG. PROF. SURVEYOR SU-051818-E

DATE

PREPARED BY:
MACKIN ENGINEERING COMPANY
RIDC PARK WEST
117 INDUSTRY DRIVE
PITTSBURGH, PA 15275

REG. PROF. ENGINEER PE021777E

DATE

BOROUGH OF CORAOPOLIS

APPROVED DATE:

RAY MCCUTCHEON BOROUGH MANAGER

MOON TOWNSHIP

APPROVED DATE:

DAWN LANE TOWNSHIP MANAGER

TABULATION OF PROPERTY OWNERS

- 1

FAMILY VIDEO
- 2

LYNN J. GEISLER AND SUSAN GEISLER
- 5

DUQUESNE LIGHT COMPANY
- 6

CSX TRANSPORTATION INC
- 7


VALLEY AMBULANCE AUTHORITY
- 10

TOWNSHIP OF MOON


TABULATION OF AUTHORIZATION AND OVERALL LENGTH

STA 200+00.00 TO STA 227+67.55 = 2767.55 FT = 0.524 MI

DISTRICT	COUNTY	ROUTE	SECTION	SHEET
11-0	ALLEGHENY	OHIO RIVER TRAIL PHASE I		2 OF 14
MOON TOWNSHIP & BOROUGH OF CORAOPOLIS				
REVISION NUMBER	REVISIONS			DATE

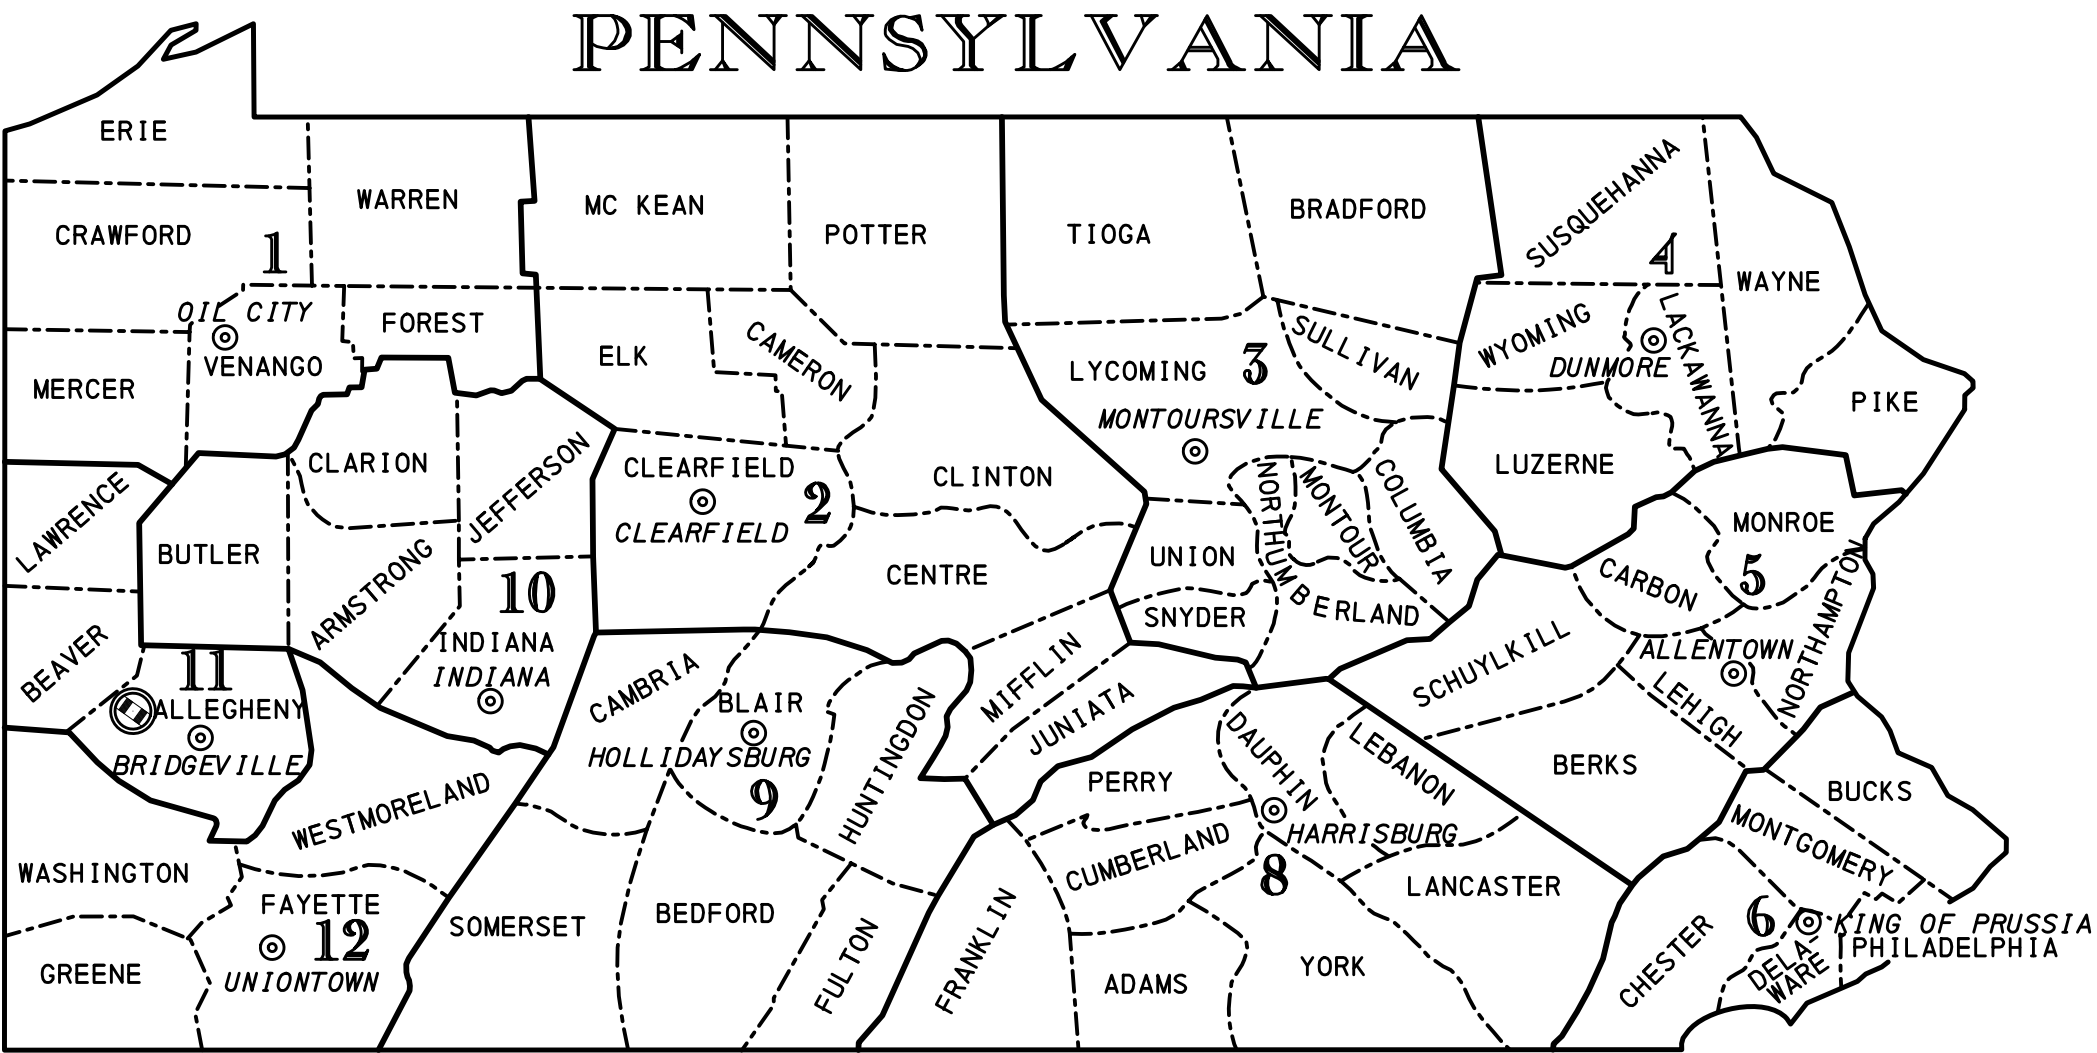


- 11 DISTRICT
- DISTRICT OFFICE
- PROJECT LOCATION

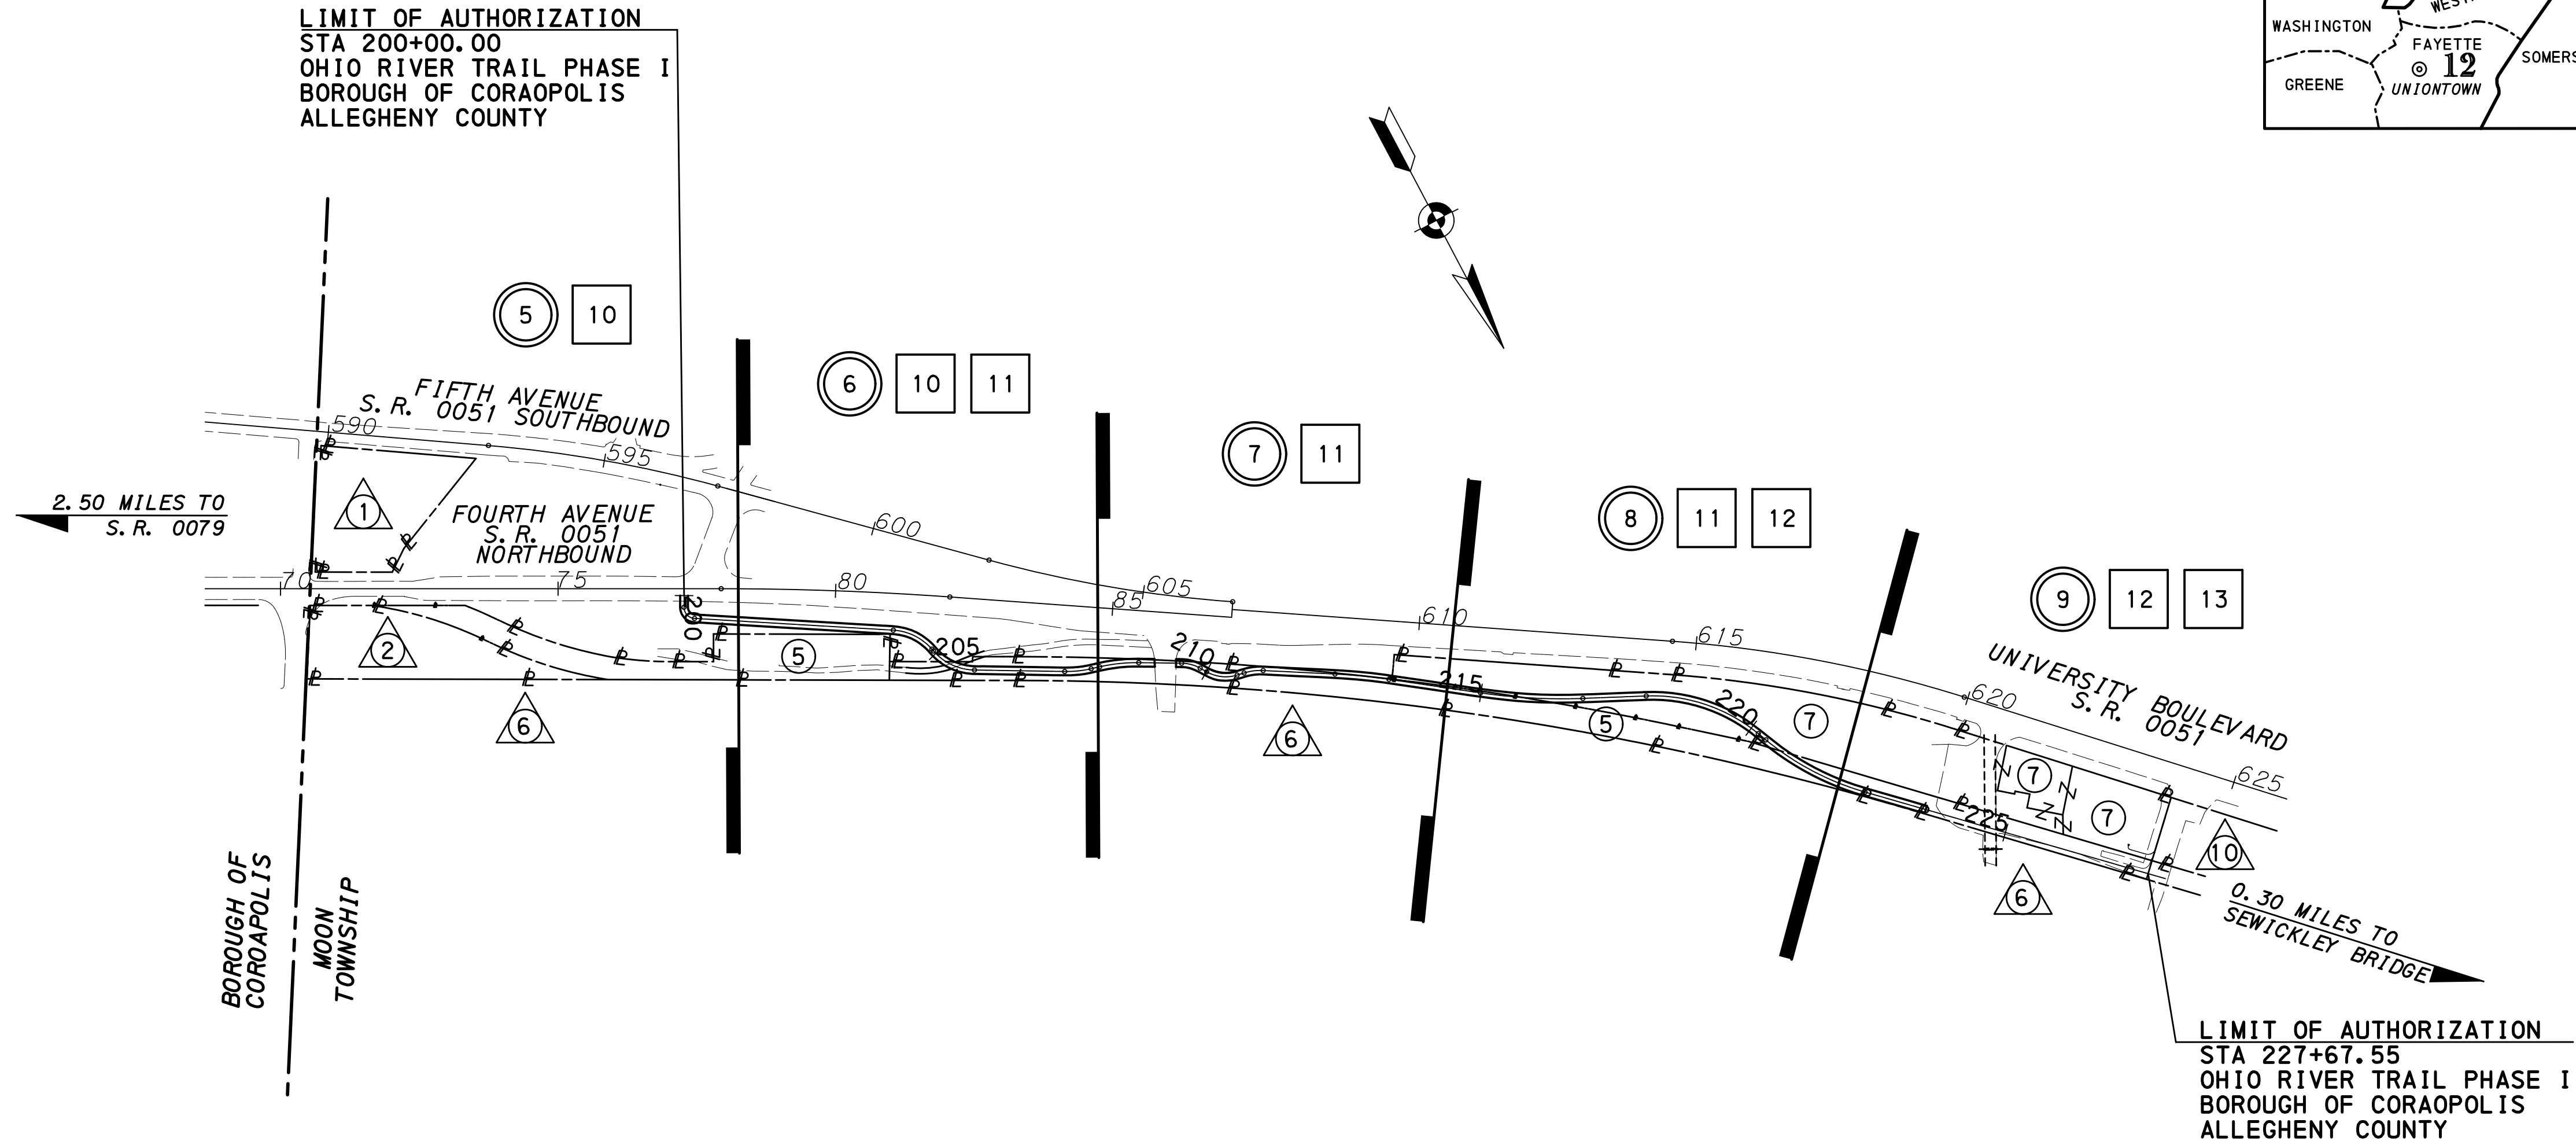

LEGEND


- PLAN
- PROFILE
- PARCEL IDENTIFICATION NUMBER
- PARCEL IDENTIFICATION NUMBER - NO TAKE

INDEX SHEET

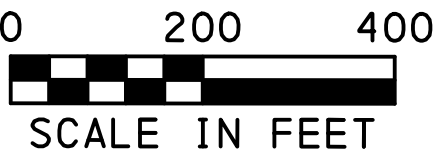

SHEET INDEX

DESCRIPTION	SHEET
TITLE SHEET	1
INDEX SHEET	2
LOCATION MAP-GENERAL NOTES	3
TYPICAL SECTIONS	4
PLAN SHEETS	5-9
PROFILE SHEETS	10-13
PROPERTY BLOCKS	14

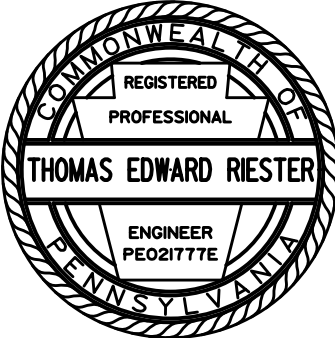

SUMMARY OF PROJECT COORDINATES

— D —	COMCAST CABLEVISION 183 SPRING RUN RD EXT BLDG 1A CORAOPLIS, PA. 15108 CONTACT: RAYMOND JONES EMAIL: raymond.jones@cable.comcast.com
— S —	MOON TOWNSHIP MUNICIPAL AUTHORITY 1700 BEAVER GRADE RD MOON TOWNSHIP, PA. 15108 CONTACT: JOANNE SCHULENBURG
— G —	COLUMBIA GAS OF PA INC - BETHEL PARK ADDRESS: 251 W MAIDEN ST WASHINGTON, PA. 15301 CONTACT: SHANNON GRIEST EMAIL: sgriest@nsource.com
— G1 —	BUCKEYE PARTNERS FIVE TEK PARK 9999 HAMILTON BLVD BREINIGSVILLE, PA. 18031 CONTACT: DAVE JONES EMAIL: DAJONES@BUCKEYE.COM

	RTE.	STATION	POINT	COORDINATES		BEARING
				NORTH	EAST	
SURVEY OF TRAIL BASELINE	OHIO RIVER TRAIL OFF-ROAD SEGMENT	200+00.00	BEGIN STA	442802.8620	1293896.7467	
		200+20.94	PC	442821.3024	1293906.6767	N 28° 18' 08" E
		200+39.94	PI	442838.0281	1293915.6835	N 28° 18' 08" E
		200+51.33	PT	442847.8831	1293899.4430	N 58° 45' 00" W
		204+10.07	PC	443033.9867	1293592.7525	N 58° 45' 00" W
		204+52.03	PI	443055.7554	1293556.8786	N 58° 45' 00" W
		204+89.53	PT	443096.6051	1293547.2807	N 13° 13' 20" W
		204+94.03	PC	443100.9894	1293546.2506	N 13° 13' 20" W
		205+38.54	PI	443144.3190	1293536.0700	N 13° 13' 20" W
		205+77.79	PT	443165.7552	1293497.0623	N 61° 12' 34" W
		207+40.37	PC	443244.0569	1293354.5759	N 61° 12' 34" W
		207+64.52	PI	443255.6883	1293333.4099	N 61° 12' 34" W
		207+88.44	PT	443261.9471	1293310.0836	N 74° 58' 50" W
		208+03.99	PC	443265.9765	1293295.0658	N 74° 58' 50" W
		208+39.67	PI	443275.2215	1293260.6097	N 74° 58' 50" W
		208+75.01	PT	443292.2892	1293229.2826	N 61° 25' 03" W
		209+52.22	PC	443329.2289	1293161.4809	N 61° 25' 03" W
		209+70.08	PI	443337.7732	1293145.7983	N 61° 25' 03" W
		209+87.19	PT	443352.7862	1293136.1259	N 32° 47' 33" W
		210+00.59	PC	443364.0506	1293128.8686	N 32° 47' 33" W
		210+30.67	PI	443389.3334	1293112.5797	N 79° 17' 40" W
		210+57.40	PT	443394.9204	1293083.0274	N 79° 17' 40" W
		210+70.50	PC	443397.3541	1293070.1546	N 79° 17' 40" W
		210+88.09	PI	443400.6212	1293052.8734	N 79° 17' 40" W
		211+05.32	PT	443409.5884	1293037.7439	N 59° 20' 41" W
		212+34.81	PC	443475.6125	1292926.3483	N 59° 20' 41" W
		212+83.76	PI	443500.5665	1292884.2462	N 59° 20' 41" W
		213+32.62	PT	443529.5124	1292844.7820	N 53° 44' 27" W
		214+99.34	PC	443628.1192	1292710.3439	N 53° 44' 27" W
		215+91.99	PI	443682.9143	1292635.6376	N 53° 44' 27" W
		216+84.11	PT	443723.0519	1292552.1359	N 64° 19' 38" W
		217+98.35	PC	443772.5449	1292449.1713	N 64° 19' 38" W
		219+12.21	PI	443821.8706	1292346.5549	N 64° 19' 38" W
		220+15.99	PT	443926.8593	1292302.5039	N 22° 45' 43" W
220+33.62	PC	443943.1166	1292295.6826	N 22° 45' 43" W		
221+36.64	PI	444038.1112	1292255.8249	N 22° 45' 43" W		
222+36.81	PT	444109.6137	1292181.6629	N 46° 02' 45" W		
227+65.81	END STA	444476.7818	1291800.8381	N 46° 02' 45" W		

GENERAL NOTES:

THE EXISTING LEGAL RIGHT OF WAY IS VARIABLE IN WIDTH
ON S.R. 0051 FORMERLY KNOWN AS L.R. 76, MOON TOWNSHIP,
ALLEGHENY COUNTY FROM STA. 595+16 SOUTHBOUND TO STA.
641+38 SOUTHBOUND IN ACCORDANCE WITH THE RIGHT OF WAY
PLAN FOR L.R. 76 SECTIONS 50&31, RECORDED NOVEMBER 21,
1967 IN THE ALLEGHENY RECORDERS' OFFICE IN STATE HIGHWAY
PLAN BOOK VOLUME 43, PAGES 1 TO 26.

ALL REQUIRED RIGHT-OF-WAY FOR THIS PROJECT SHALL BE
ACQUIRED IN FEE SIMPLE UNLESS OTHERWISE NOTED. AREAS,
IF ANY, NOT TO BE ACQUIRED IN FEE SIMPLE SHALL BE
ACQUIRED IN THE LESSER ESTATE OR INTEREST NOTED ON THE
PLAN SHEET.

THE FILING OF THIS PLAN IS NOT A CONDEMNATION OF THE PROPERTIES DESIGNATED THEREIN AND DOES NOT IN ANY MANNER WHATSOEVER RESTRICT THE USE OR DISPOSAL THEREOF. AUTHORIZATION TO CONDEMN UNDER THIS PLAN EXTENDS FOR ONLY ONE YEAR FROM THE DATE OF THE SECRETARY'S SIGNATURE INITIALLY AUTHORIZING ACQUISITION OR SUBSEQUENTLY REVISING THE PLAN OR REAUTHORIZING ACQUISITION THEREUNDER.

PRIVATE PROPERTY LINES ARE PLOTTED FROM THE DEED OF RECORD, RECORDED SUBDIVISION, OR LOT PLANS. PRIVATE PROPERTY LINES WERE NOT SURVEYED BY THE PROFESSIONAL LAND SURVEYOR RESPONSIBLE FOR THE PROJECT.

THE VERTICAL CONTROL FOR THIS PROJECT IS BASED ON THE
NORTH AMERICAN VERTICAL DATUM OF 1988 (NAVD 88).

THE HORIZONTAL CONTROL FOR THIS PROJECT IS TIED TO THE PENNSYLVANIA STATE COORDINATE SYSTEM SOUTH ZONE (NAD 1983).

ALL CURVE DATA IS BASED ON ARC DEFINITION.


TRAIL EASEMENT: AN EASEMENT FOR THE CONSTRUCTION, INSPECTION, MAINTENANCE, REPAIR, RECONSTRUCTION, AND ALTERATION OF TRAIL. THE EASEMENT SHALL NOT PREVENT THE PROPERTY OWNER FROM MAKING ANY LEGAL USE OF THE AREA WHICH IS NOT DETRIMENTAL TO THE TRAIL AND THE SAFETY OF THE TRAIL USERS. HOWEVER, NO STRUCTURE OF ANY KIND MAY BE ERRECTED IN THE TRAIL EASEMENT AREA WITHOUT ADVANCED WRITTEN APPROVAL BY THE OWNER OF TRAIL EASEMENT.

TEMPORARY CONSTRUCTION EASEMENT. AN EASEMENT TO USE THE LAND AND AS NECESSARY DURING CONSTRUCTION OF THE PROJECT. THE EASEMENT IS REQUIRED ONLY UNTIL THE CONSTRUCTION OR WORK INDICATED BY THE PLAN IS COMPLETED, UNLESS SOONER RELINQUISHED IN WRITING BY THE BOROUGH OF CORAOPOLIS.


SLOPE LIMITS SHOWN ON THIS PLAN ARE INDICATED AS FOLLOWS



THE HALF CIRCLED NUMBER INDICATES
A SCALED DIMENSION.

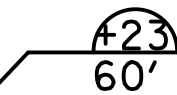

LIMIT OF AUTHORIZATION
STA 200+00.00
OHIO RIVER TRAIL PHASE I
BOROUGH OF CORAOPOLIS
ALLEGHENY COUNTY


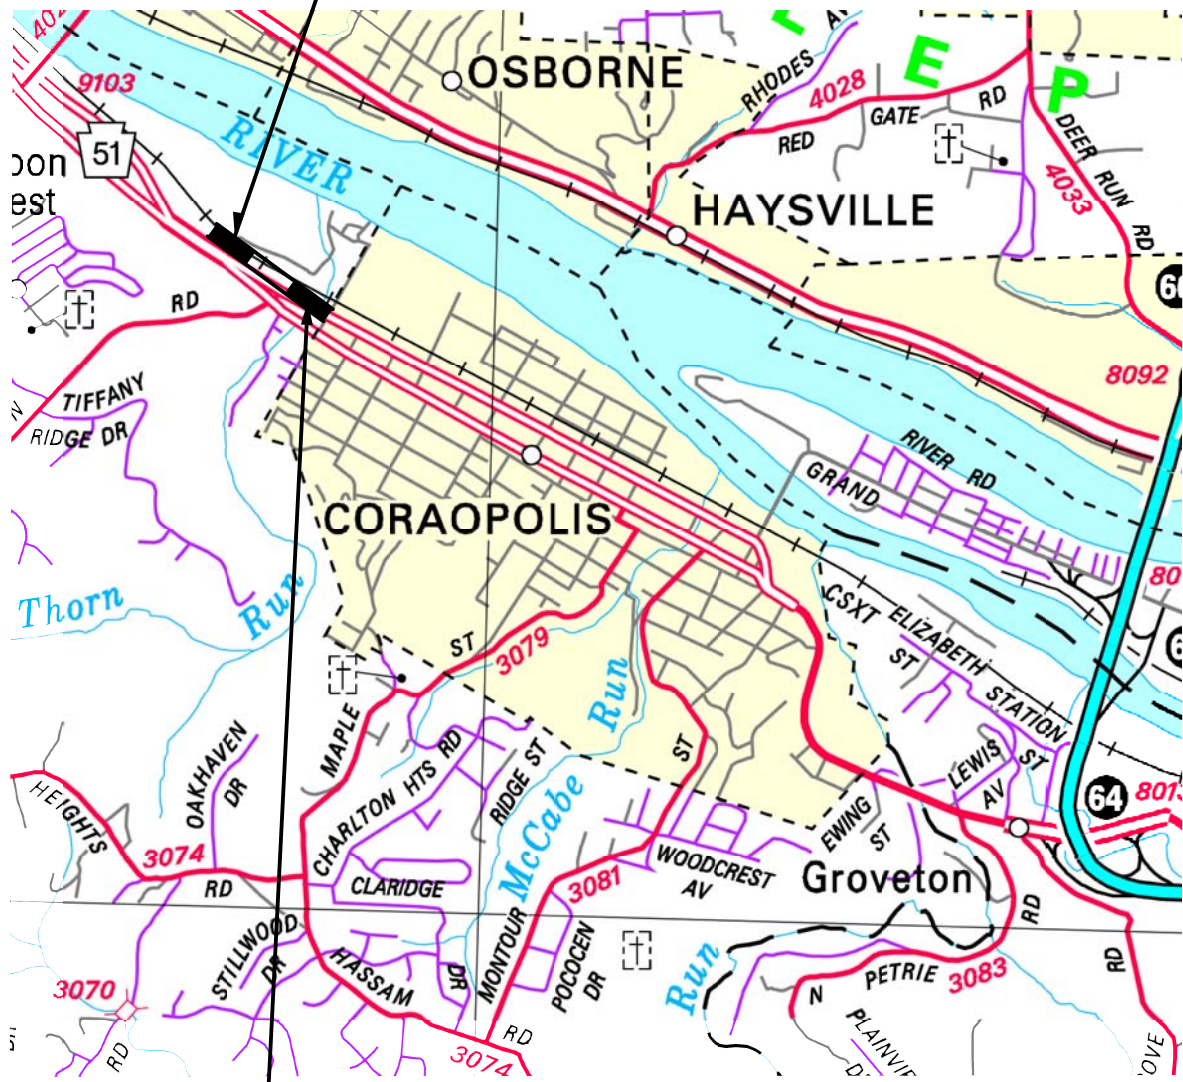


LOCATION MAP


LIMIT OF AUTHORIZATION
STA 277+67.55
OHIO RIVER TRAIL PAHSE I
BOROUGH OF CORAOPOLIS
ALLEGHENY COUNTY

LEGEND


-  EXPRESSWAY
 STATE ROUTE
 LOCAL ROADS
 TOWNSHIP LINE
 PROJECT

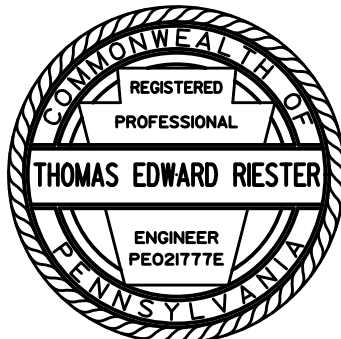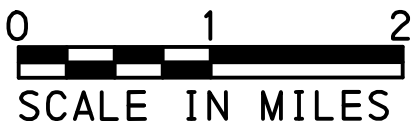


DISTRICT	COUNTY	ROUTE	SECTION	SHEET
11-0	ALLEGHENY	OHIO RIVER TRAIL PHASE 1		4 OF 14
MOON TOWNSHIP & BOROUGH OF CORAOPOLIS				
REVISION NUMBER	REVISIONS			DATE

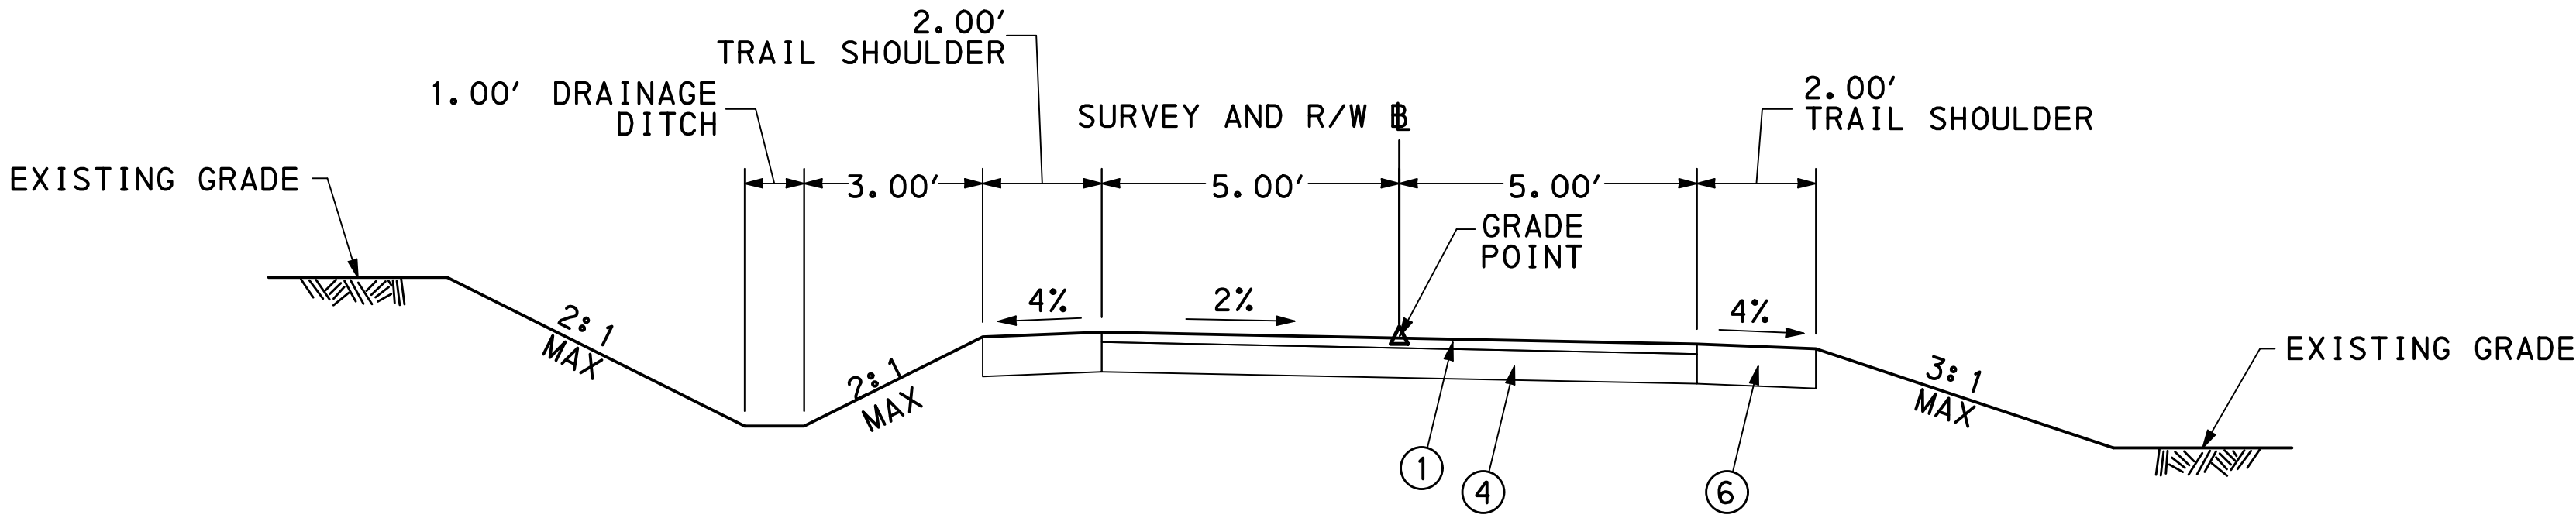


OHIO RIVER TRAIL PHASE 1 - TYPICAL SECTION
STA 200+20.00 TO STA 205+35.00
NOT TO SCALE

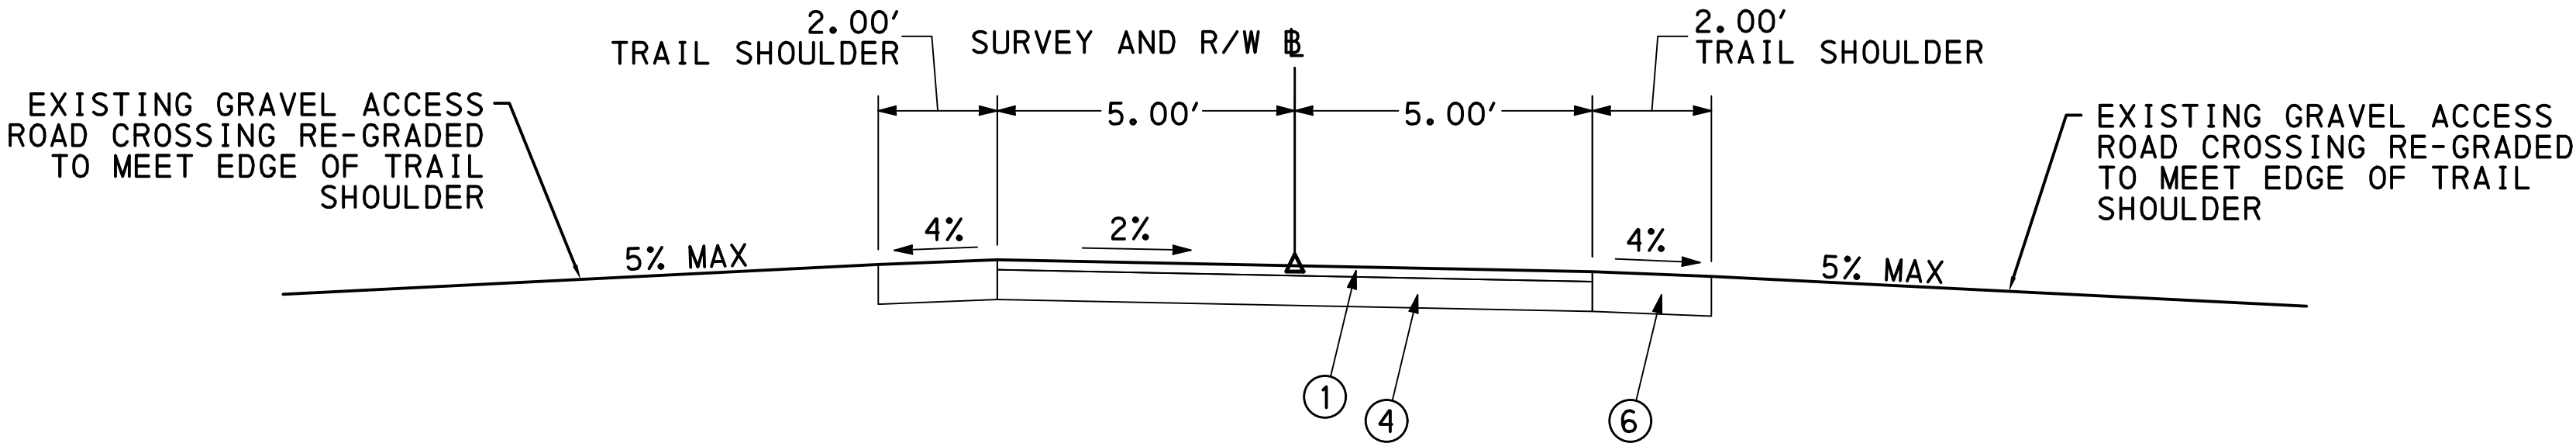

OHIO RIVER TRAIL PHASE 1 - TYPICAL SECTION
STA 205+35.00 TO STA 205+50.00
NOT TO SCALE

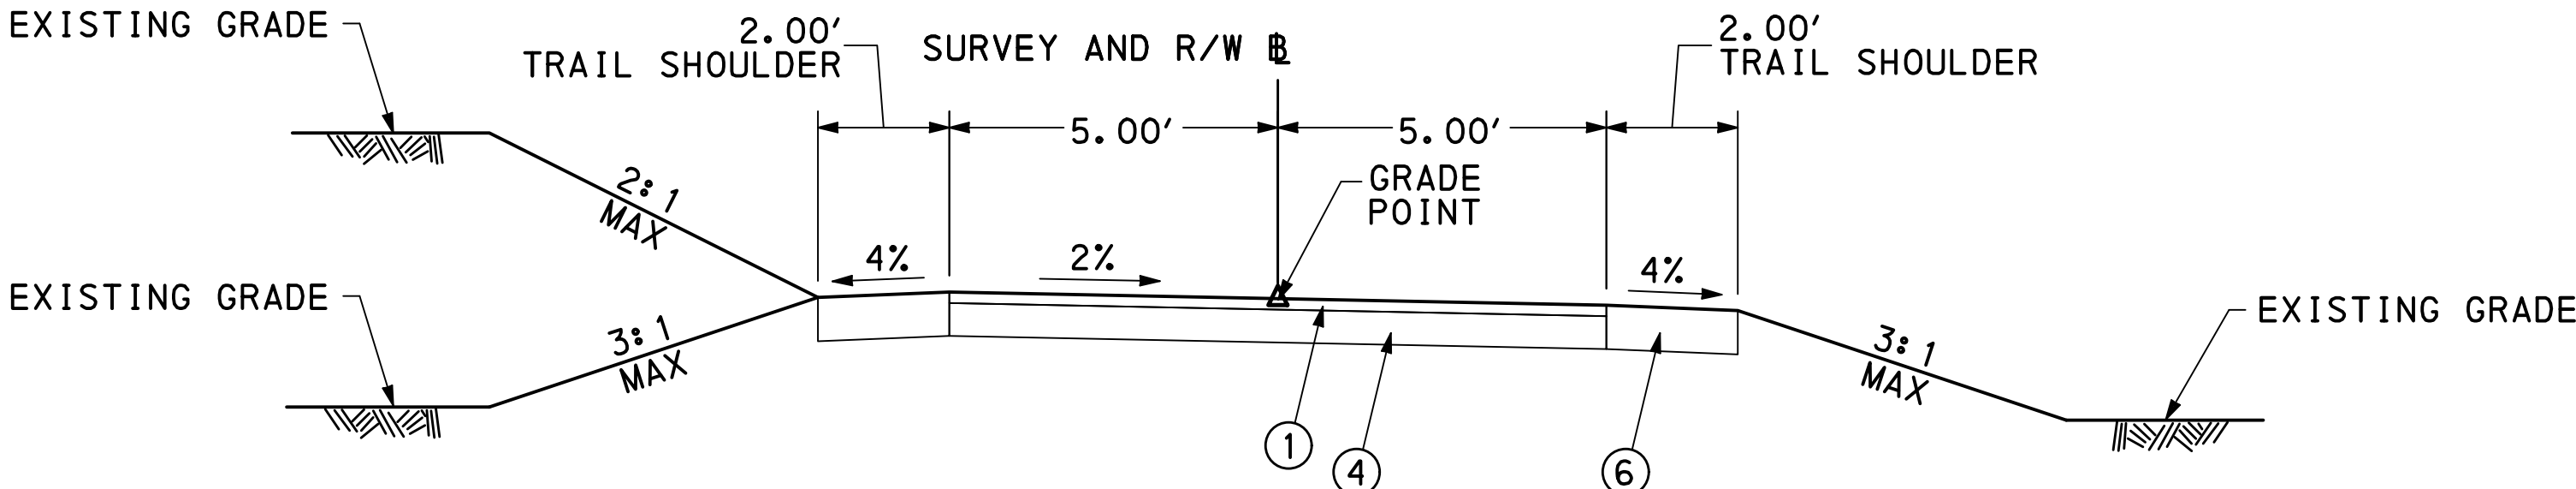


OHIO RIVER TRAIL PHASE 1 - TYPICAL SECTION
STA 205+50.00 TO STA 209+03.21
STA 209+42.30 TO 223+97.00
NOT TO SCALE

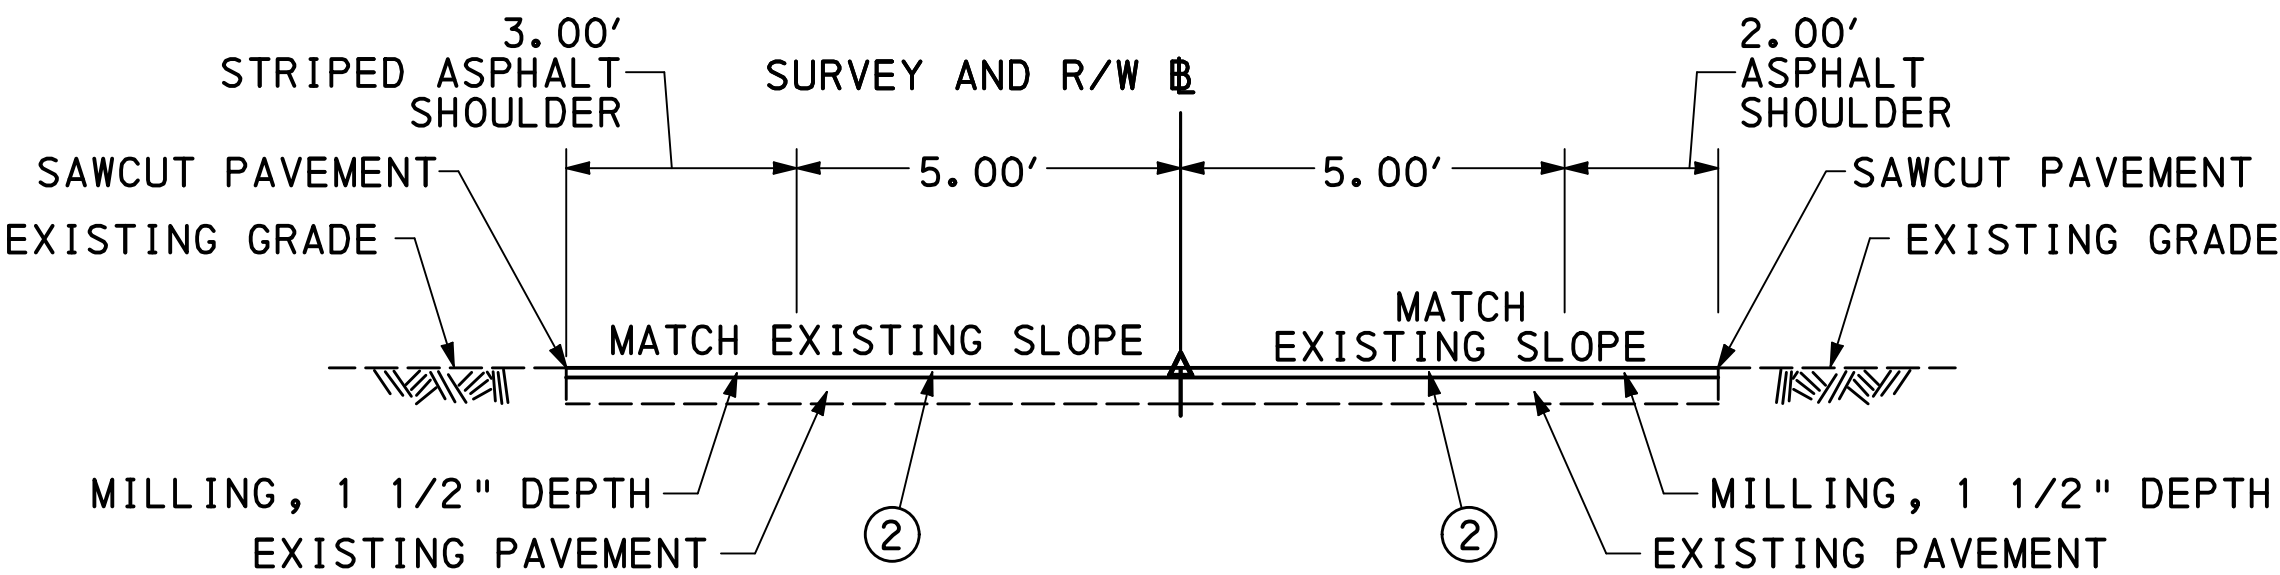


OHIO RIVER TRAIL PHASE 1 - TYPICAL SECTION
STA 223+97.00 TO STA 224+87.00
STA 226+91.00 TO 227+67.55
NOT TO SCALE

- ① AASHTO #10 CRUSHED LIMESTONE, 2" DEPTH
- ② SUPERPAVE ASPHALT MIXTURE DESIGN, HMA WEARING COURSE, PG 64-22, 9.5 MM MIX, 1 1/2" DEPTH
- ③ SUPERPAVE ASPHALT MIXTURE DESIGN, HMA BINDER COURSE, PG 64-22, 19 MM MIX, 2" DEPTH
- ④ SUBBASE, 6" DEPTCH (NO. 2A)
- ⑤ SUBBASE, 4" DEPTH (NO. 2A)
- ⑥ NO. 2A COURSE AGGREGATE, 8" DEPTH

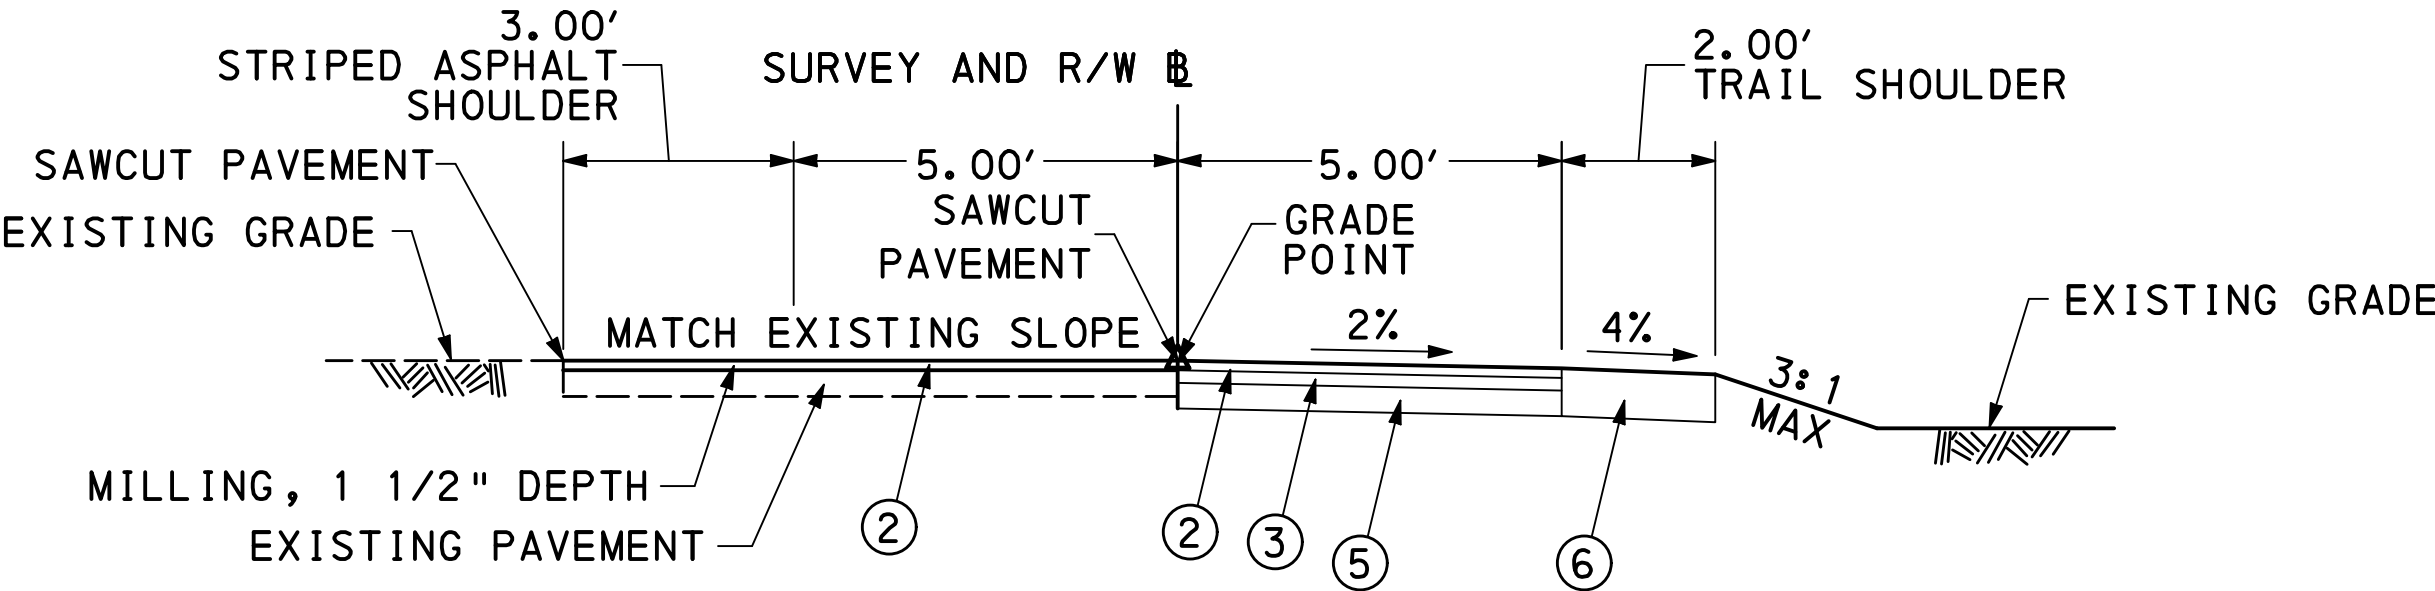


OHIO RIVER TRAIL PHASE 1 - TYPICAL SECTION
STA 224+87.00 TO STA 226+91.00
NOT TO SCALE

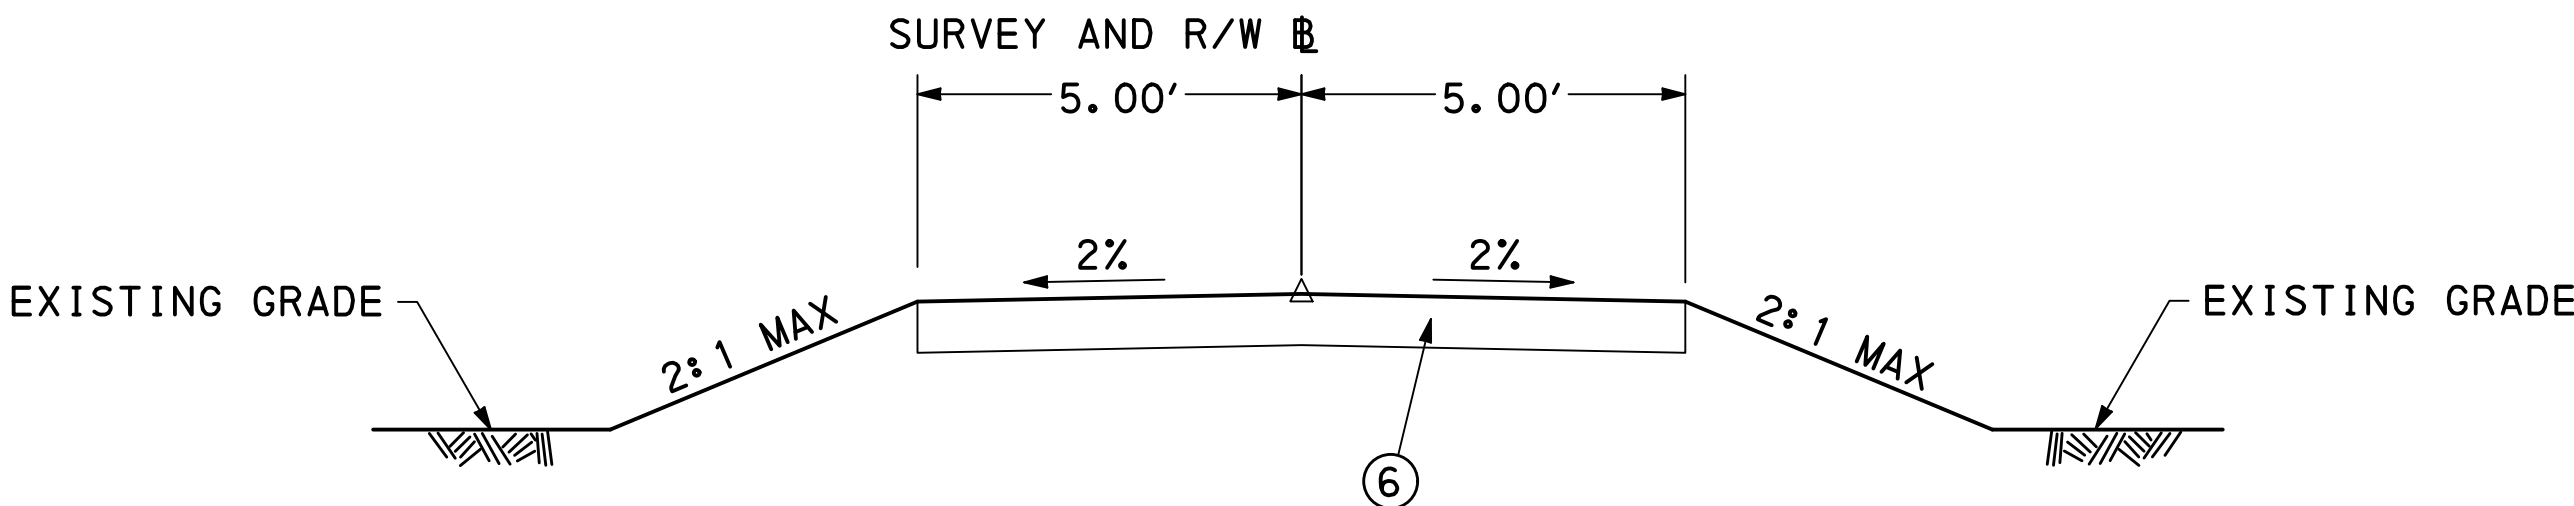

GRAVEL ACCESS ROAD - TYPICAL SECTION
STA 1000+00.00 TO STA 1001+47.09
NOT TO SCALE

TYPICAL SECTIONS

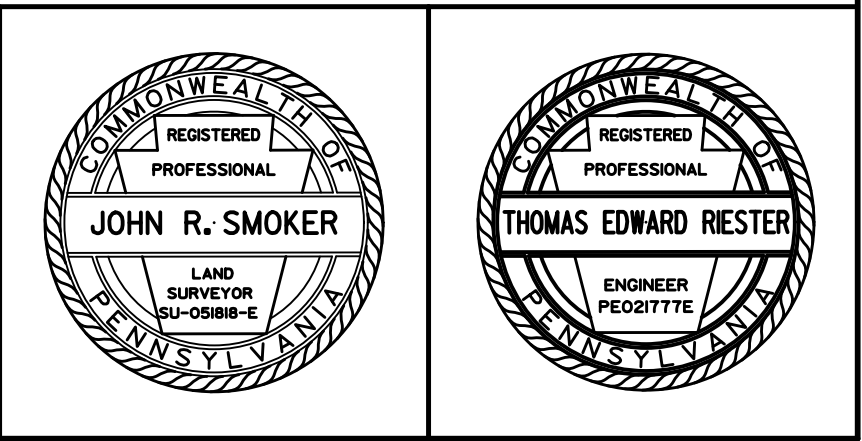


DISTRICT	COUNTY	ROUTE	SECTION	SHEET
11-0	ALLEGHENY	OHIO RIVER TRAIL PHASE 1		5 OF 14
MOON TOWNSHIP & BOROUGH OF CORAOPOLIS				
REVISION NUMBER	REVISIONS			DATE

TRAIL EASEMENT: AN EASEMENT FOR THE CONSTRUCTION, INSPECTION, MAINTENANCE, REPAIR, RECONSTRUCTION, AND ALTERATION OF TRAIL. THE EASEMENT SHALL NOT PREVENT THE PROPERTY OWNER FROM MAKING ANY LEGAL USE OF THE AREA WHICH IS NOT DETRIMENTAL TO THE TRAIL AND THE SAFETY OF THE TRAIL USERS. HOWEVER, NO STRUCTURE OF ANY KIND MAY BE ERECTED IN THE TRAIL EASEMENT AREA WITHOUT ADVANCED WRITTEN APPROVAL BY THE OWNER OF TRAIL EASEMENT.

TEMPORARY CONSTRUCTION EASEMENT. AN EASEMENT TO USE THE LAND AS NECESSARY DURING CONSTRUCTION OF THE PROJECT. THE EASEMENT IS REQUIRED ONLY UNTIL THE CONSTRUCTION OR WORK INDICATED BY THE PLAN IS COMPLETED, UNLESS SOONER RELINQUISHED IN WRITING BY THE BOROUGH OF CORAOPOLIS.

LIMIT OF AUTHORIZATION
STA 200+00.00
OHIO RIVER TRAIL PHASE I
BOROUGH OF CORAOPOLIS
ALLEGHENY COUNTY



TRAIL CURVE DATA
PT STA 200+39.94
Δ = 87° 08' 03" LT
T = 19.00'
L = 30.39'
R = 20.00'
E = 7.58'
PC STA 200+20.94
PT STA 200+51.33

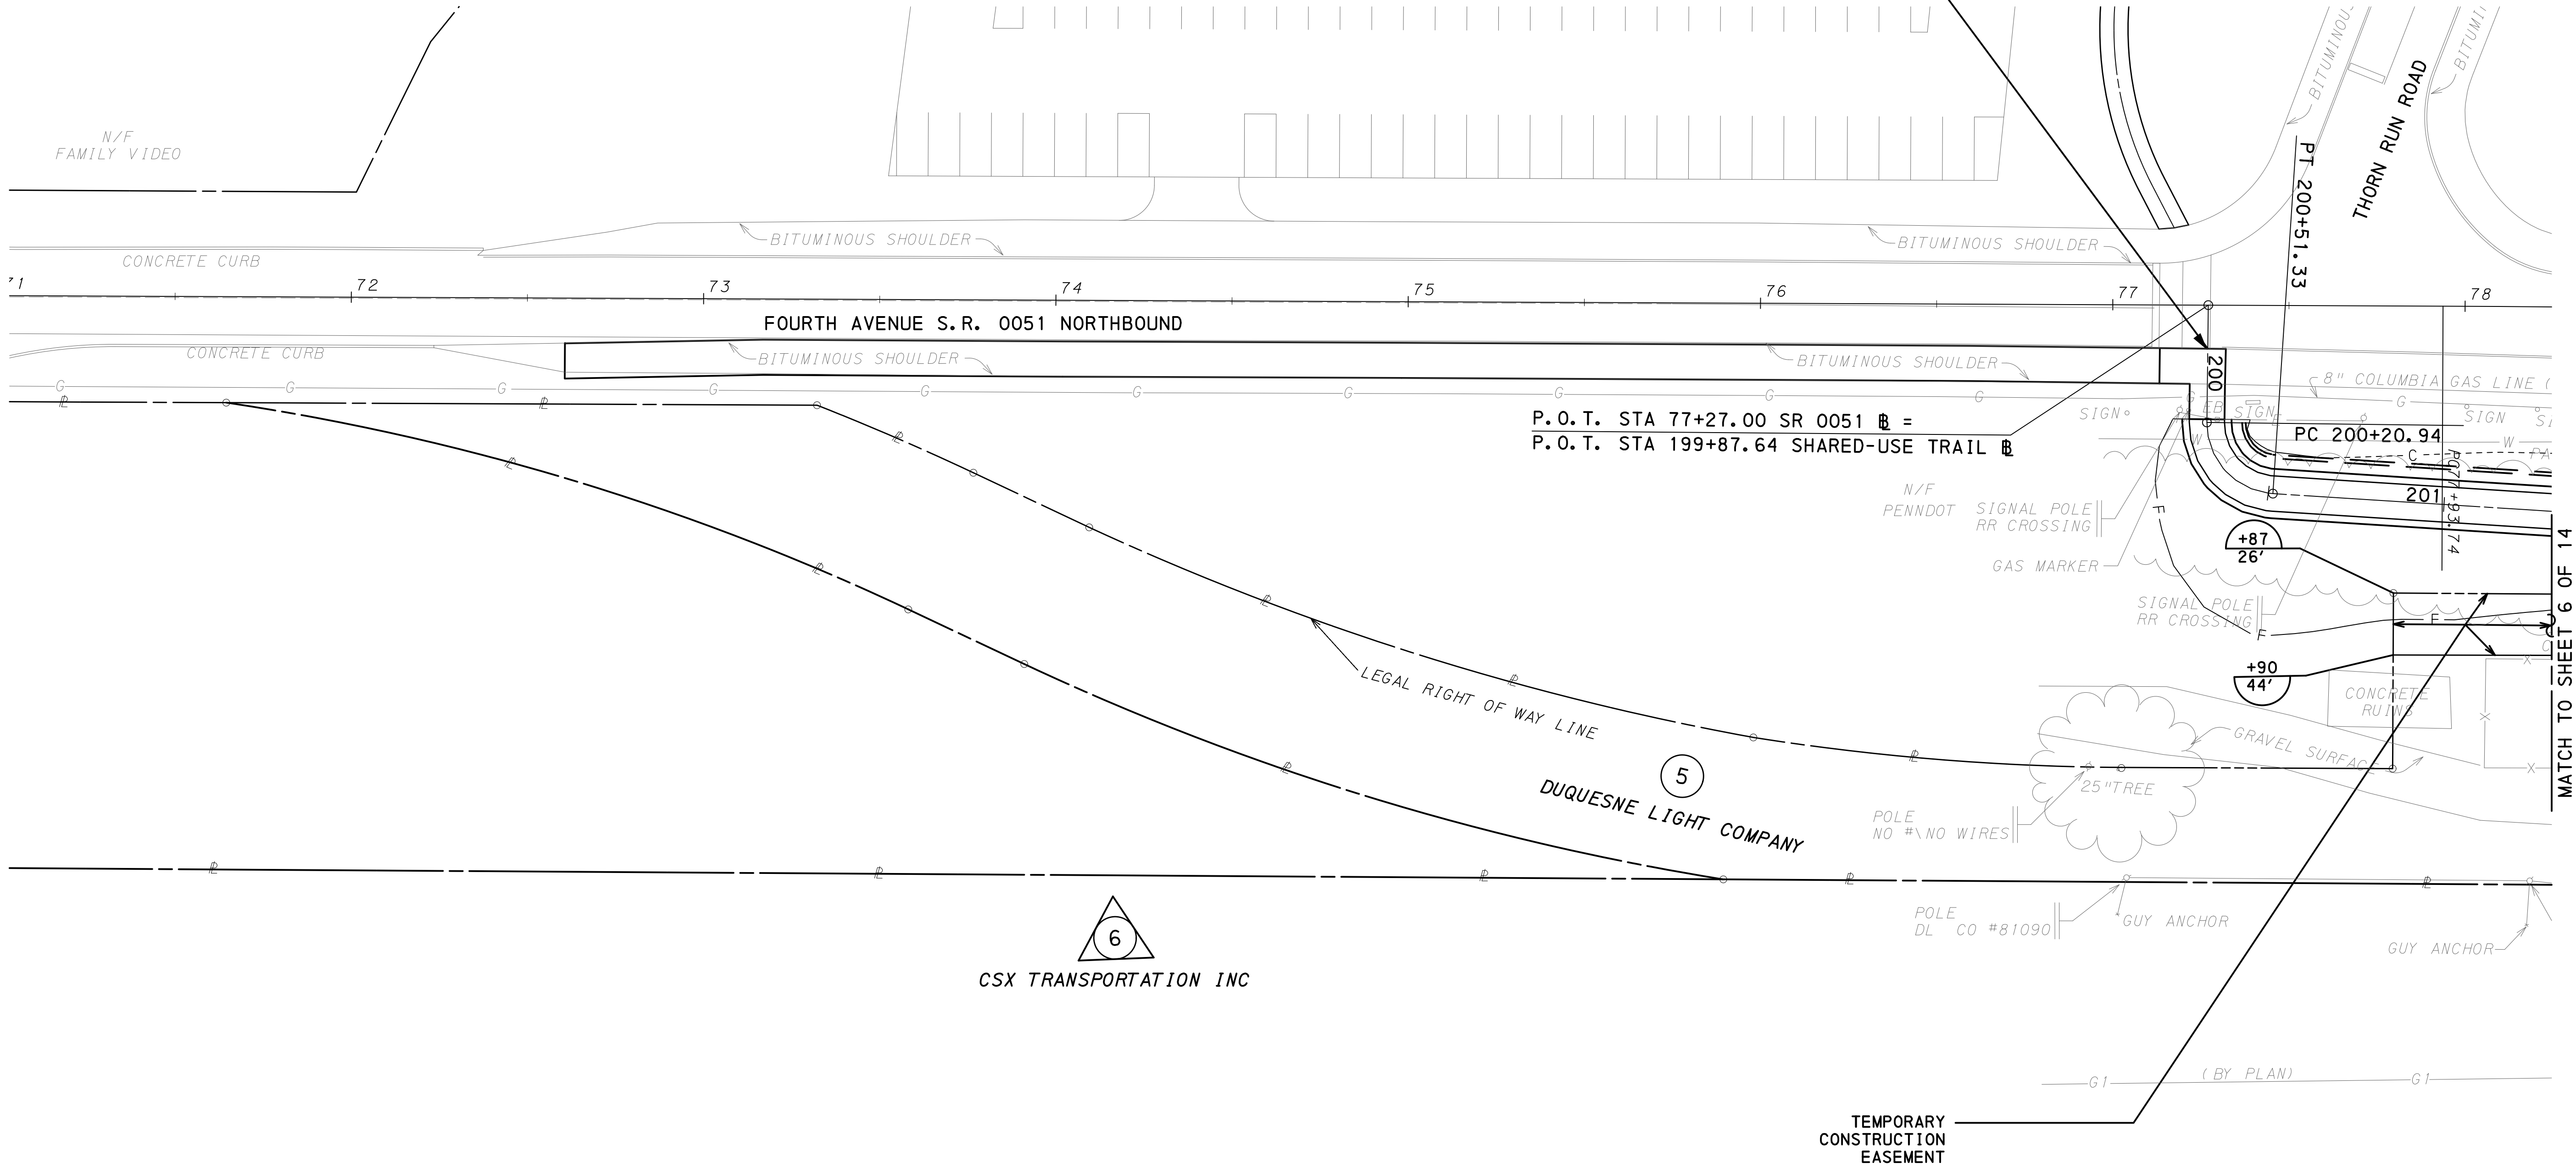

LEGEND

- | | | |
|----------------------|-------------------|---|
| - G - GAS LINE | -GV- GAS VALVE | -MH- MANHOLE |
| - D - DATA LINE | -GM- GAS METER | ☼ LIGHT STANDARD |
| - T - TELEPHONE LINE | -CO- CLEAN OUT | -WB- WATER BOX |
| - E - ELECTRIC LINE | -FH- FIRE HYDRANT | -WV- WATER VALVE |
| - S - SANITARY SEWER | -EB- ELECTRIC BOX | --- EXISTING CONTOURS |
| == STORM SEWER | -UG- UNDERGROUND | — EXISTING CONDITIONS (PAVEMENTS, WALKS, CURBS, ETC.) |
| | | — PROPOSED IMPROVEMENTS |


FOR PROFILE OHIO RIVER TRAIL PHASE 1
SEE SHEET 10

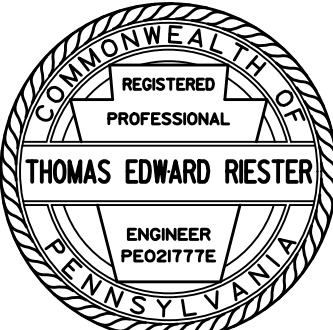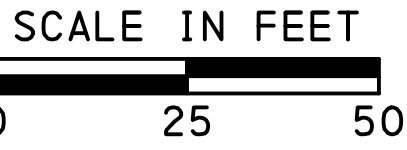

DISTRICT	COUNTY	ROUTE	SECTION	SHEET
11-0	ALLEGHENY	OHIO RIVER TRAIL PHASE 1		6 OF 14
MOON TOWNSHIP & BOROUGH OF CORAOPOLIS				
REVISION NUMBER	REVISIONS			DATE

TRAIL EASEMENT: AN EASEMENT FOR THE CONSTRUCTION, INSPECTION, MAINTENANCE, REPAIR, RECONSTRUCTION, AND ALTERATION OF TRAIL. THE EASEMENT SHALL NOT PREVENT THE PROPERTY OWNER FROM MAKING ANY LEGAL USE OF THE AREA WHICH IS NOT DETRIMENTAL TO THE TRAIL AND THE SAFETY OF THE TRAIL USERS. HOWEVER, NO STRUCTURE OF ANY KIND MAY BE ERECTED IN THE TRAIL EASEMENT AREA WITHOUT ADVANCED WRITTEN APPROVAL BY THE OWNER OF TRAIL EASEMENT.

TEMPORARY CONSTRUCTION EASEMENT. AN EASEMENT TO USE THE LAND AS NECESSARY DURING CONSTRUCTION OF THE PROJECT. THE EASEMENT IS REQUIRED ONLY UNTIL THE CONSTRUCTION OR WORK INDICATED BY THE PLAN IS COMPLETED, UNLESS SOONER RELINQUISHED IN WRITING BY THE BOROUGH OF CORAOPOLIS.

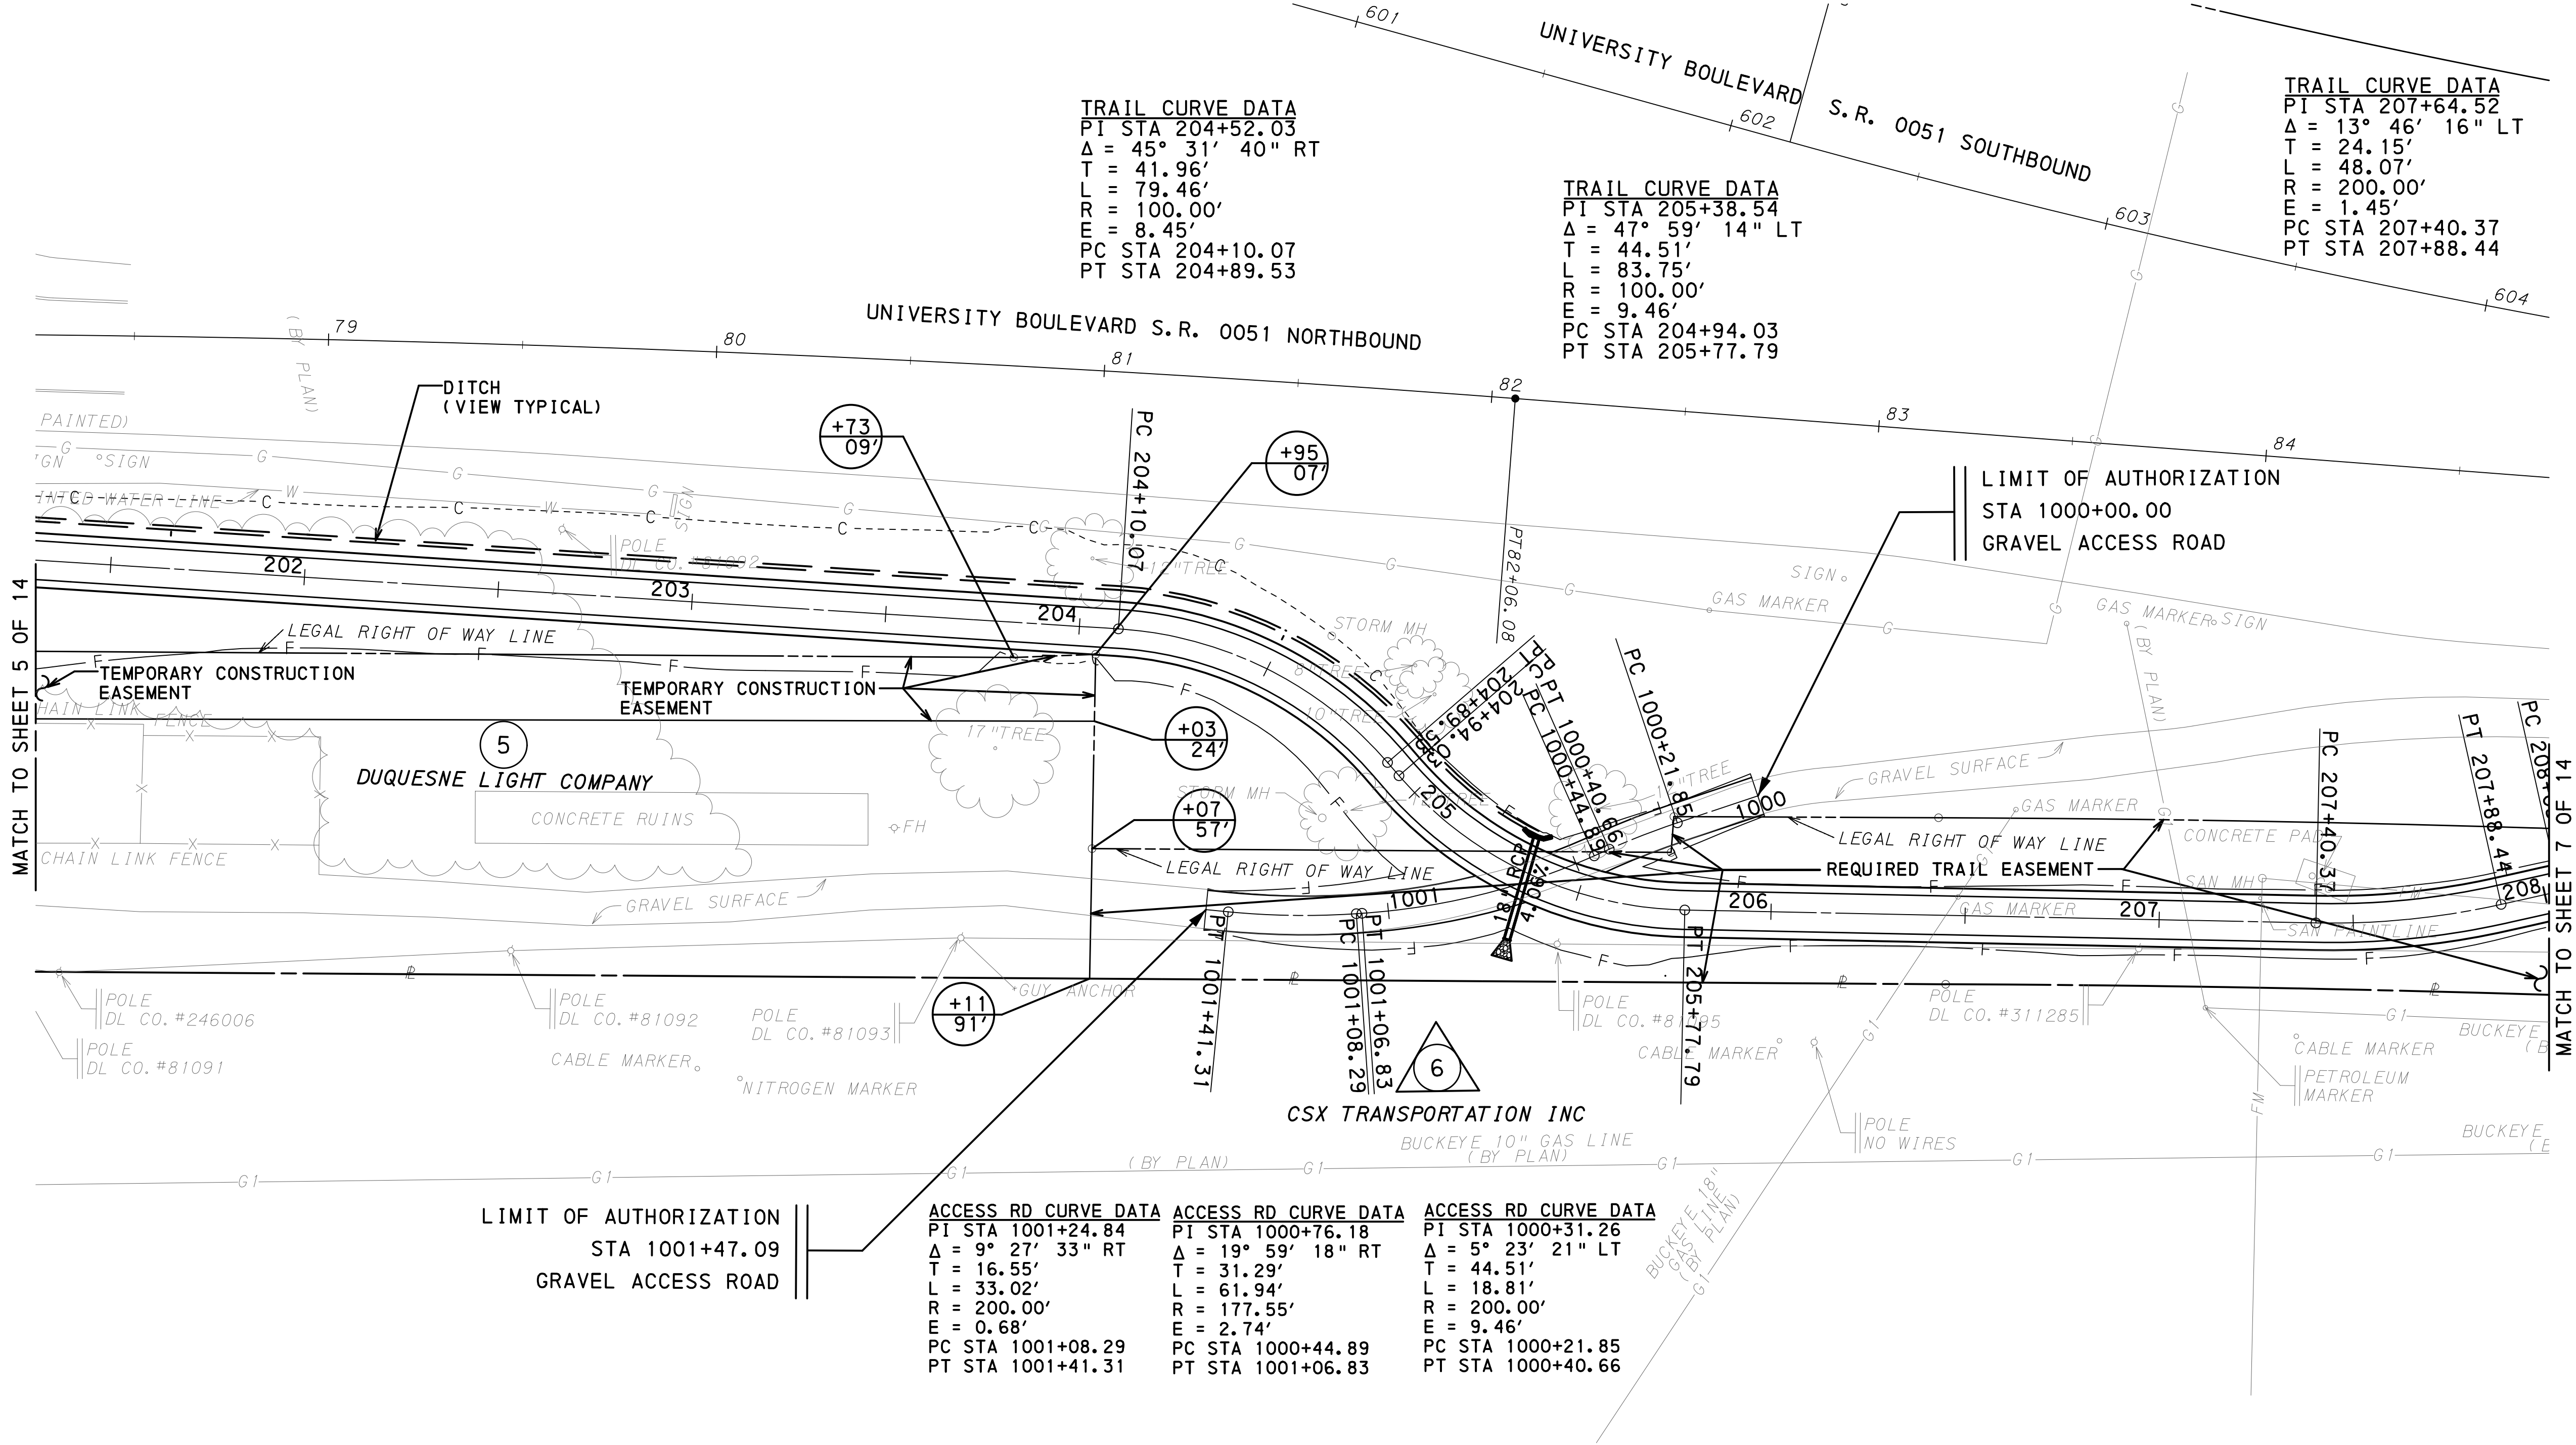


LEGEND

- | | | | | | |
|--------|----------------|--------|--------------|--------|---|
| - G - | GAS LINE | - GV - | GAS VALVE | - MH - | MANHOLE |
| - D - | DATA LINE | - GM - | GAS METER | - LS - | LIGHT STANDARD |
| - T - | TELEPHONE LINE | - CO - | CLEAN OUT | - WB - | WATER BOX |
| - E - | ELECTRIC LINE | - FH - | FIRE HYDRANT | - WV - | WATER VALVE |
| - S - | SANITARY SEWER | - EB - | ELECTRIC BOX | - EC - | EXISTING CONTOURS |
| - SS - | STORM SEWER | - UG - | UNDERGROUND | - EC - | EXISTING CONDITIONS (PAVEMENTS, WALKS, CURBS, ETC.) |
| | | | | - P - | PROPOSED IMPROVEMENTS |

SCALE IN FEET

0 25 50

FOR PROFILE OHIO RIVER TRAIL PHASE 1
SEE SHEETS 10 & 11

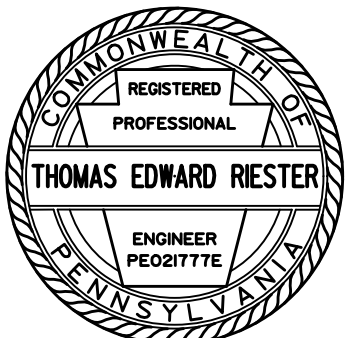


DISTRICT	COUNTY	ROUTE	SECTION	SHEET
11-0	ALLEGHENY	OHIO RIVER TRAIL PHASE 1		8 OF 14
MOON TOWNSHIP & BOROUGH OF CORAOPOLIS				
REVISION NUMBER	REVISIONS			DATE

TRAIL EASEMENT: AN EASEMENT FOR THE CONSTRUCTION, INSPECTION, MAINTENANCE, REPAIR, RECONSTRUCTION, AND ALTERATION OF TRAIL. THE EASEMENT SHALL NOT PREVENT THE PROPERTY OWNER FROM MAKING ANY LEGAL USE OF THE AREA WHICH IS NOT DETRIMENTAL TO THE TRAIL AND THE SAFETY OF THE TRAIL USERS. HOWEVER, NO STRUCTURE OF ANY KIND MAY BE ERECTED IN THE TRAIL EASEMENT AREA WITHOUT ADVANCED WRITTEN APPROVAL BY THE OWNER OF TRAIL EASEMENT.

TEMPORARY CONSTRUCTION EASEMENT. AN EASEMENT TO USE THE LAND AS NECESSARY DURING CONSTRUCTION OF THE PROJECT. THE EASEMENT IS REQUIRED ONLY UNTIL THE CONSTRUCTION OR WORK INDICATED BY THE PLAN IS COMPLETED, UNLESS SOONER RELINQUISHED IN WRITING BY THE BOROUGH OF CORAOPOLIS.

TRAIL CURVE DATA
PI STA 215+91.99
Δ = 10° 35' 11" LT
T = 92.65'
L = 184.77'
R = 1000.00'
E = 4.28'
PC STA 214+99.34
PT STA 216+84.11

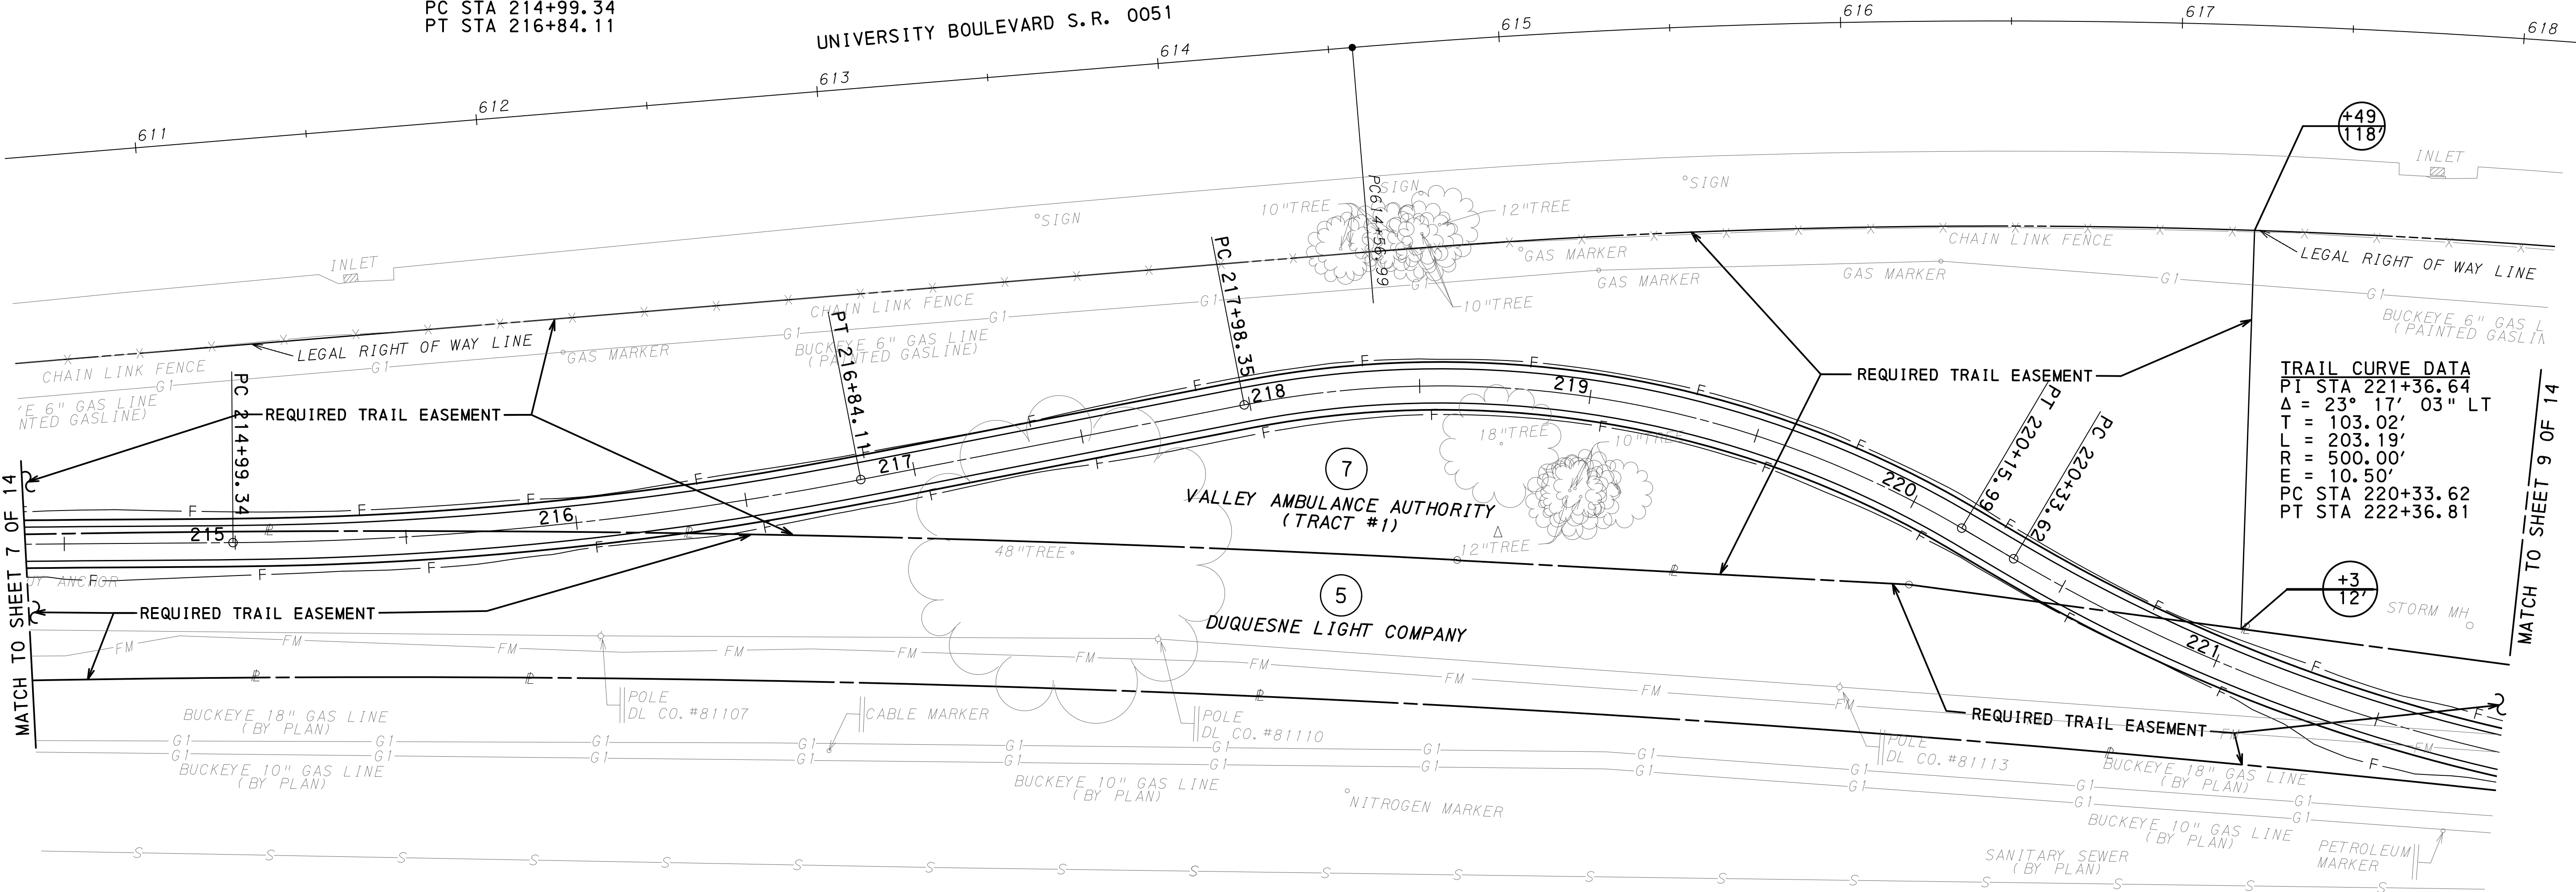


6
CSX TRANSPORTATION INC

TRAIL CURVE DATA
PI STA 219+12.21
Δ = 41° 33' 56" RT
T = 113.86'
L = 217.64'
R = 300.00'
E = 20.88'
PC STA 217+98.35
PT STA 220+15.99

- LEGEND**
- | | | |
|----------------------|-------------------|---|
| - G - GAS LINE | -GV- GAS VALVE | -MH- MANHOLE |
| - D - DATA LINE | -GM- GAS METER | ★ LIGHT STANDARD |
| - T - TELEPHONE LINE | -CO- CLEAN OUT | -WB- WATER BOX |
| - E - ELECTRIC LINE | -FH- FIRE HYDRANT | -WV- WATER VALVE |
| - S - SANITARY SEWER | -EB- ELECTRIC BOX | --- EXISTING CONTOURS |
| == STORM SEWER | -UG- UNDERGROUND | — EXISTING CONDITIONS (PAVEMENTS, WALKS, CURBS, ETC.) |
| | | — PROPOSED IMPROVEMENTS |

FOR PROFILE OHIO RIVER TRAIL PHASE 1
SEE SHEETS 11 & 12


SCALE IN FEET
0 25 50

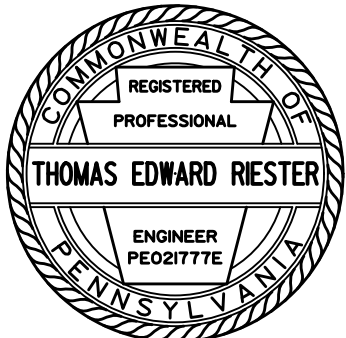

DISTRICT	COUNTY	ROUTE	SECTION	SHEET
11-0	ALLEGHENY	OHIO RIVER TRAIL PHASE 1		9 OF 14
MOON TOWNSHIP & BOROUGH OF CORAOPOLIS				
REVISION NUMBER	REVISIONS			DATE

TRAIL EASEMENT: AN EASEMENT FOR THE CONSTRUCTION, INSPECTION, MAINTENANCE, REPAIR, RECONSTRUCTION, AND ALTERATION OF TRAIL. THE EASEMENT SHALL NOT PREVENT THE PROPERTY OWNER FROM MAKING ANY LEGAL USE OF THE AREA WHICH IS NOT DETRIMENTAL TO THE TRAIL AND THE SAFETY OF THE TRAIL USERS. HOWEVER, NO STRUCTURE OF ANY KIND MAY BE ERECTED IN THE TRAIL EASEMENT AREA WITHOUT ADVANCED WRITTEN APPROVAL BY THE OWNER OF TRAIL EASEMENT.

TEMPORARY CONSTRUCTION EASEMENT. AN EASEMENT TO USE THE LAND AS NECESSARY DURING CONSTRUCTION OF THE PROJECT. THE EASEMENT IS REQUIRED ONLY UNTIL THE CONSTRUCTION OR WORK INDICATED BY THE PLAN IS COMPLETED, UNLESS SOONER RELINQUISHED IN WRITING BY THE BOROUGH OF CORAOPOLIS.

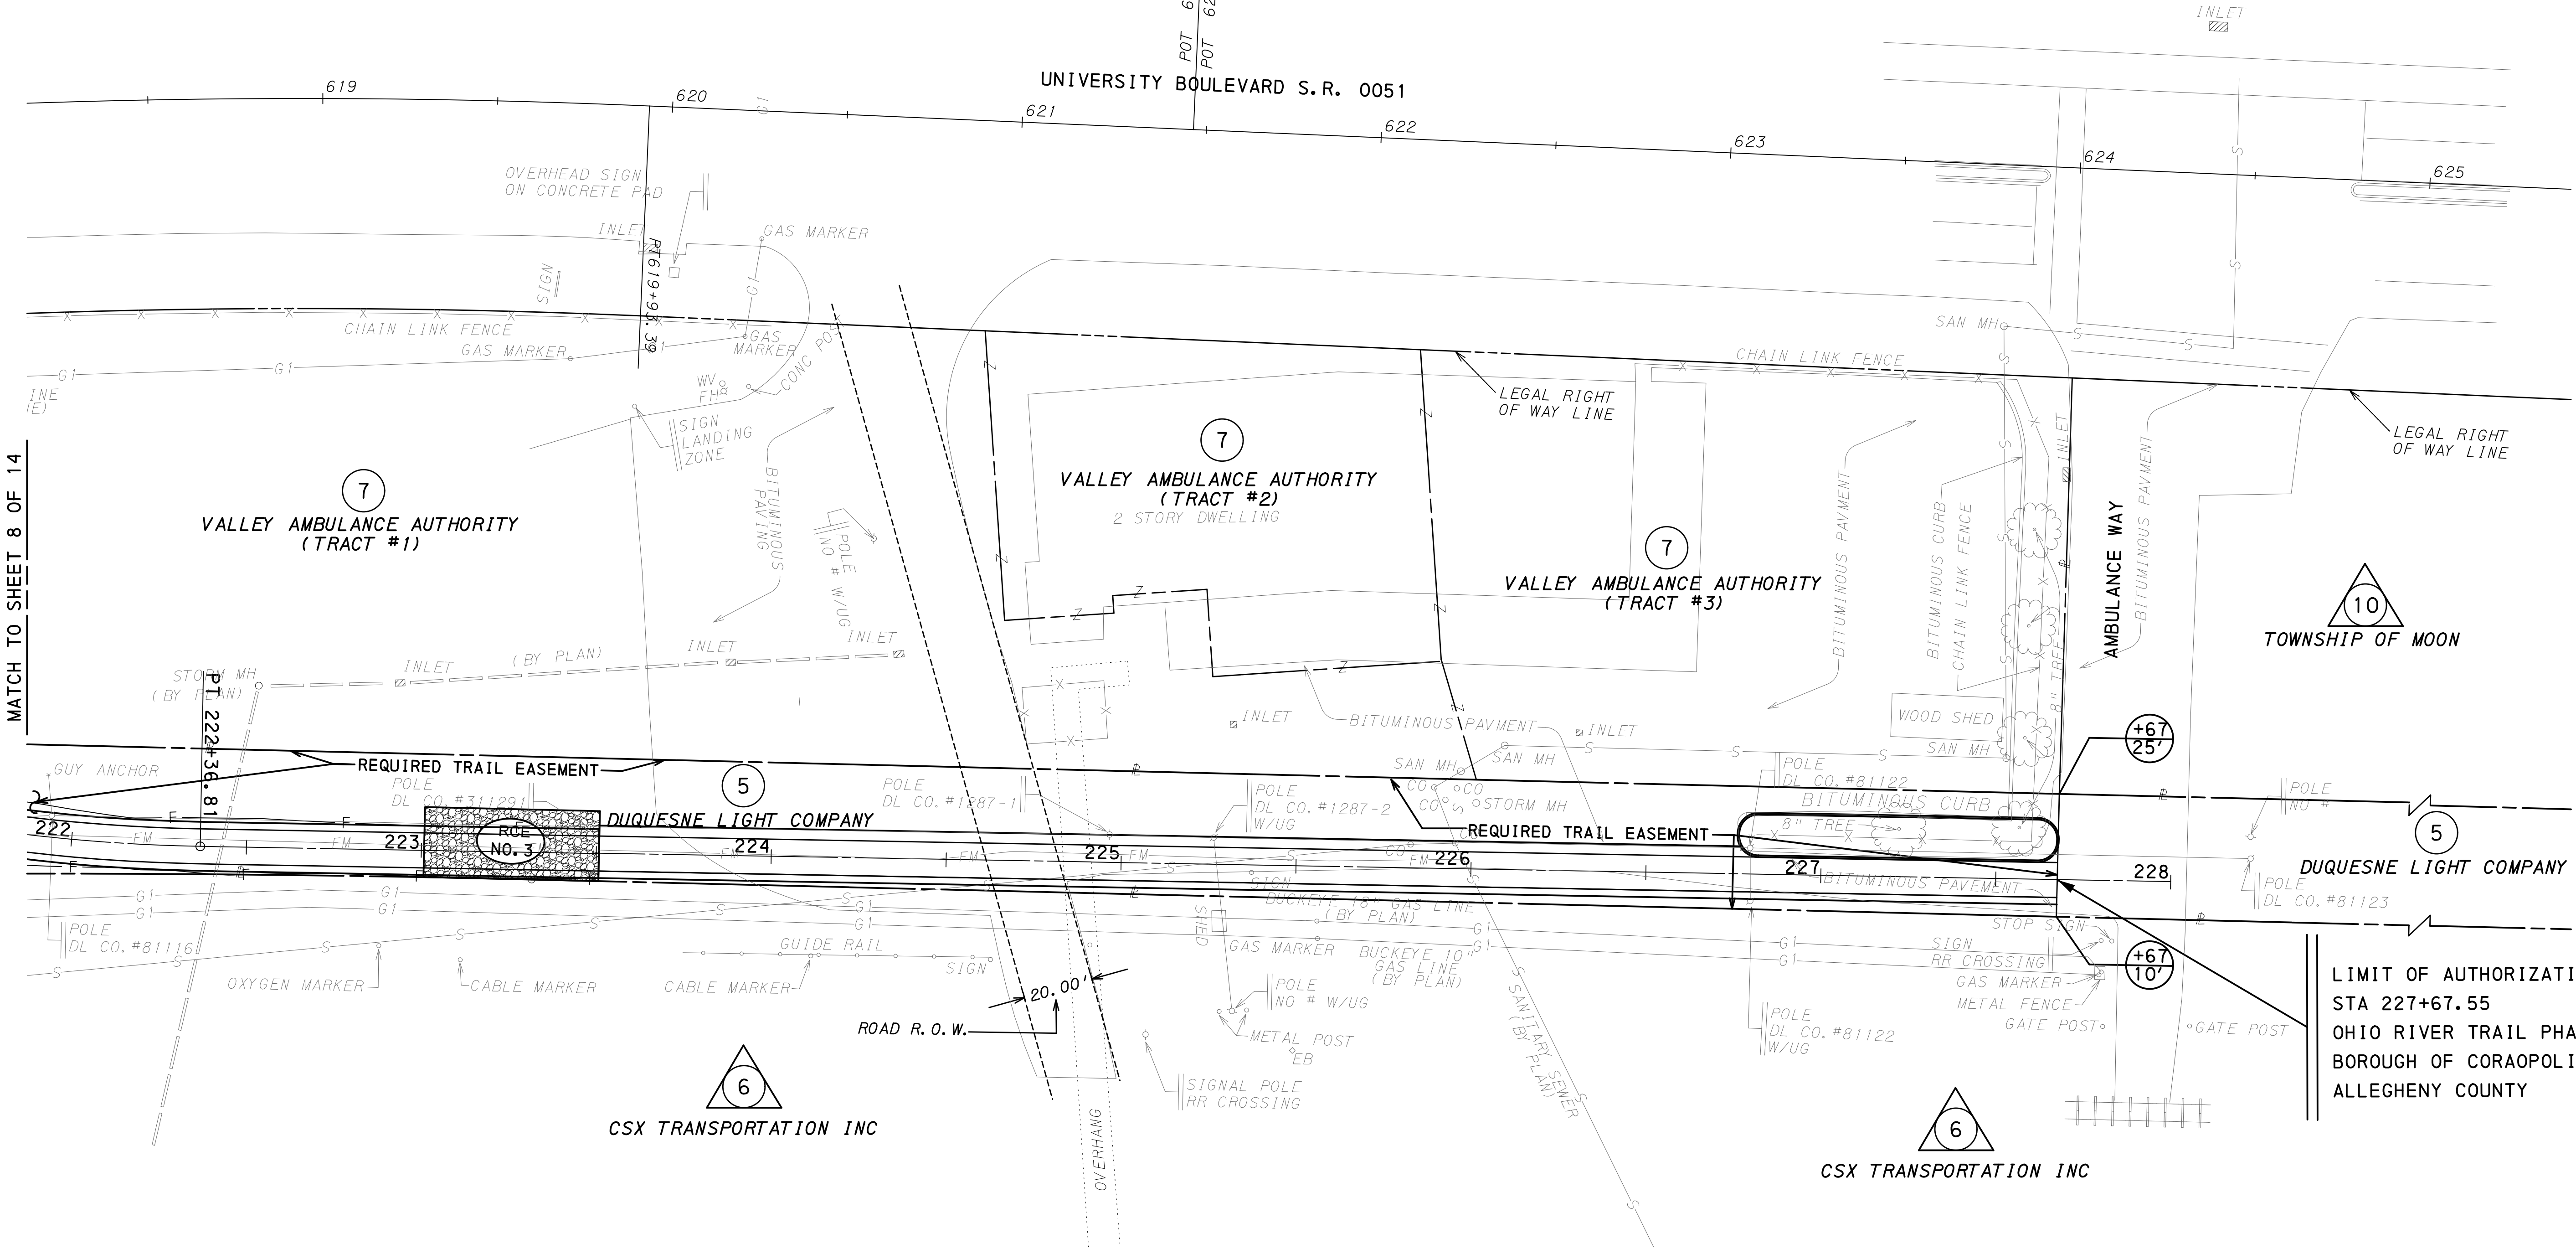



LEGEND

- | | | |
|----------------------|---------------------|---|
| - G - GAS LINE | - GV - GAS VALVE | - MH - MANHOLE |
| - D - DATA LINE | - GM - GAS METER | ★ LIGHT STANDARD |
| - T - TELEPHONE LINE | - CO - CLEAN OUT | - WB - WATER BOX |
| - E - ELECTRIC LINE | - FH - FIRE HYDRANT | - WV - WATER VALVE |
| - S - SANITARY SEWER | - EB - ELECTRIC BOX | --- EXISTING CONTOURS |
| == STORM SEWER | - UG - UNDERGROUND | --- EXISTING CONDITIONS (PAVEMENTS, WALKS, CURBS, ETC.) |
| | | --- PROPOSED IMPROVEMENTS |

FOR PROFILE OHIO RIVER TRAIL PHASE 1
SEE SHEETS 12 & 13

SCALE IN FEET

0 25 50

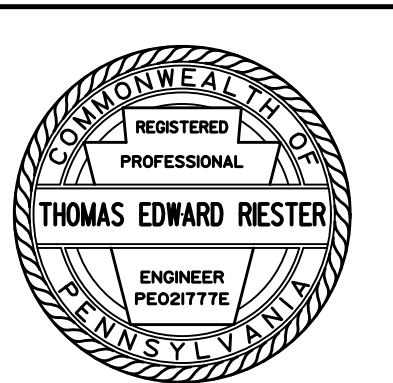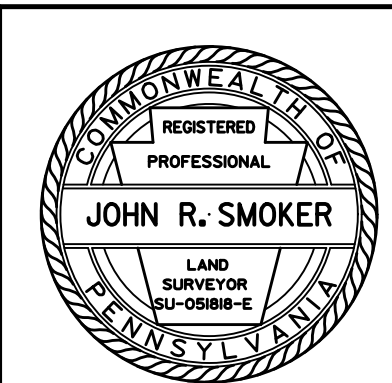


DISTRICT	COUNTY	ROUTE	SECTION	SHEET
11-0	ALLEGHENY	OHIO RIVER TRAIL PHASE 1		10 OF 14
MOON TOWNSHIP & BOROUGH OF CORAOPOLIS				
REVISION NUMBER	REVISIONS			DATE

LIMIT OF AUTHORIZATION
STA 200+00.00
OHIO RIVER TRAIL PHASE 1
BOROUGH OF CORAOPOLIS
ALLEGHENY COUNTY


PVI STA = 201+50.60
ELEV = 728.96
MO = 0.21'
VC = 100.00'
HLSD = NA

PVI STA = 204+39.89
ELEV = 723.79
MO = 0.18'
VC = 100.00'
SSD = NA

PVI STA = 205+71.12
ELEV = 719.56
MO = 0.46'
VC = 100.00'
HLSD = NA

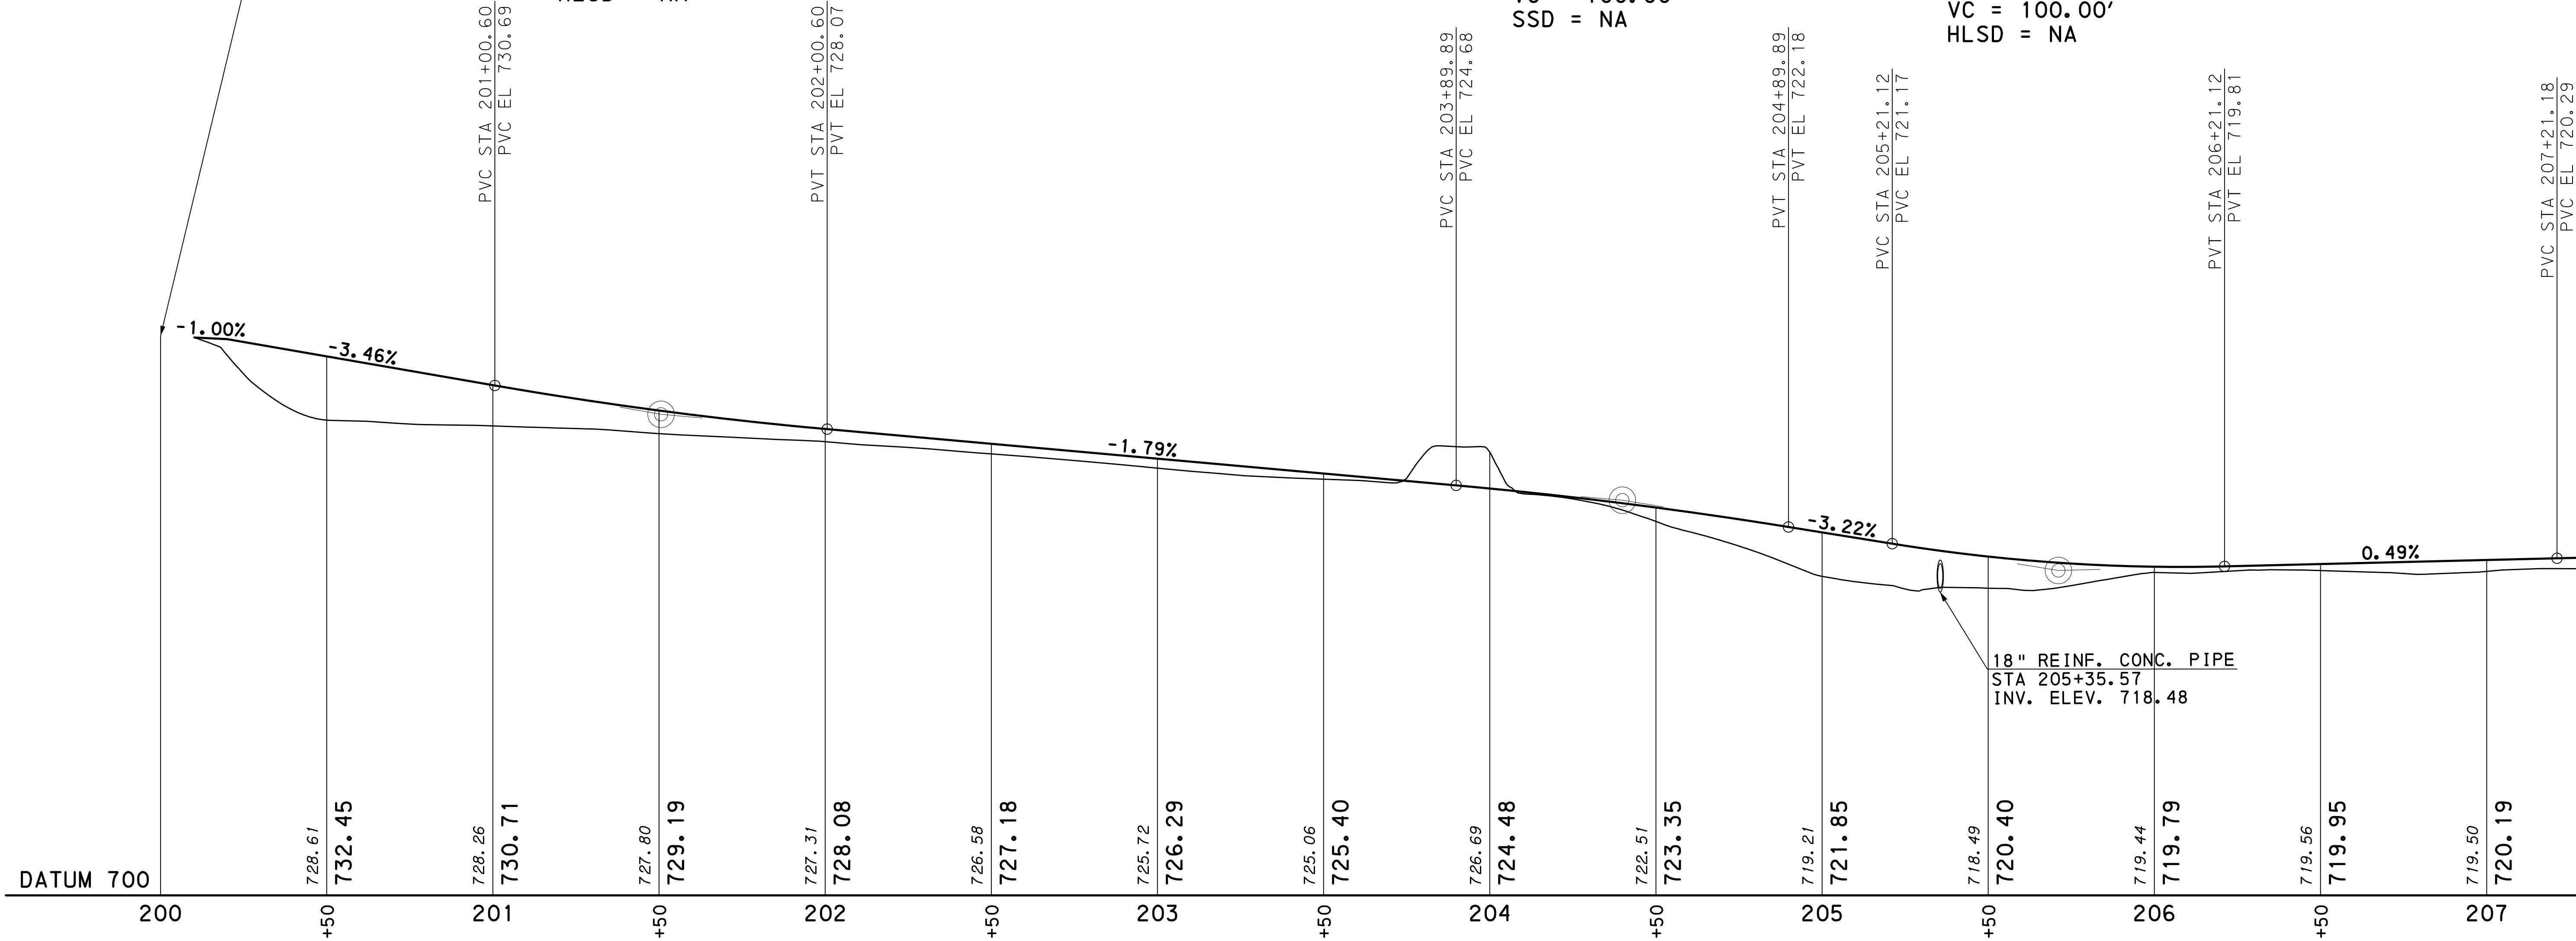


OHIO RIVER TRAIL PHASE 1

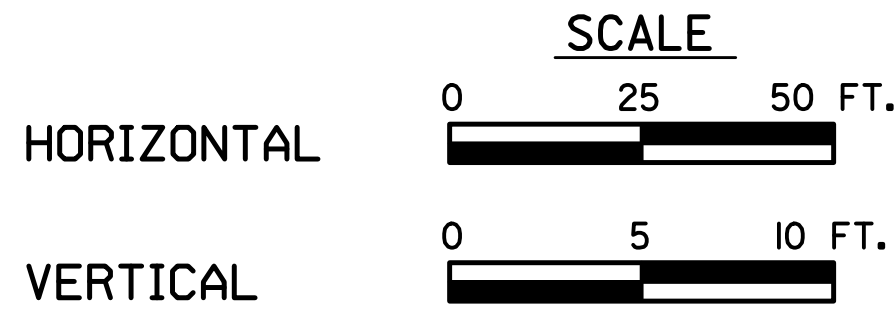


SURVEY BOOK NOS.


FOR PLAN OHIO RIVER TRAIL PHASE 1
SEE SHEETS 5 & 6

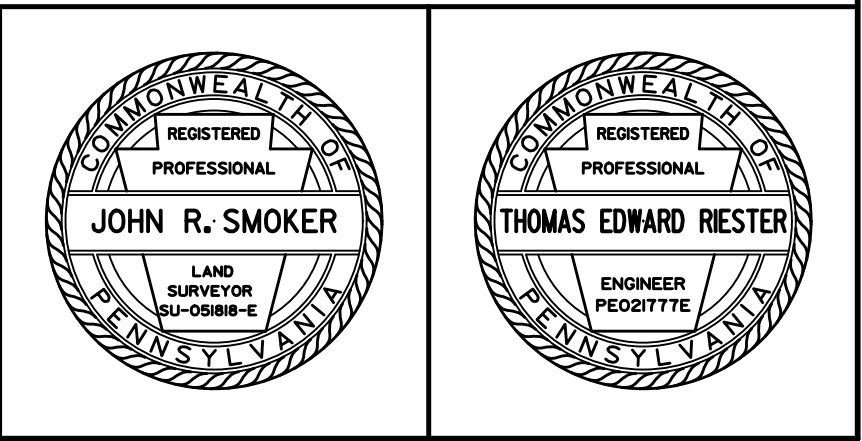

DISTRICT	COUNTY	ROUTE	SECTION	SHEET
11-0	ALLEGHENY	OHIO RIVER TRAIL PHASE 1		11 OF 14
MOON TOWNSHIP & BOROUGH OF CORAOPOLIS				
REVISION NUMBER	REVISIONS			DATE

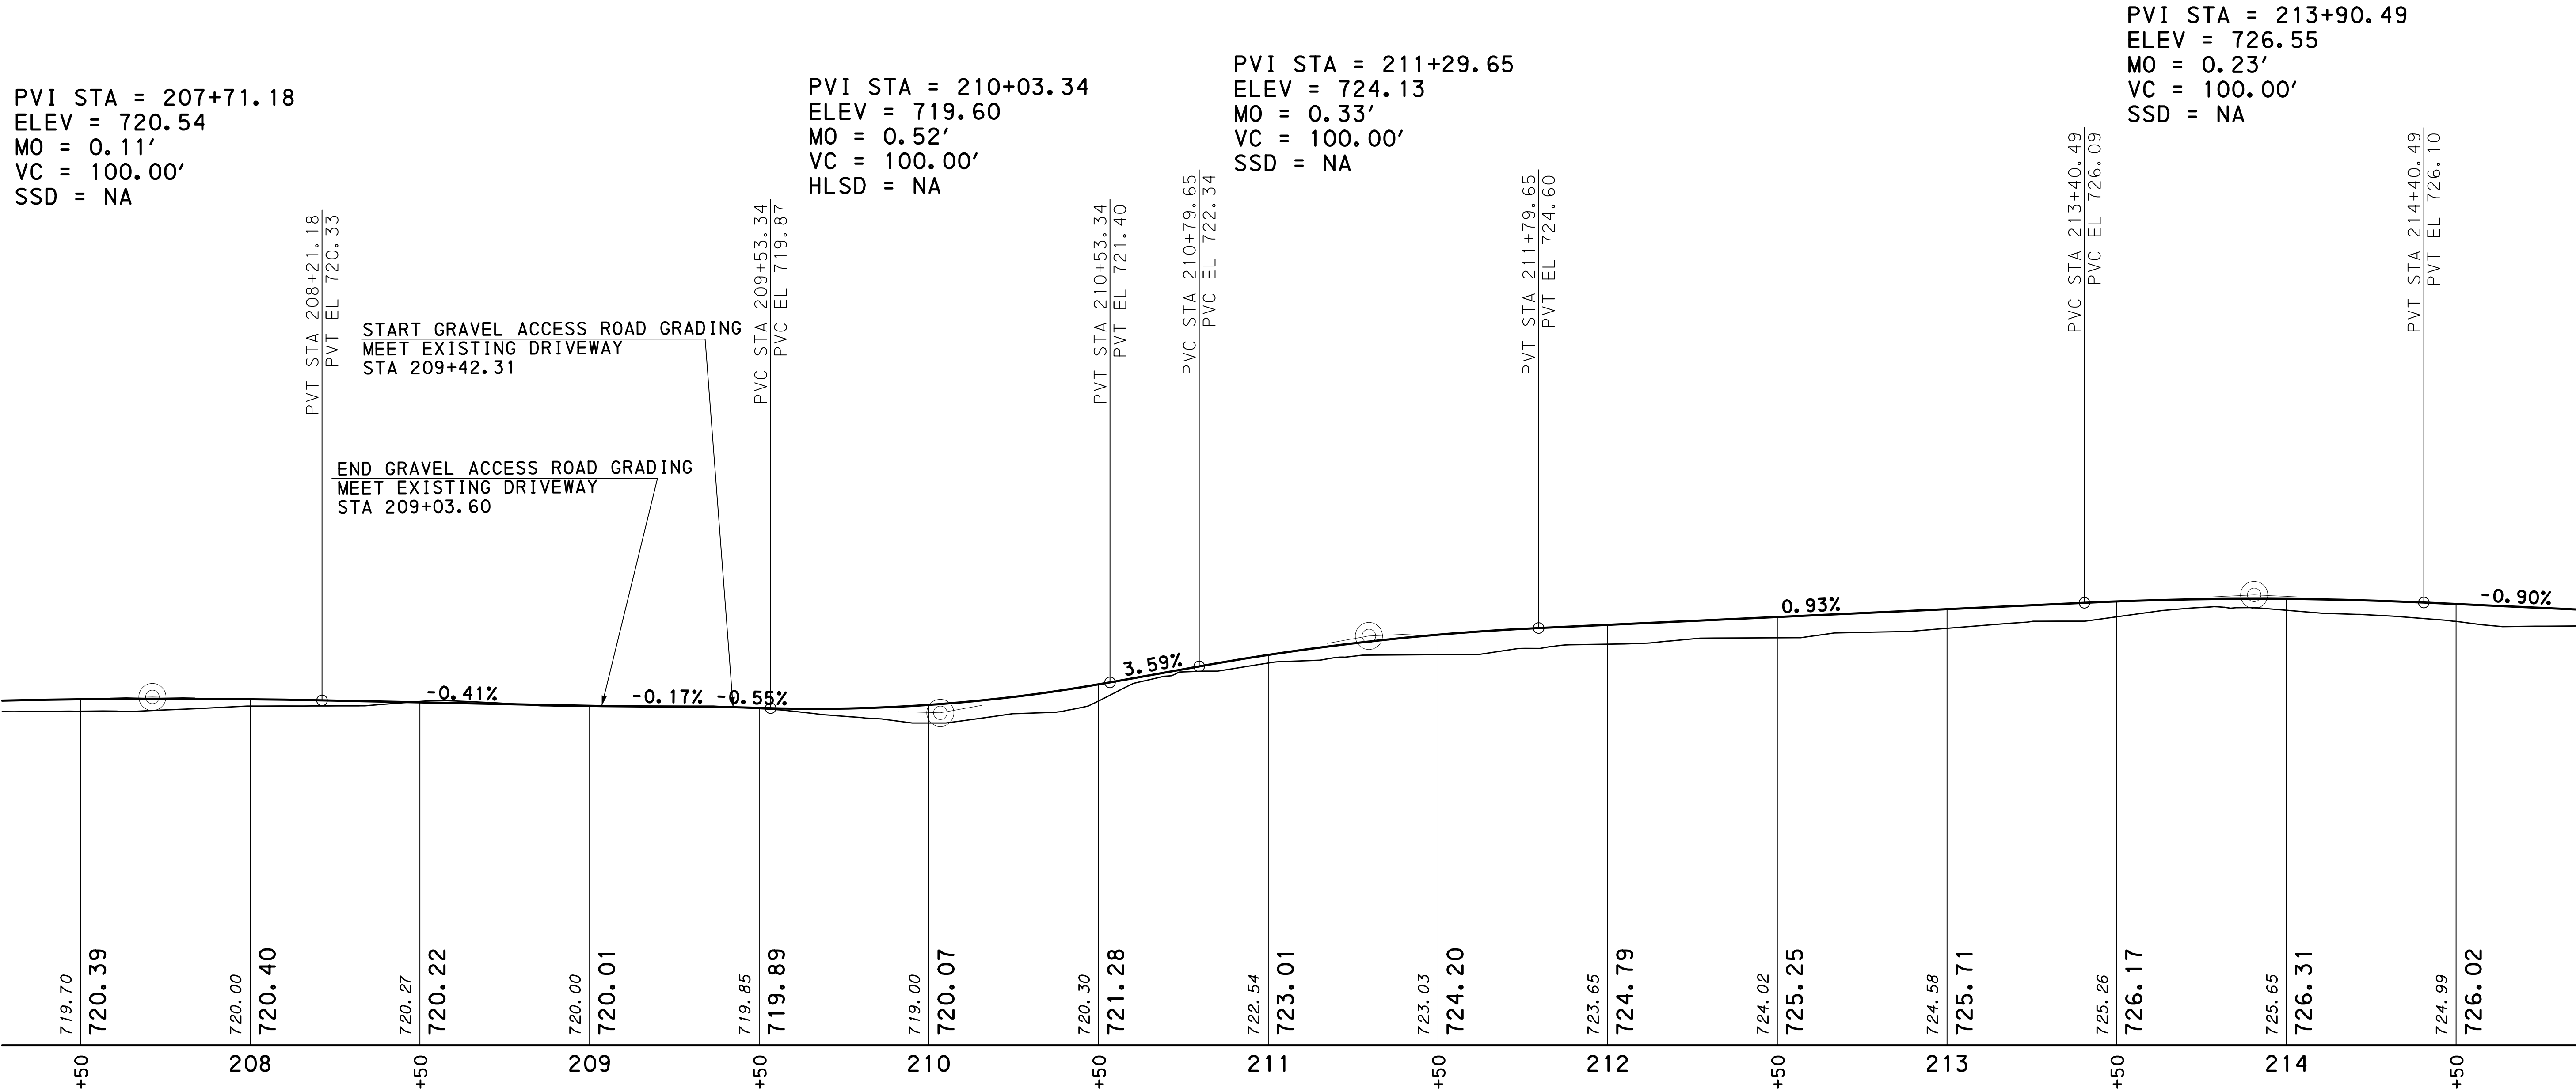


OHIO RIVER TRAIL PHASE 1

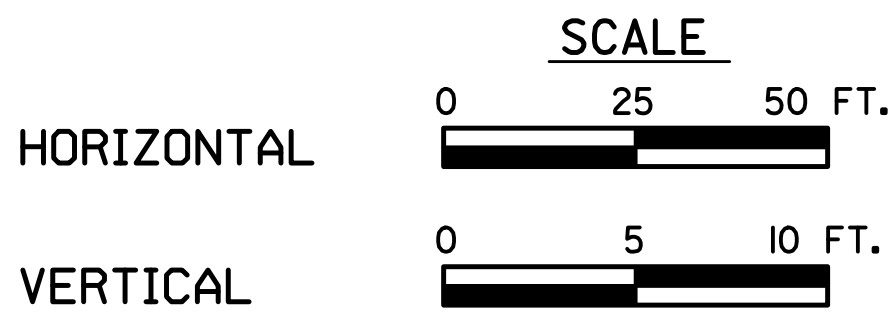


SURVEY BOOK NOS.


FOR PLAN OHIO RIVER TRAIL PHASE 1
SEE SHEETS 6 & 7

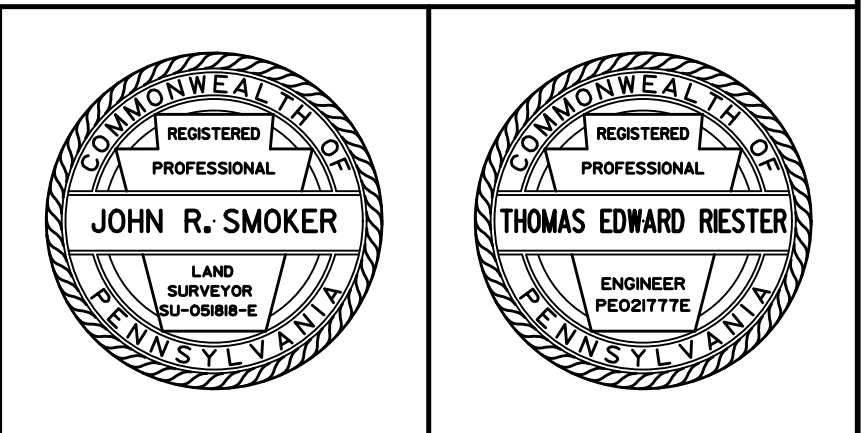

DISTRICT	COUNTY	ROUTE	SECTION	SHEET
11-0	ALLEGHENY	OHIO RIVER TRAIL PHASE 1		12 OF 14
MOON TOWNSHIP & BOROUGH OF CORAOPOLIS				
REVISION NUMBER	REVISIONS			DATE

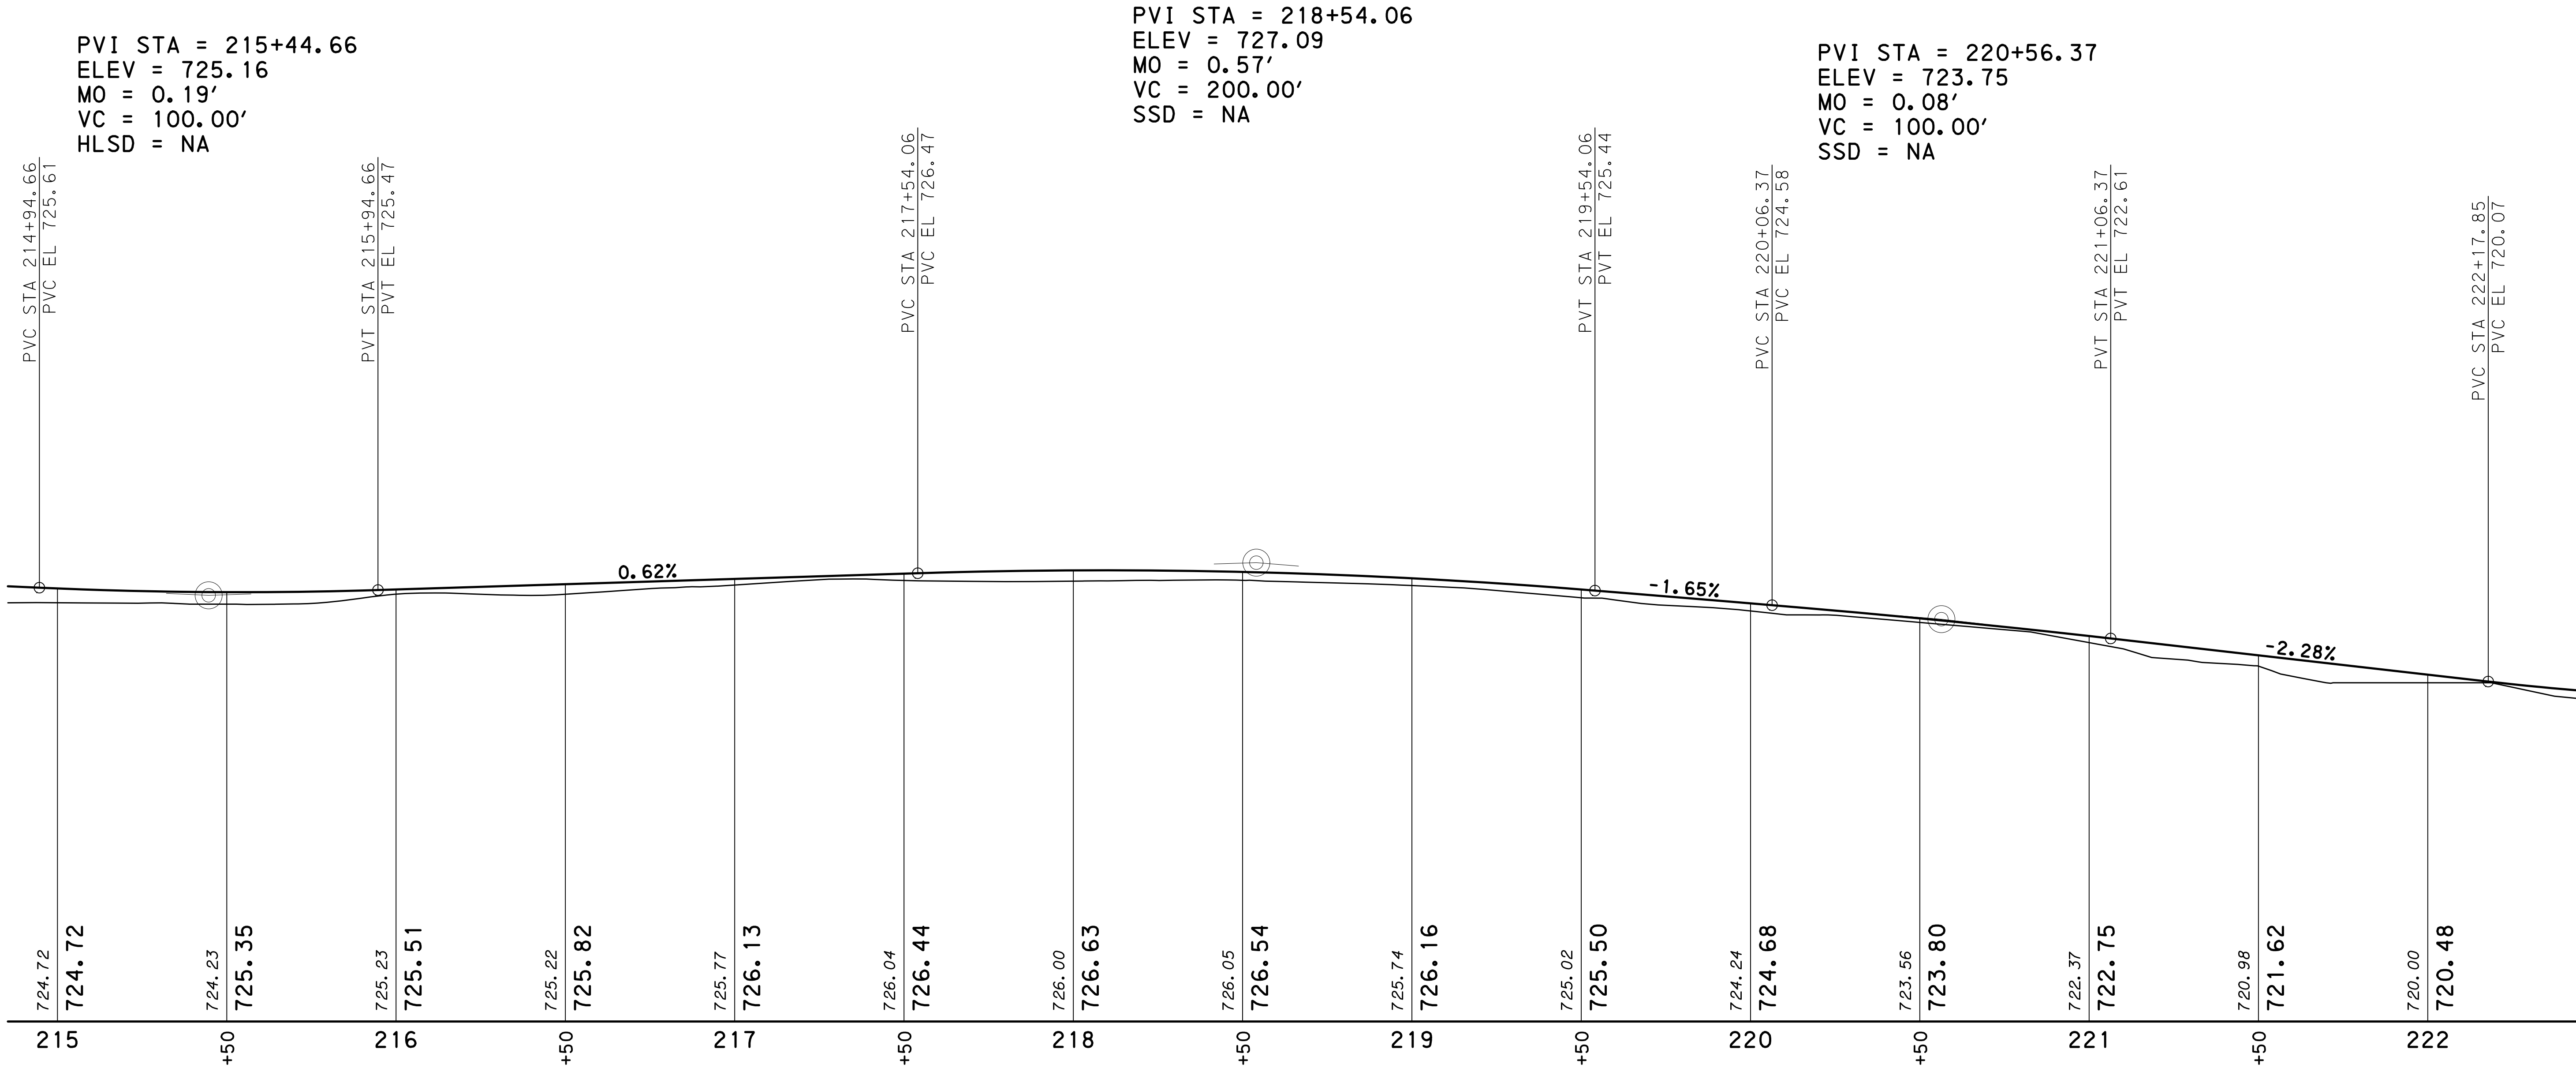


OHIO RIVER TRAIL PHASE 1

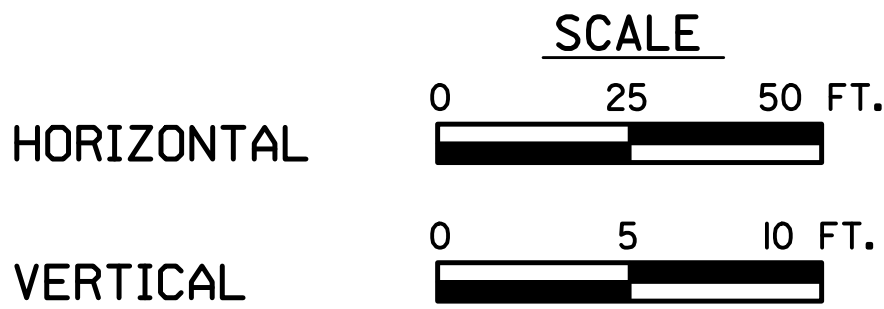

SURVEY BOOK NOS.

FOR PLAN OHIO RIVER TRAIL PHASE 1
SEE SHEET 8

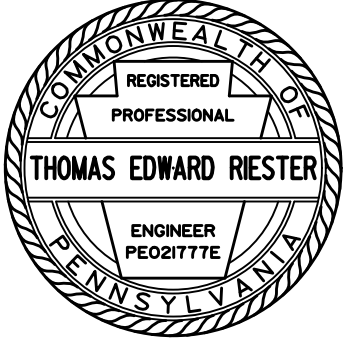

DISTRICT	COUNTY	ROUTE	SECTION	SHEET
11-0	ALLEGHENY	OHIO RIVER TRAIL PHASE 1		13 OF 14
MOON TOWNSHIP & BOROUGH OF CORAOPOLIS				
REVISION NUMBER	REVISIONS			DATE

PVI STA = 1000+77.83
ELEV = 720.73
MO = 0.13'
VC = 20.00'
SSD = NA

PVI STA = 1000+32.94
ELEV = 720.39
MO = 0.16'
VC = 37.89'
HLSD = NA

LIMIT OF AUTHORIZATION
STA 1001+47.09
GRAVEL ACCESS ROAD
BOROUGH OF CORAOPOLIS
ALLEGHENY COUNTY


LIMIT OF AUTHORIZATION
STA 1001+47.09
GRAVEL ACCESS ROAD
BOROUGH OF CORAOPOLIS
ALLEGHENY COUNTY

PVI STA = 222+67.85
ELEV = 718.93
MO = 0.29'
VC = 100.00'
HLSD = NA


DATUM 700

GRAVEL ACCESS ROAD PROFILE

LIMIT OF AUTHORIZATION
STA 227+67.55
OHIO RIVER TRAIL PHASE 1
BOROUGH OF CORAOPOLIS
ALLEGHENY COUNTY

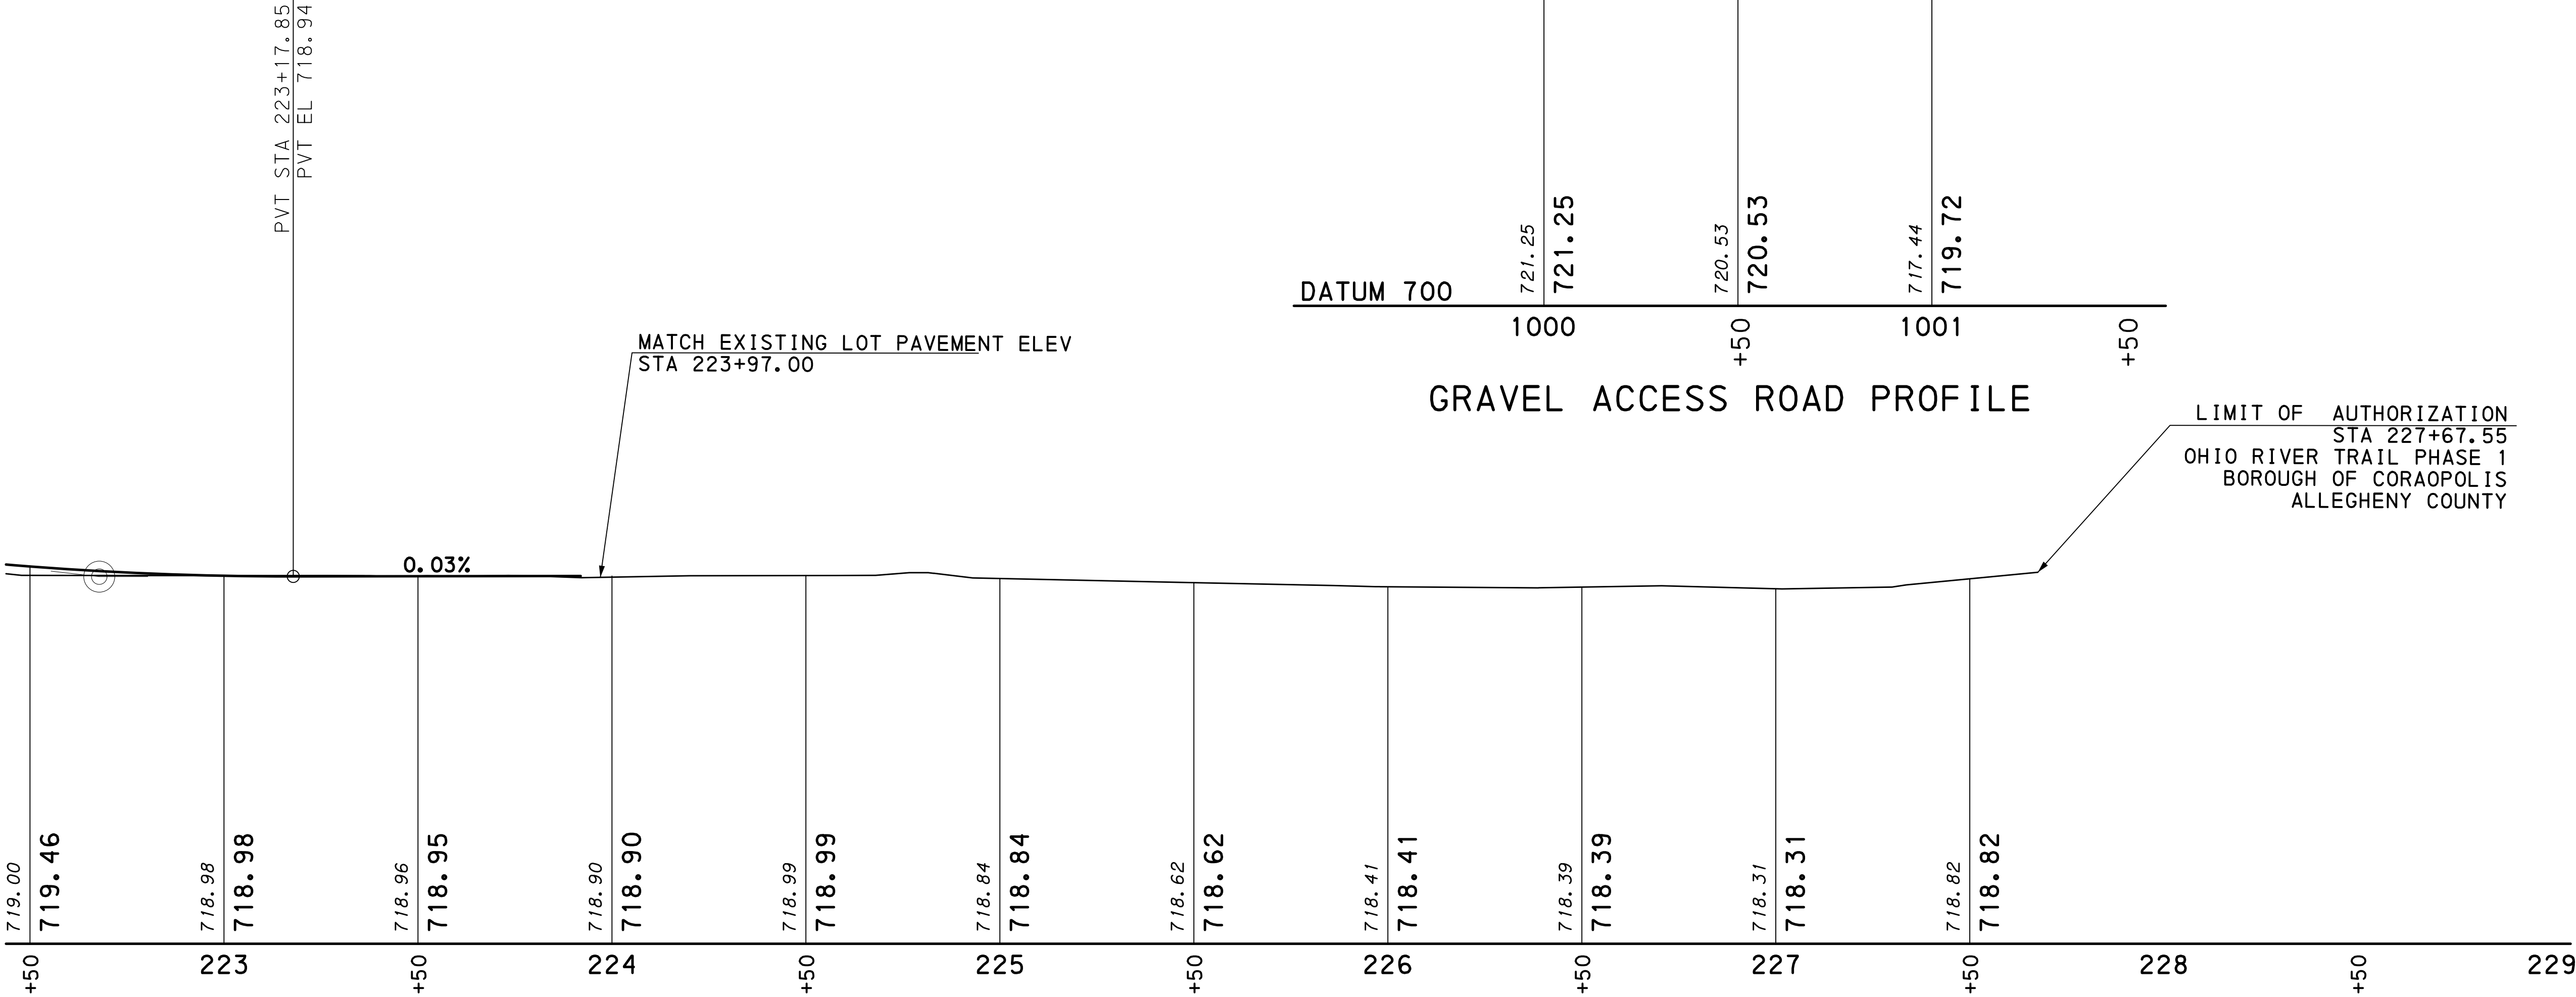


OHIO RIVER TRAIL PHASE 1

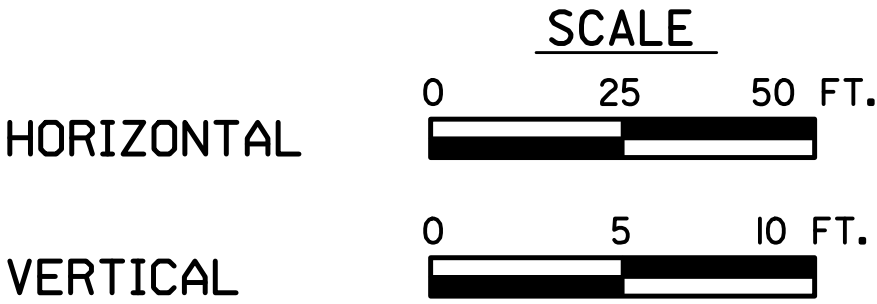

SURVEY BOOK NOS.

FOR PLAN OHIO RIVER TRAIL PHASE 1
SEE SHEET 9

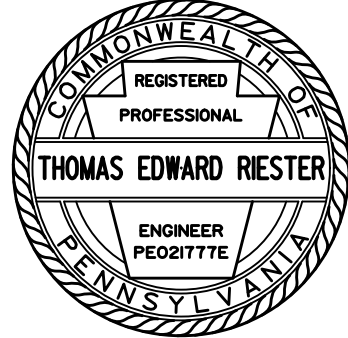

DISTRICT	COUNTY	ROUTE	SECTION	SHEET
11-0	ALLEGHENY	OHIO RIVER TRAIL PHASE 1	.	14 OF 14
MOON TOWNSHIP & BOROUGH OF CORAOPOLIS				
REVISION NUMBER	REVISIONS			DATE

RIGHT-OF-WAY CLAIM INFORMATION				
COMMONWEALTH OF PENNSYLVANIA - DEPARTMENT OF TRANSPORTATION				
RTE. OHIO RIVER TRAIL PHASE 1 BOROUGH OF CORAOPOLIS ALLEGHENY COUNTY				
PARCEL NO. 5		SHEET NO. 5-9		CLAIM NO.
PROPERTY OWNER(S) DUQUESNE LIGHT COMPANY				
GRANTOR(S) PITTSBURGH RAILWAYS COMPANY				
DEED BOOK VOLUME 3267	AREAS	ACRE / SF	REQUIRED AREA	ACRE / SF
PAGE 226	DEED	5.0793	TEMP CONSTR EASEMENT	5,391
DATE OF DEED 06-19-1953	CALCULATED		TRAIL EASEMENT	92,651
DATE OF RECORD 06-23-1953	ADVERSES			
CONSIDERATION \$23,340.20	LEGAL R/W			
P.R.T.T. N/A	EFFECTIVE			
TAX MAP PARCEL 0505-D-357	TOTAL REQ'D R/W		VERIFICATION DATE 05-04-2017	
	TOTAL RESIDUE		DRAWN BY MACKIN ENG. CO.	
	RESIDUE LT			
	RESIDUE RT		SCALE AS SHOWN	

PRIVATE PROPERTY LINES ARE PLOTTED FROM THE DEED OF RECORD, RECORDED SUBDIVISION OR LOT PLANS, EXISTING TOPOGRAPHICAL REATURES AND LIMITED FIELD DATA. PRIVATE PROPERTY LINES WERE NOT SURVEYED BY THE PROFESSIONAL LAND SURVEYOR RESPONSIBLE FOR THE PROJECT.

TEMPORARY CONSTRUCTION EASEMENT. AN EASEMENT TO USE THE LAND AS NECESSARY DURING CONSTRUCTION OF THE PROJECT. THE EASEMENT IS REQUIRED ONLY UNTIL THE CONSTRUCTION OR WORK INDICATED BY THE PLAN IS COMPLETED, UNLESS SOONER RELINQUISHED IN WRITING BY THE BOROUGH OF CORAOPOLIS.

TRAIL EASEMENT: AN EASEMENT FOR THE CONSTRUCTION, INSPECTION, MAINTENANCE, REPAIR, RECONSTRUCTION, AND ALTERATION OF TRAIL. THE EASEMENT SHALL NOT PREVENT THE PROPERTY OWNER FROM MAKING ANY LEGAL USE OF THE AREA WHICH IS NOT DETRIMENTAL TO THE TRAIL AND THE SAFETY OF THE TRAIL USERS. HOWEVER, NO STRUCTURE OF ANY KIND MAY BE ERECTED IN THE TRAIL EASEMENT AREA WITHOUT ADVANCED WRITTEN APPROVAL BY THE OWNER OF TRAIL EASEMENT.

RIGHT-OF-WAY CLAIM INFORMATION					
COMMONWEALTH OF PENNSYLVANIA - DEPARTMENT OF TRANSPORTATION					
RTE. OHIO RIVER TRAIL PHASE 1 BOROUGH OF CORAOPOLIS ALLEGHENY COUNTY					
PARCEL NO. 7		SHEET NO. 7-9		CLAIM NO.	
PROPERTY OWNER(S) VALLEY AMBULANCE AUTHORITY					
GRANTOR(S) RB&W CORPORATION					
TRACT #1	TRACT #2	TRACT #3	AREAS	ACRE / SF	REQUIRED AREA
DEED BOOK VOLUME 7953	DEED BOOK VOLUME 5445	DEED BOOK VOLUME 8542	DEED	3.128	ACRE / SF
PAGE 83	PAGE 223	PAGE 174	CALCULATED		TRAIL EASEMENT 1,325
DATE OF DEED 01/27/1989	DATE OF DEED 12/24/1974	DATE OF DEED 04/28/1988	ADVERSES		
DATE OF RECORD 01/30/1989	DATE OF RECORD 12/30/1974	DATE OF RECORD 08/09/1991	LEGAL R/W		
CONSIDERATION \$20,000	CONSIDERATION \$0.0	CONSIDERATION \$50,000	EFFECTIVE		
P.R.T.T. \$200	P.R.T.T. \$0.0	P.R.T.T. \$500	TOTAL REQ'D R/W		VERIFICATION DATE 05-04-2017
TAX MAP PARCEL 505-D-371	TAX MAP PARCEL 505-H-316	TAX MAP PARCEL 505-H-318	TOTAL RESIDUE		DRAWN BY MACKIN ENG. CO.
			RESIDUE LT		
			RESIDUE RT		SCALE AS SHOWN

PRIVATE PROPERTY LINES ARE PLOTTED FROM THE DEED OF RECORD, RECORDED SUBDIVISION OR LOT PLANS, EXISTING TOPOGRAPHICAL REATURES AND LIMITED FIELD DATA. PRIVATE PROPERTY LINES WERE NOT SURVEYED BY THE PROFESSIONAL LAND SURVEYOR RESPONSIBLE FOR THE PROJECT.

TRAIL EASEMENT: AN EASEMENT FOR THE CONSTRUCTION, INSPECTION, MAINTENANCE, REPAIR, RECONSTRUCTION, AND ALTERATION OF TRAIL. THE EASEMENT SHALL NOT PREVENT THE PROPERTY OWNER FROM MAKING ANY LEGAL USE OF THE AREA WHICH IS NOT DETRIMENTAL TO THE TRAIL AND THE SAFETY OF THE TRAIL USERS. HOWEVER, NO STRUCTURE OF ANY KIND MAY BE ERECTED IN THE TRAIL EASEMENT AREA WITHOUT ADVANCED WRITTEN APPROVAL BY THE OWNER OF TRAIL EASEMENT.

