


ROCHESTER TOWNSHIP
BOROUGH OF ROCHESTER
BEAVER COUNTY
PENNSYLVANIA

 

These maps were not prepared or intended for use as a real estate title map. The railway company does not represent or suggest that the property lines and right-of-way lines shown on the maps are accurate, or that the maps are correct. The company does not represent that it has checked this map for accuracy.

NOTE: THE TRACK CONFIGURATION AS SHOWN IS FOR HISTORICAL REFERENCE ONLY. IT IS NOT INTENDED TO REPRESENT CONRAIL'S CURRENT TRACK CONFIGURATION.

THE CENTERLINE GEOMETRY AND PROPERTY/PARCEL LINE INFORMATION DEPICTED ON THIS MAP IS BASED ON A COMPILED OF VARIOUS HISTORICAL SOURCES OF REAL PROPERTY INFORMATION WITHIN CONRAIL. WHILE EVERY EFFORT GOES INTO PRODUCING AN ACCURATE RECORD MAP, IT IS NOT BASED ON A CURRENT GROUND SURVEY, AND ACCORDINGLY, IS NOT DISTRIBUTED FOR CERTIFICATION PURPOSES.





NOTE: PARCELS REFER TO
MAP V3/14

CONRAIL
RIGHT OF WAY MAP
FORMERLY
PITTSBURGH, FORT WAYNE & CHICAGO RAILWAY
FORT WAYNE LINE
FROM STA. 1372+00.00 TO STA. 1425+00.00
LINE CODE 2202 MILEPOST 26.0 TO 27.0 VAL SECTION 7338


YOUNGSTOWN LINE
FROM STA. 0+00 TO STA. 35+75+
LINE CODE 2233 MILEPOST 26.6 TO 27.0 VAL SECTION 7415

BLOCK HOUSE RUN I.T.
FROM STA. 1372+00.00 TO STA. 1425+00.00
LINE CODE 2244 MILEPOST 0.7 TO 0.0 VAL SECTION 7338

RECORD MAP REFERENCE RM 24248/C127 A110s w2 Maps 16-
FILENAME 220202600
ADMINISTRATIVE SERVICES PHILADELPHIA, PA.
08-26-1992

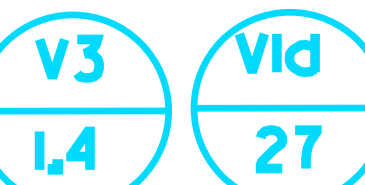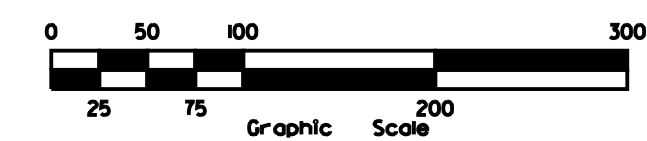

TOWNSHIP OF ROCHESTER
BOROUGH OF NEW BRIGHTON
COUNTY OF BEAVER
COMMONWEALTH OF PENNSYLVANIA

 

NOTE: SEE ROLL MAP C127 FOR STATE APPROPRIATION FOR CONSTRUCTION OF STATE ROUTE #65

NOTE: THE TRACK CONFIGURATION AS SHOWN IS FOR HISTORICAL REFERENCE ONLY. IT IS NOT INTENDED TO REPRESENT CONRAIL'S CURRENT TRACK CONFIGURATION.



THE CENTERLINE GEOMETRY AND PROPERTY/PARCEL LINE INFORMATION DEPICTED ON THIS MAP IS BASED ON A COMPILED OF VARIOUS HISTORICAL SOURCES OF REAL PROPERTY INFORMATION WITHIN CONRAIL. WHILE EVERY EFFORT GOES INTO PRODUCING AN ACCURATE RECORD MAP, IT IS NOT BASED ON A CURRENT GROUND SURVEY, AND ACCORDINGLY, IS NOT DISTRIBUTED FOR CERTIFICATION PURPOSES.

These maps were not prepared or intended for use as a real estate title map. The railway company does not represent or suggest that the property lines and right-of-way lines shown on the maps are accurate, or that the maps are correct. The company does not represent that it has checked this map for accuracy.

CONRAIL
RIGHT OF WAY MAP
TOWNSHIP OF ROCHESTER
PITTSBURGH, FORT WAYNE & CHICAGO RAILWAY
FORT WAYNE LINE
FROM STA. 1425+60.00 TO STA. 1478+40.00
LINE CODE 2202 MILEPOST 27.0 TO 28.0 VAL SECTION 7338
BLOCK HOUSE RUN I.T.
FROM STA. 1425+60.00 TO STA. 1478+40.00
LINE CODE 221f MILEPOST 0.0 TO 1.0 VAL SECTION 7338
RECORD MAP REFERENCE RM24248C127 A110s w2Map 17818
FILENAME 220202700
ADMINISTRATIVE SERVICES PHILADELPHIA, PA.
09-03-1992

0 50 100 200 300
25 75 150 225 300
Graphic Scale (feet)

VID
PENNA.
28

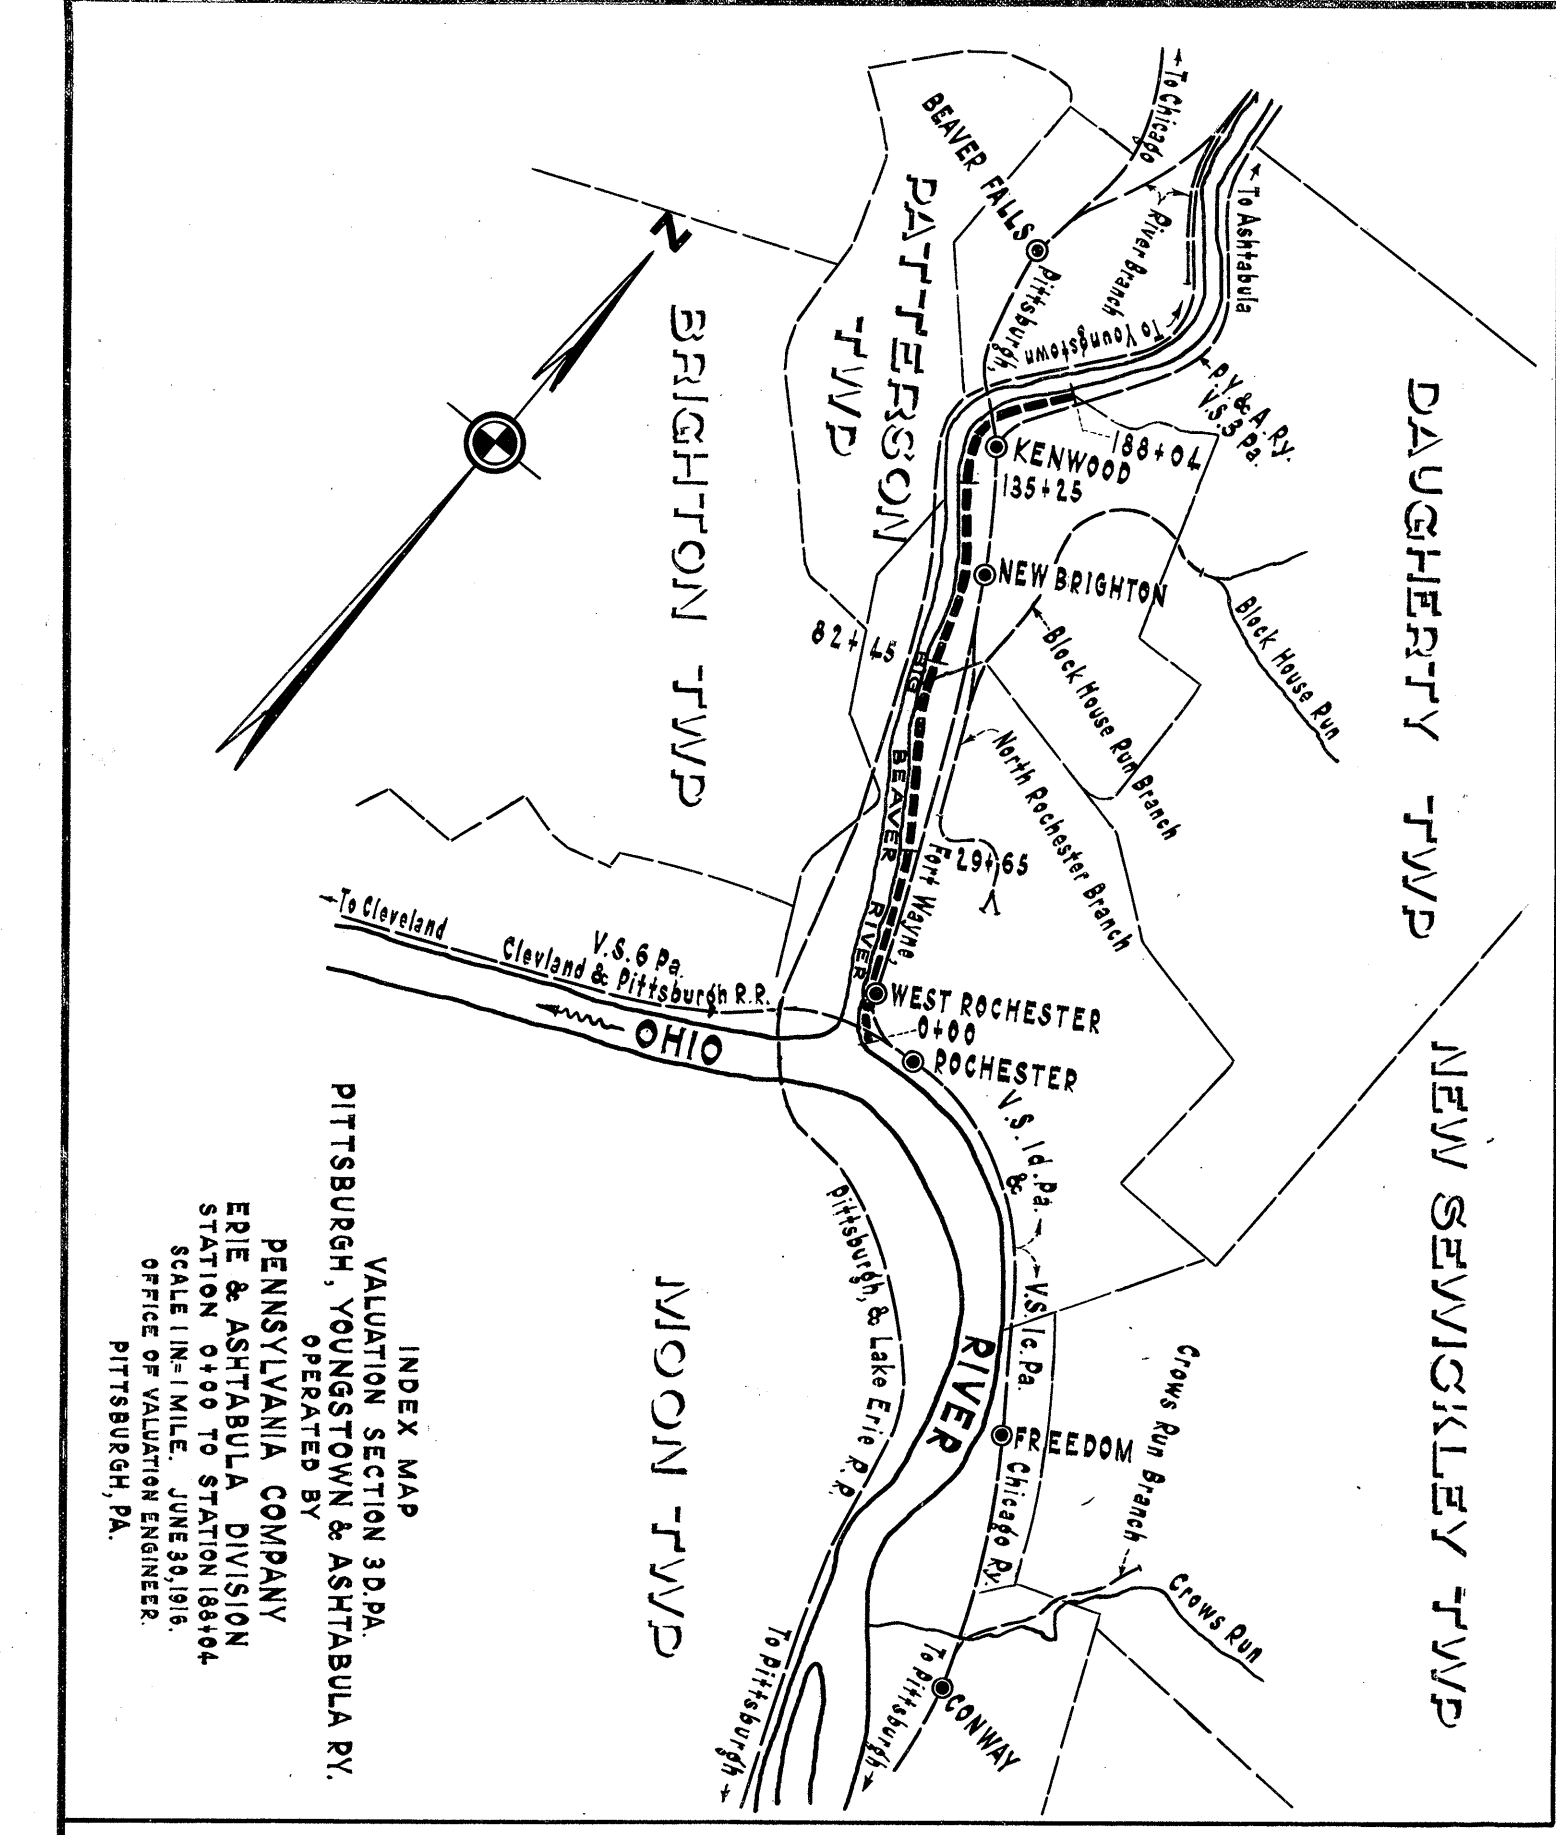 

2202005
223004

INDEX MAP
VALUATION SECTION 32A
PITTSBURGH, YOUNGSTOWN & ASHTABULA RY.
ERIE & ASHTABULA DIVISION
STATION 5140 TO STATION 18144
OFFICE OF VALUATION ENGINEERS
PITTSBURGH, PA.


1988+22+1956+64.47 Sketch
showing Division of Ownership
of Facilities. 6-20-90 Valuation
Engineers File.

PY & A.Ry. 1998+22+
R.F.W. & C.Ry. 1905+68

These maps were not prepared
or intended for use as a real
estate title map. The railway
company does not represent or
suggest that the property lines
and right-of-way lines shown on
the maps are correct, or that
the maps are correct. The
company does not represent
that it has checked this map for
accuracy.

CONTRACT NO. OR REF. NO.	REVISION NO.	REVISION DATE
1	1	1987
2	2	1988
3	3	1989
410	410	2396
411		

To Chicago

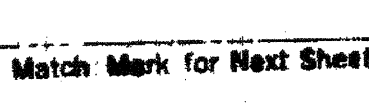

RIGHT OF WAY & TRACK MAP
PITTSBURGH, YOUNGSTOWN & ASHTABULA R.R.
OPERATED BY
PENNSYLVANIA COMPANY
ERIE & ASHTABULA DIVISION
STATION 22+65' TO STATION 32+4.5'
SCALE: 1 IN. = 100' JUNE 30 1916