
 


TOWN OF BADEN
BEAVER COUNTY
PENNSYLVANIA

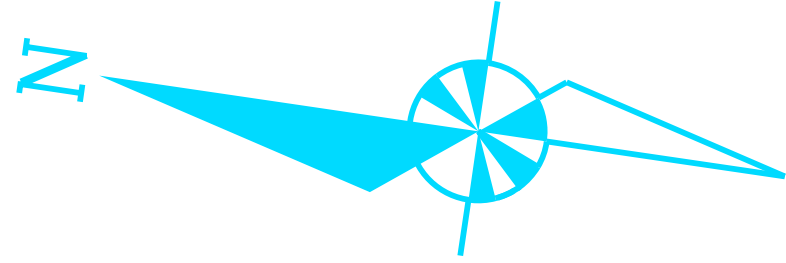

DISCLAIMER:
NORFOLK SOUTHERN RAILWAY COMPANY AND ITS PARENT(S), SUBSIDIARIES AND AFFILIATES (EACH A "NS ENTITY" AND ALL SUCH ENTITIES TOGETHER BEING "NS ENTITIES"), AND ITS AND THEIR RESPECTIVE OFFICERS, DIRECTORS, EMPLOYEES, AGENTS AND CONTRACTORS (ALL SAID PARTIES TOGETHER BEING THE "NS PARTIES"), MAKE NO WARRANTY OF ANY KIND, EXPRESS OR IMPLIED, INCLUDING WITHOUT LIMITATION ANY WARRANTY OF MERCHANTABILITY OR WARRANTY FOR FITNESS OF USE FOR A PARTICULAR PURPOSE, WITH RESPECT TO THE INFORMATION CONTAINED ON THIS MAP (THE "INFORMATION"). ANY USER OF THE INFORMATION (THE "USER") ACCEPTS THE INFORMATION "AS IS, WITH ALL FAULTS," AND THE USER (1) ASSUMES ALL RESPONSIBILITY FOR THE USE THEREOF AND (2) FURTHER COVENANTS AND AGREES TO DEFEND, INDEMNIFY AND HOLD HARMLESS THE NS PARTIES FROM AND AGAINST ANY INJURY, DAMAGE, LOSS OR LIABILITY WHATSOEVER ARISING FROM ANY USE OF THE INFORMATION, REGARDLESS OF CAUSE. THE NS PARTIES DISCLAIM AND THE NS PARTIES SHALL NOT BE HELD LIABLE FOR, ANY AND ALL INJURIES, DAMAGES, LOSS OR LIABILITY, WHETHER DIRECT, INDIRECT, INCIDENTAL OR CONSEQUENTIAL WHICH ARISE OR MAY ARISE FROM THIS MAP THE INFORMATION OR THE USE THEREOF BY ANY PERSON OR ENTITY, REGARDLESS OF CAUSE.
THE USER SHOULD OBTAIN INDEPENDENT VERIFICATION OF ALL INFORMATION CONTAINED ON THIS MAP.
Possession of this map conveys no right of permission to enter or occupy property of any NS Entity. Permission for entry, if a given NS Entity decides, at its sole election, to grant it, must be obtained through the usual and customary procedures that such NS Entity has established for access to its property.

OHIO RIVER

NOTE: THE TRACK CONFIGURATION AS SHOWN IS FOR HISTORICAL REFERENCE ONLY. IT IS NOT INTENDED TO REPRESENT CONRAIL'S CURRENT TRACK CONFIGURATION.
THE CENTERLINE GEOMETRY AND PROPERTY/PARCEL LINE INFORMATION DEPICTED ON THIS MAP IS BASED ON A COMPILED OF VARIOUS HISTORICAL SOURCES OF REAL PROPERTY INFORMATION WITHIN CONRAIL. WHILE EVERY EFFORT GOES INTO PRODUCING AN ACCURATE RECORD MAP, IT IS NOT BASED ON A CURRENT GROUND SURVEY, AND ACCORDINGLY, IS NOT DISTRIBUTED FOR CERTIFICATION PURPOSES.

CONRAIL
RIGHT OF WAY MAP
PITTSBURGH, FORT WAYNE & CHICAGO RAILWAY
FORT WAYNE LINE
FROM STA. 1056+00 TO STA. 1108+00
LINE CODE 2202 MILEPOST 20.0 TO 21.0 VAL SECTION 7336
ECONOMY IND. TRK. EXT.
FROM STA. 1056+00 TO STA. 1108+00
LINE CODE 220d MILEPOST 2.4 TO 2.9 VAL SECTION 7336
RECORD MAP REFERENCE ATLAS * 2 PAGES 5.6 & 7
FILENAME 220202000
ADMINISTRATIVE SERVICES PHILADELPHIA, PA.
08-15-1992

