


CITY OF ROCHESTER
TOWN OF EAST ROCHESTER
COUNTY OF BEAVER
COMMONWEALTH OF PENNSYLVANIA



DISCLAIMER:
NORFOLK SOUTHERN RAILWAY COMPANY, ITS EMPLOYEES, AGENTS AND PERSONNEL, MAKES NO WARRANTY OF MERCHANTABILITY OR WARRANTY FOR FITNESS OF USE FOR A PARTICULAR PURPOSE, EXPRESS OR IMPLIED WITH RESPECT TO THE INFORMATION CONTAINED ON THIS MAP. ANY USER OF THIS INFORMATION ACCEPTS THE SAME AS IS, WITH ALL FAULTS, AND ASSUMES ALL RESPONSIBILITY FOR THE USE THEREOF, AND FURTHER COVENANTS AND AGREES TO HOLD NORFOLK SOUTHERN RAILWAY COMPANY, ITS EMPLOYEES, AGENTS, AND PERSONNEL, HARMLESS FROM AND AGAINST ANY DAMAGE, LOSS OR LIABILITY ARISING FROM ANY USE OF THE INFORMATION.
ANY USER SHOULD OBTAIN INDEPENDENT VERIFICATION OF ALL INFORMATION CONTAINED ON THIS MAP.
NORFOLK SOUTHERN RAILWAY COMPANY, ITS EMPLOYEES, AGENTS, AND PERSONNEL, DISCLAIMS AND SHALL NOT BE HELD LIABLE FOR, ANY AND ALL DAMAGES, LOSS OR LIABILITY, WHETHER DIRECT, INDIRECT OR CONSEQUENTIAL WHICH ARISES OR MAY ARISE FROM THIS MAP INFORMATION OR USE THEREOF BY ANY PERSON OR ENTITY.
Possession of this map conveys no right of permission to enter or occupy Railroad property. Permission for entry, if Norfolk Southern chooses to grant it, must be obtained through the usual and customary procedures that the Railroad has established for access to Railroad property.

NOTE: THE TRACK CONFIGURATION AS SHOWN IS FOR HISTORICAL REFERENCE ONLY. IT IS NOT INTENDED TO REPRESENT CONRAIL'S CURRENT TRACK CONFIGURATION.

THE CENTERLINE GEOMETRY AND PROPERTY/PARCEL LINE INFORMATION DEPICTED ON THIS MAP IS BASED ON A COMPILED OF VARIOUS HISTORICAL SOURCES OF REAL PROPERTY INFORMATION WITHIN CONRAIL. WHILE EVERY EFFORT GOES INTO PRODUCING AN ACCURATE RECORD MAP, IT IS NOT BASED ON A CURRENT GROUND SURVEY, AND ACCORDINGLY, IS NOT DISTRIBUTED FOR CERTIFICATION PURPOSES.

CONRAIL
RIGHT OF WAY MAP
FORMERLY
PITTSBURGH, FORT WAYNE & CHICAGO RAILWAY
FORT WAYNE LINE
FROM STA. 1320+00 TO STA. 1372+00
LINE CODE 2202 MILEPOST 25.0 TO 26.0 VAL SECTION 7338
RECORD MAP REFERENCE ATLAS 2W PGS. 12,13,14 RM W-5564
FILENAME 220202500
ADMINISTRATIVE SERVICES PHILADELPHIA, PA.
09-17-1992

0 50 100 200 300
25 75 150 200
Graphic Scale (feet)

V1d
PENNA
26