


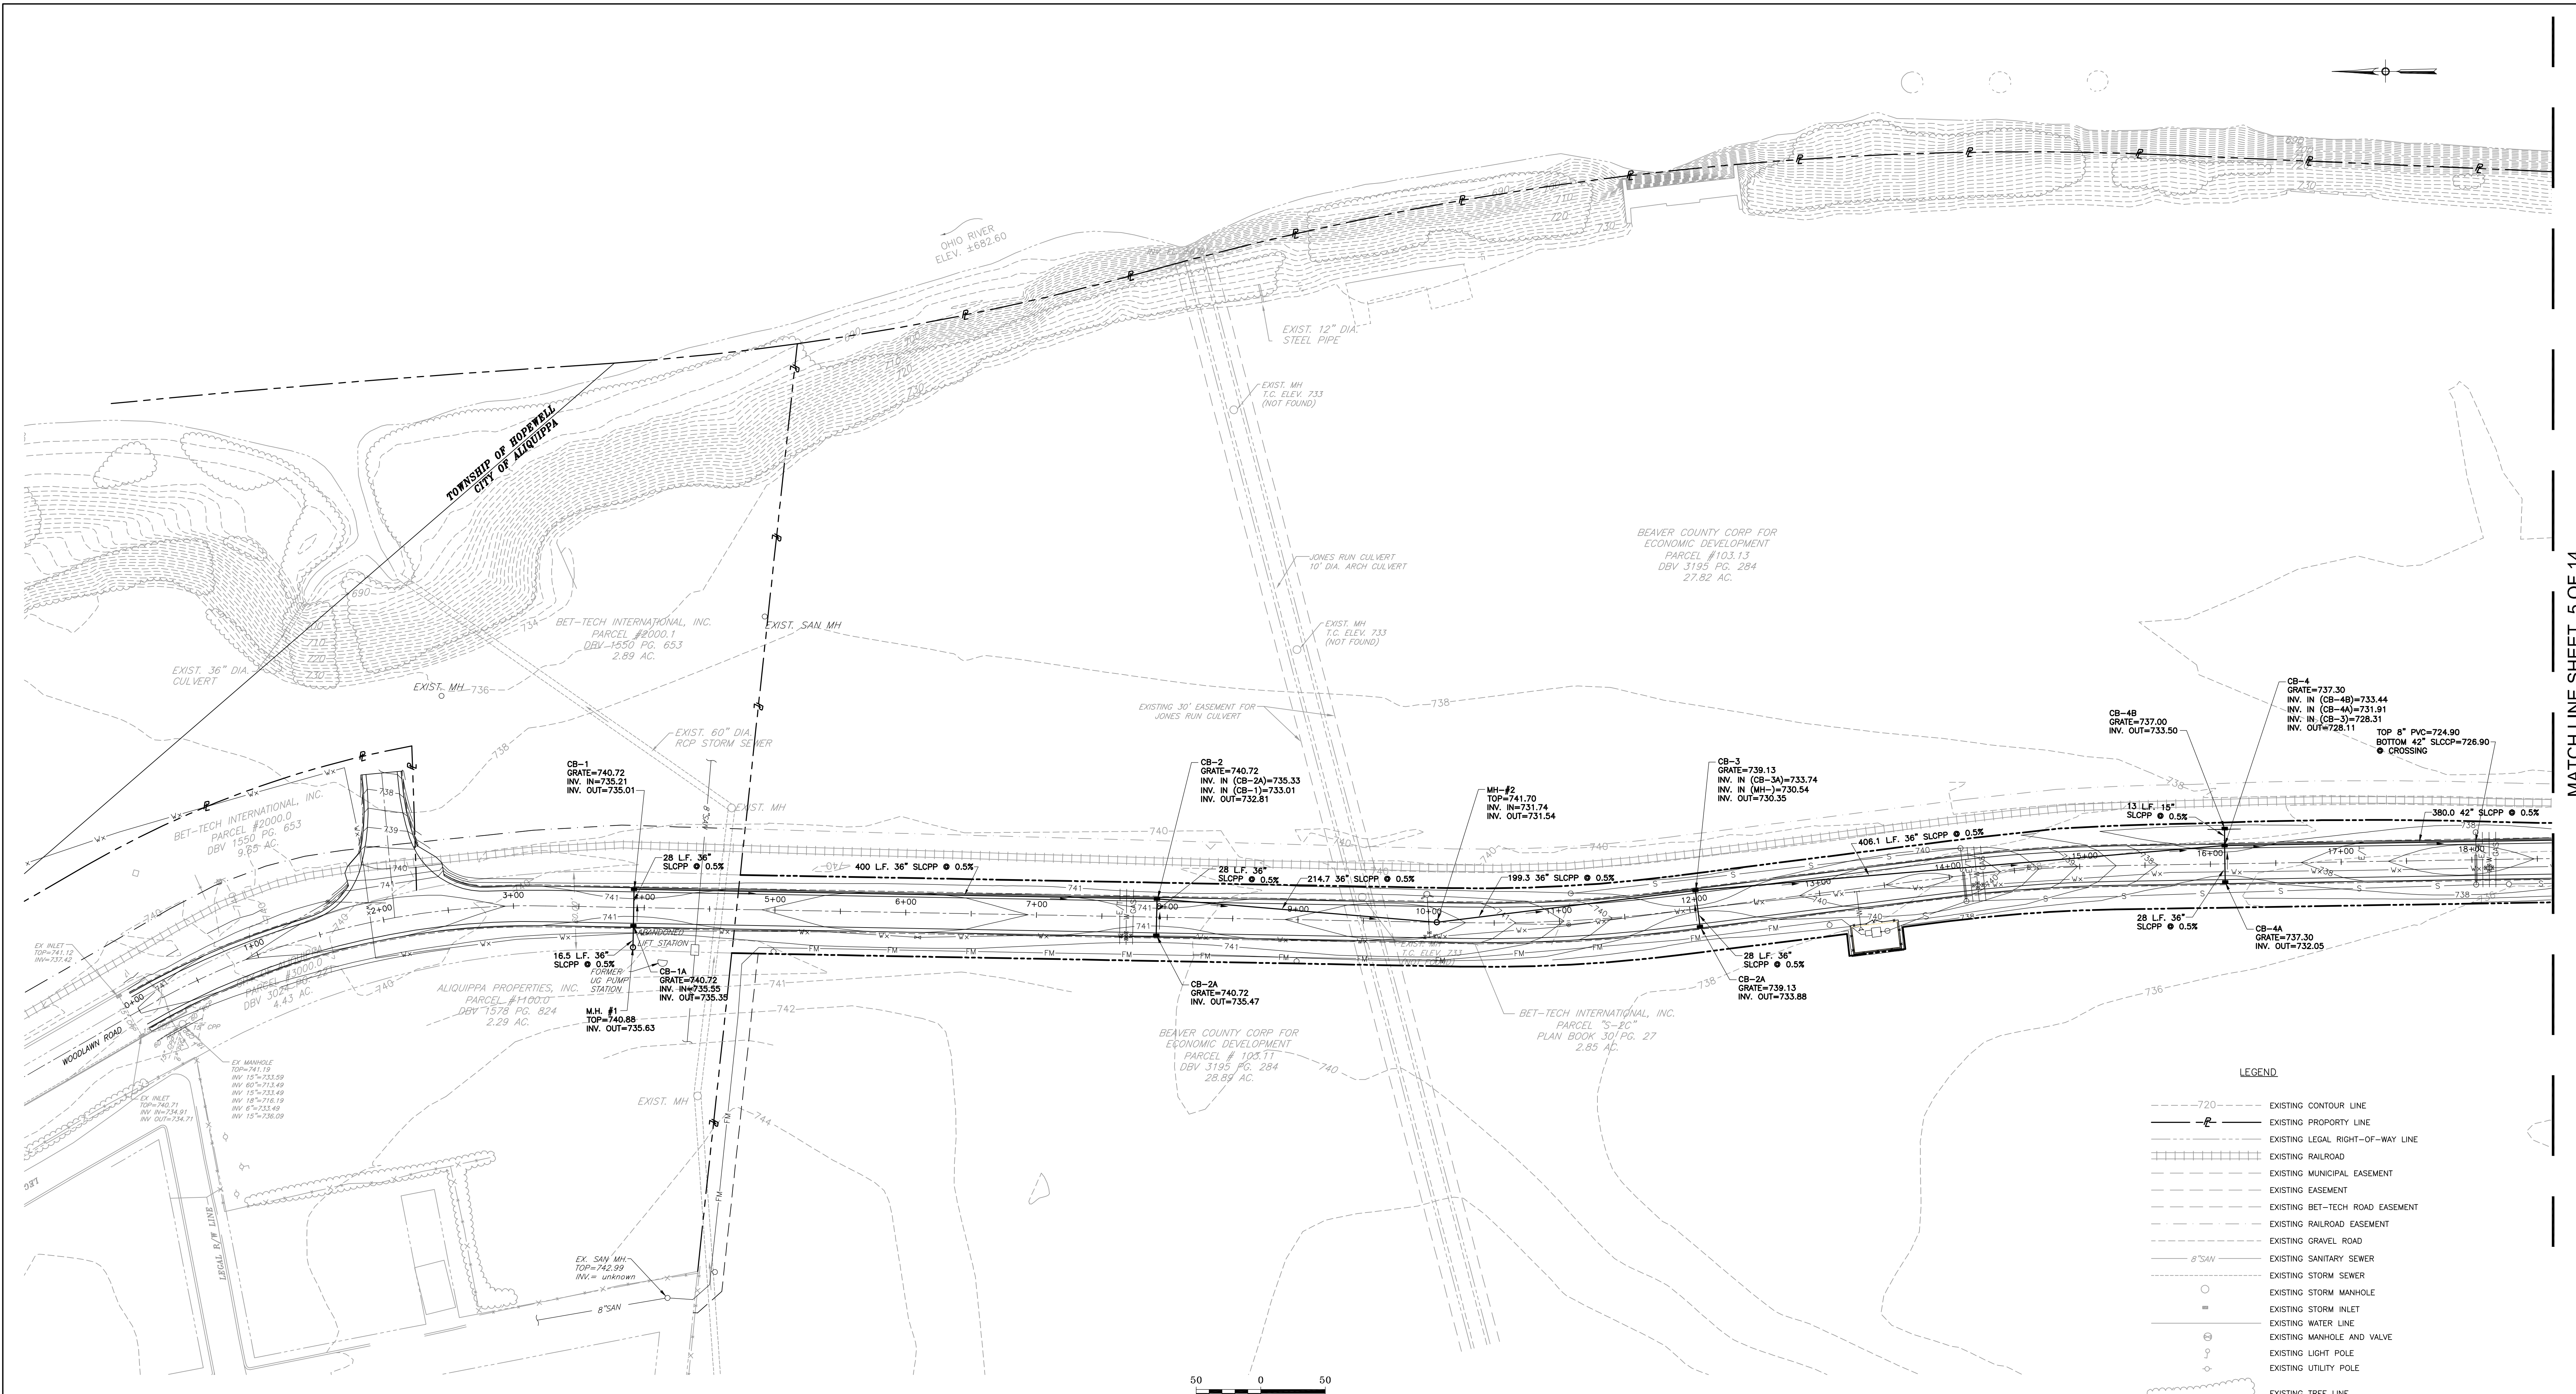

MATCH LINE SHEET 5 OF 14

STORM SEWER NOTES

1. THE CONTRACTOR SHALL OBTAIN ALL PERMITS WHICH MAY BE REQUIRED TO COMPLETE THE STORM SEWER.
2. THE CONTRACTOR SHALL CONFINE ALL WORK TO WITHIN THE DESIGNATED RIGHT-OF-WAY LIMITS FOR THE PROJECT. THE CONTRACTOR WILL BE RESPONSIBLE FOR DAMAGES RESULTING FROM OPERATIONS CARRIED OUT IN LOCATIONS OUTSIDE OF THE WORK AREA.
3. INFORMATION REGARDING THE REPORTED PRESENCE, SIZE, CHARACTER, AND LOCATION OF EXISTING UNDERGROUND UTILITIES HAS BEEN SHOWN ON THE CONSTRUCTION DRAWINGS AND RECORDED AS SUCH IN GOOD FAITH. HOWEVER, THERE IS NO IMPLIED GUARANTEE OF THE ACCURACY OF THIS INFORMATION, AND IT HAS BEEN CONSIDERED BY THE CONTRACTOR IN THIS LIGHT, THE CONTRACTOR RECOGNIZES THAT THE LOCATION OF THE UNDERGROUND STRUCTURES SHOWN MAY BE INACCURATE AND OBSTRUCTIONS OTHER THAN THOSE SHOWN MAY BE ENCOUNTERED IN THE WORK. THE CONTRACTOR HEREBY DISTINCTLY AGREES THAT THE ENGINEER IS NOT RESPONSIBLE FOR THE CORRECTNESS OR SUFFICIENCY OF THE INFORMATION GIVEN.
4. TRENCH BACKFILL MUST BE PROVIDED PER PROJECT SPECIFICATIONS AND TRENCHING DETAILS.

UTILITY COMPANIES:

CITY OF ALIQUIPPA
581 FRANKLIN AVE.
ALIQUIPPA, PA 15001
724-375-5188
ADMINISTRATION OFFICE /
DEPARTMENT OF PUBLIC WORKS

**MUNICIPAL WATER AUTHORITY
OF ALIQUIPPA (MW&A)**
160 HOPWELL AVENUE
ALIQUIPPA, PA 15001
724-375-5525
ATTN: MR. ALONZO ELLIS

COLUMBIA GAS OF PA
1600 DUBLIN ROAD
COLUMBUS, OH 43215
1-800-440-6111
ATTN: MS. SHARON BELL

DOMINION PEOPLES GAS CO.
5600 COMMUNITY CENTER DRIVE
GIBSONIA, PA 15044
ATTN: MR. LEO FREISMUTH
(NO FACILITIES NEAR SITE)

DUQUESNE LIGHT COMPANY
214 MEADOWLARK LANE #3
ALIQUIPPA, PA 15001
412-393-2309
ATTN: MR. JOE CORNIBE

VERIZON COMMUNICATIONS
2202 WEST STATE STREET
NEW CASTLE, PA 16101
724-656-5230
ATTN: MS. KAREN MCBETH

THE OHIO CENTRAL RAILROAD
47849 PAPERMILL ROAD
COSHOCTON, OH 43812
740-622-8092
ATTN: MR. CHRIS LAYMAN
AND MR. JOHN CORNS

CALL BEFORE YOU DIG!
PENNSYLVANIA LAW REQUIRES
3 WORKING DAYS NOTICE FOR
CONSTRUCTION PHASE AND 10 WORKING
DAYS IN DESIGN STAGE - STOP CALL
Pennsylvania One Call System, Inc



1-800-242-1776

SERIAL NUMBER 0726107


REVISIONS	

DESIGNED	ELK
DRAWN	/DAB
CHECKED	MP
REVIEWED	
S.O.	109672 - task 5
CADD FILE	

THE BEAVER COUNTY CORPORATION FOR ECONOMIC DEVELOPMENT
250 INSURANCE STREET - SUITE 300 - BEAVER, PA 15009
PHONE: 724-728-8610 - FAX: 724-728-3666

MICHAEL BAKER JR., INC.
A unit of Michael Baker Corporation
4301 Dutch Ridge Road
BEAVER, PENNSYLVANIA 15009

CONSULTING ENGINEERS
(724) 495-7711

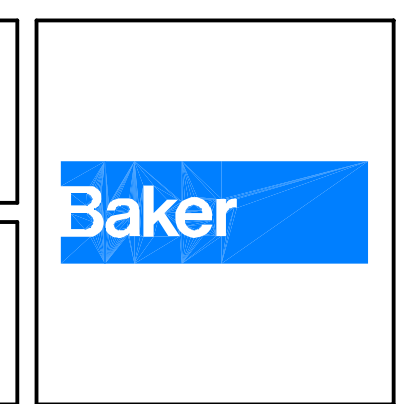

**WOODLAWN ROAD AND
SANITARY SEWER EXTENSIONS
STORM SEWER PLAN
(NORTH)**

SCALE: AS NOTED

DATE: APRIL 26, 2011

SHEET NO.
4
OF 14