


Typical Bike Lane Signage

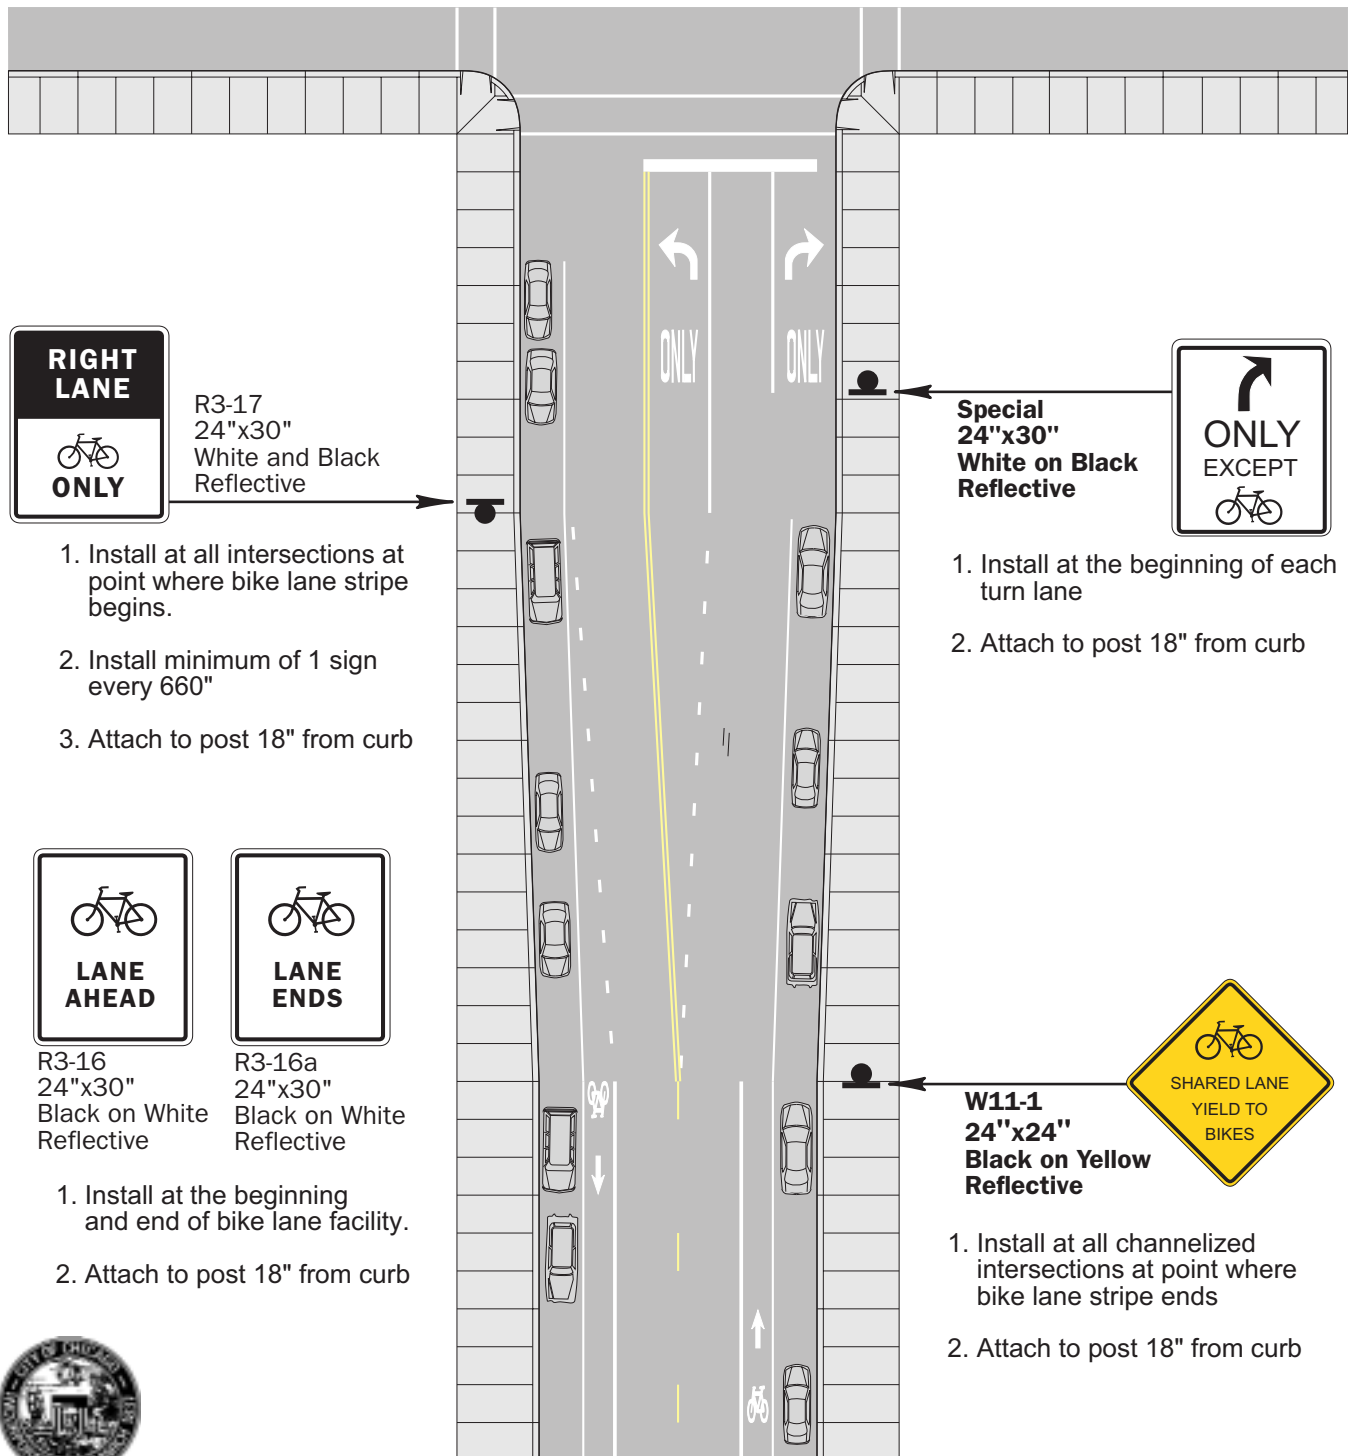

City of Chicago
Richard M. Daley, Mayor
DEPARTMENT OF TRANSPORTATION
Miguel d'Escoto, Commissioner
BUREAU OF TRAFFIC
Donald Grabowski, Deputy Commissioner

C I T Y O F C H I C A G O

Typical Bike Lane Signage

REVISED	5-16-02	SCALE	1"=30'
H:\Bike Lanes\Design Manual\Typical Signage			No. ___ of ___