



EXTERIOR

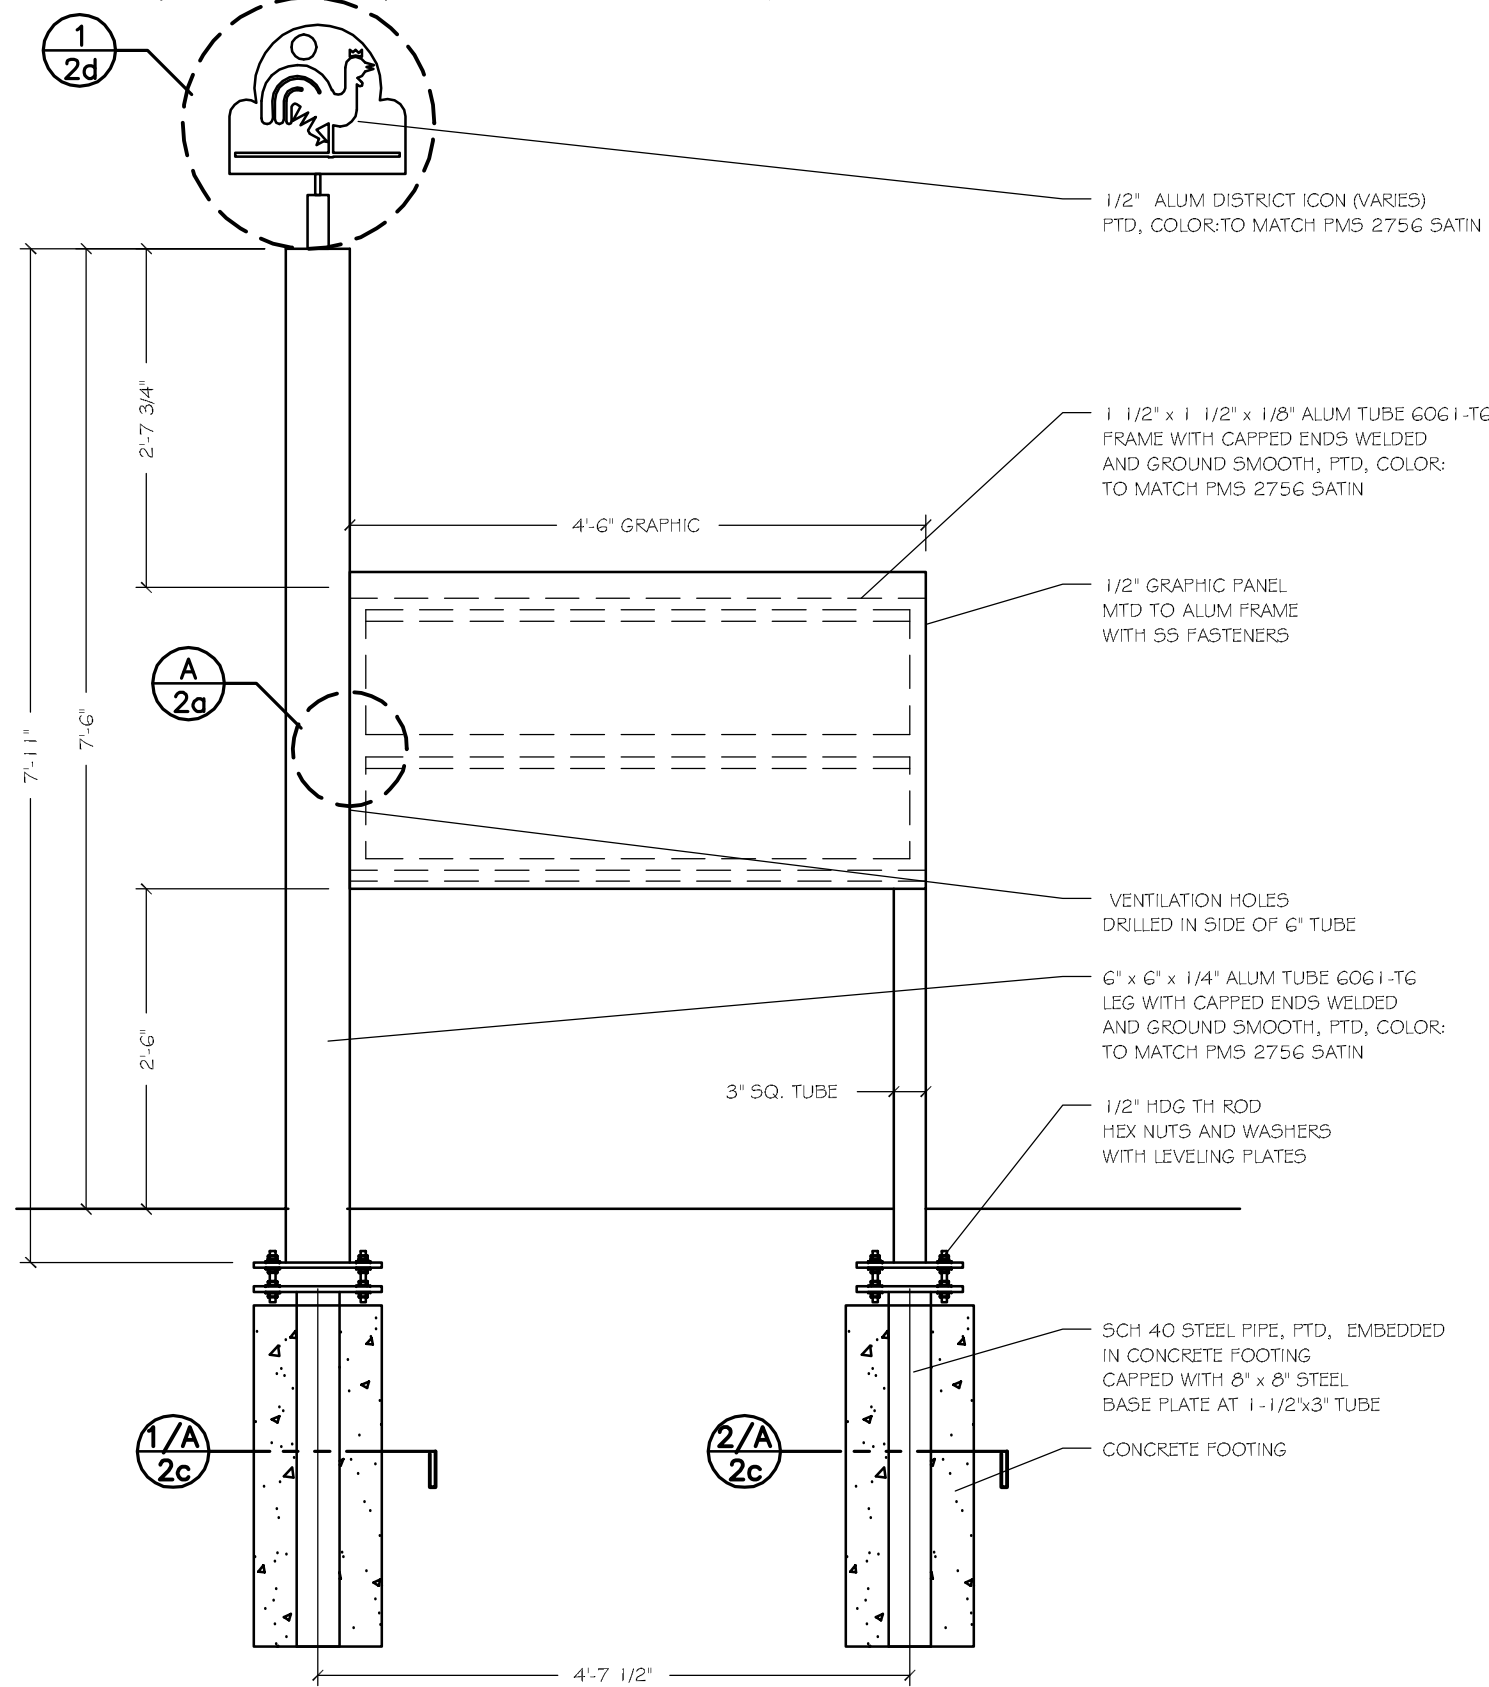

1 ELEVATION
3/4" = 1'-0"

QTY: 8

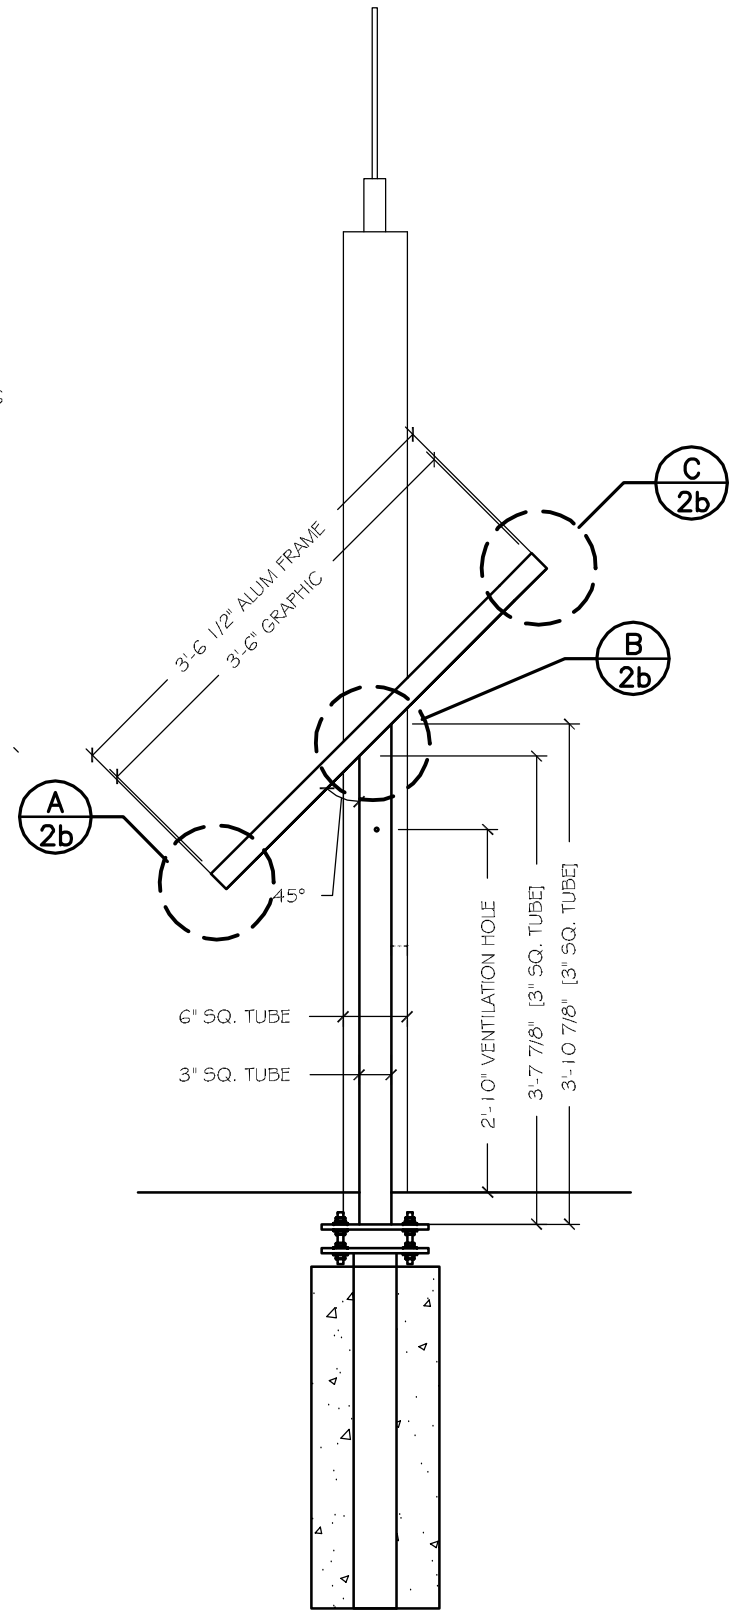

2 SIDE ELEVATION
3/4" = 1'-0"

CHECKED BY:

DRAWN BY:

FOR APPROVAL
16 AUG 04

FOR PRODUCTION
30 AUG 04


FOR PRODUCTION
06 JAN 05

WHEELING WAYSIDE


SIGN TYPE TILT

DESIGN COMMUNICATIONS LTD


617 542 9620 (951 0777 FAX) Boston Orlando 407 856 9661 (856 9617 FAX)

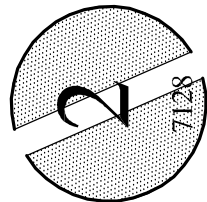

EXTERIOR

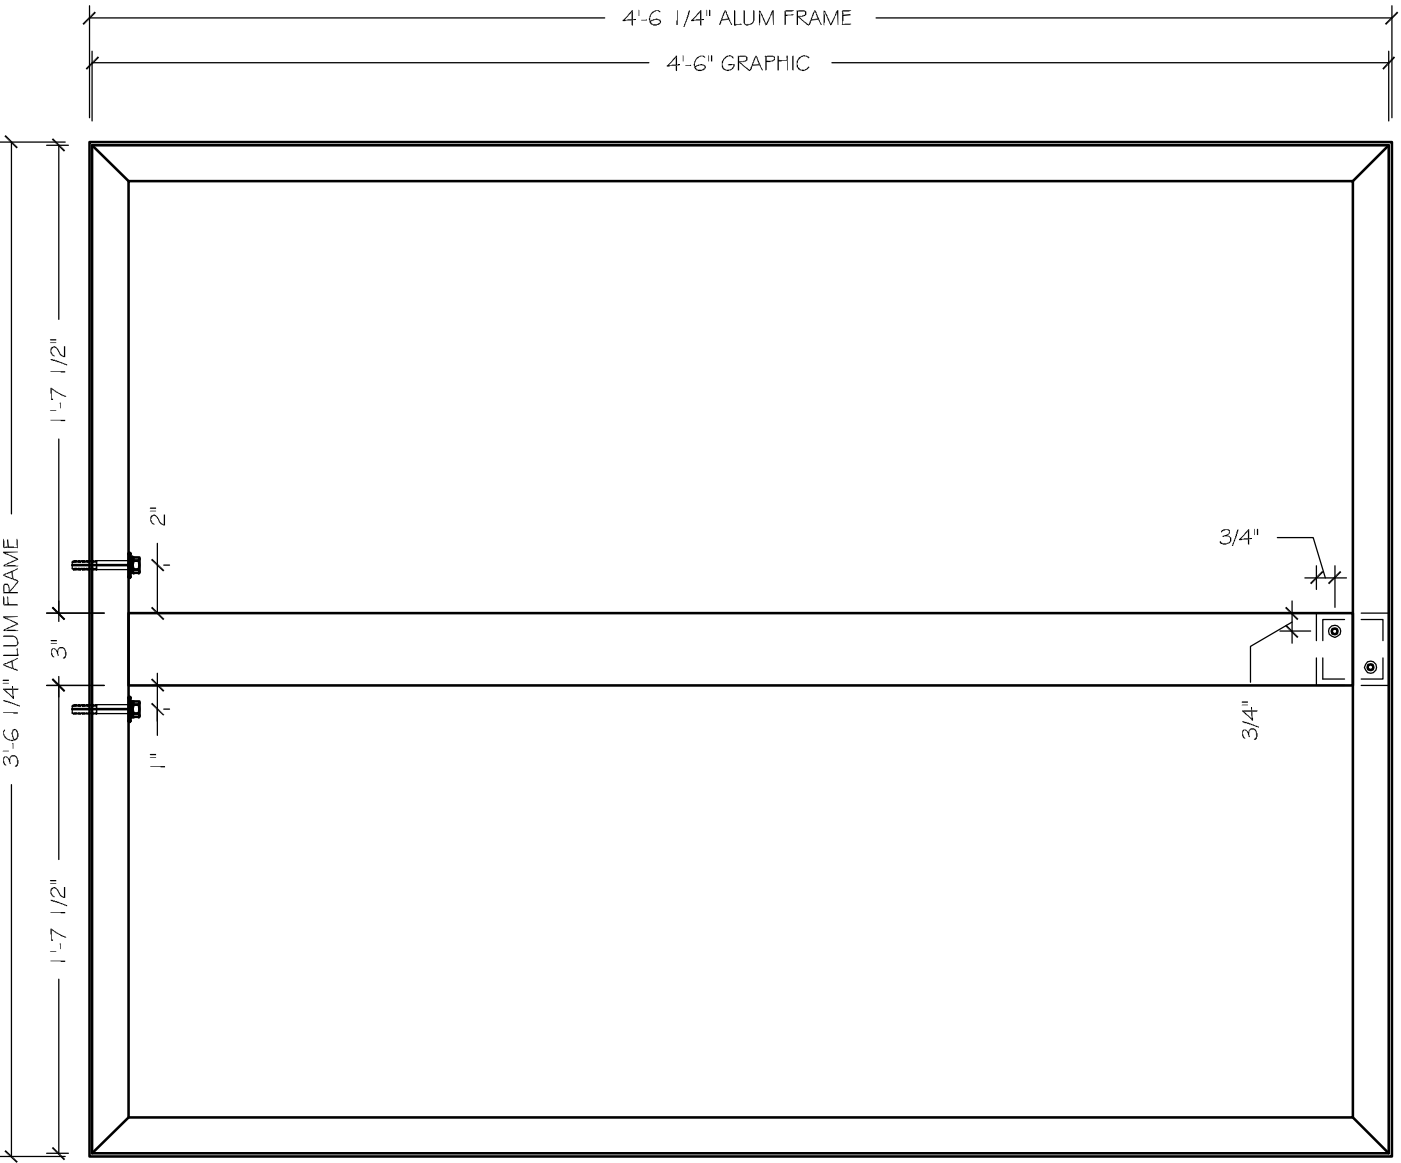

I DETAIL ELEVATION FRAME
1 1/2" = 1'-0"

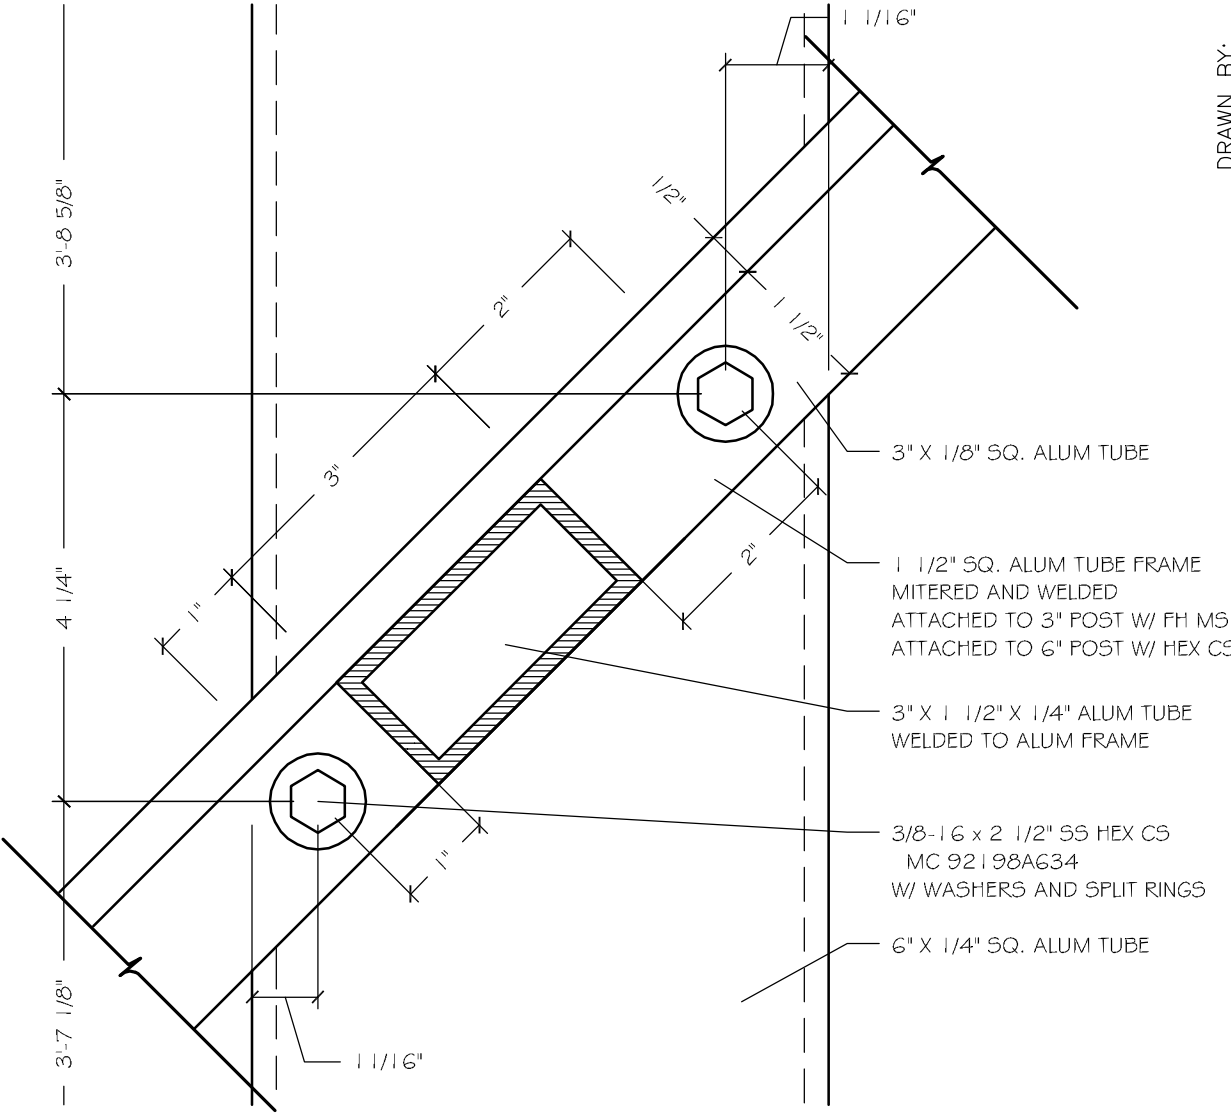

A DETAIL SECTION POST MOUNTING
HALF SIZE

DRAWN BY: CHECKED BY:

FOR APPROVAL
16 AUG 04


FOR PRODUCTION
30 AUG 04

FOR PRODUCTION
06 JAN 05

WHEELING WAYSIDE
SIGN TYPE TILT

DESIGN COMMUNICATIONS LTD

617 542 9620 (951 0777 FAX) Boston Orlando 407 856 9661 (856 9617 FAX)

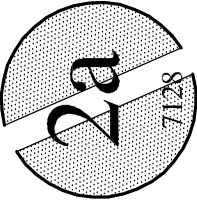

EXTERIOR


FOR APPROVAL
16 AUG 04

FOR PRODUCTION
30 AUG 04


FOR PRODUCTION
06 JAN 05

CHECKED BY:


DRAWN BY:

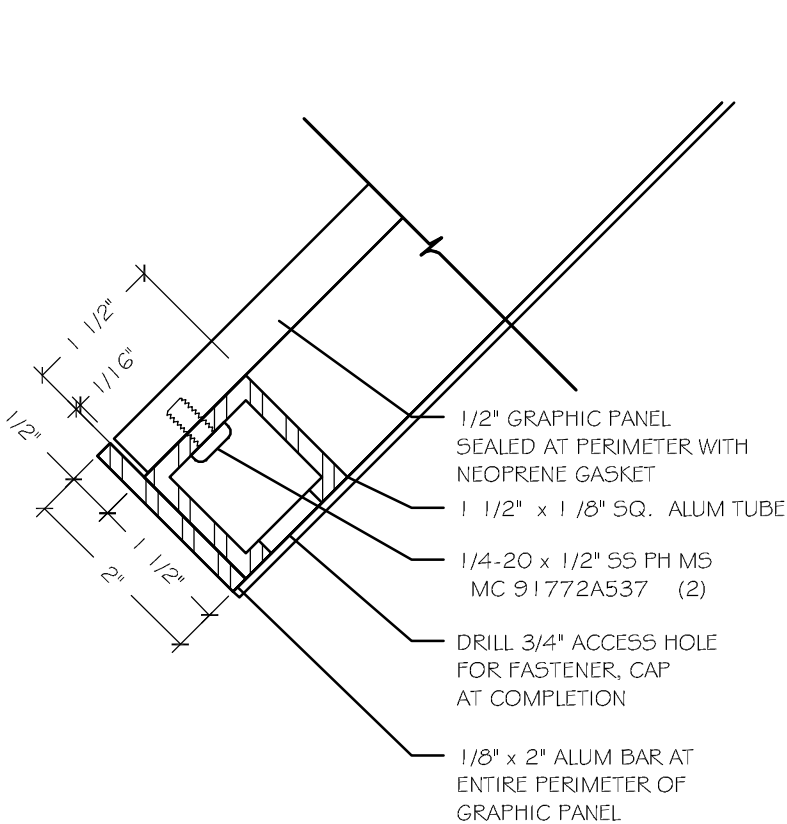

A DETAIL SECTION GRAPHIC PANEL
HALF SIZE

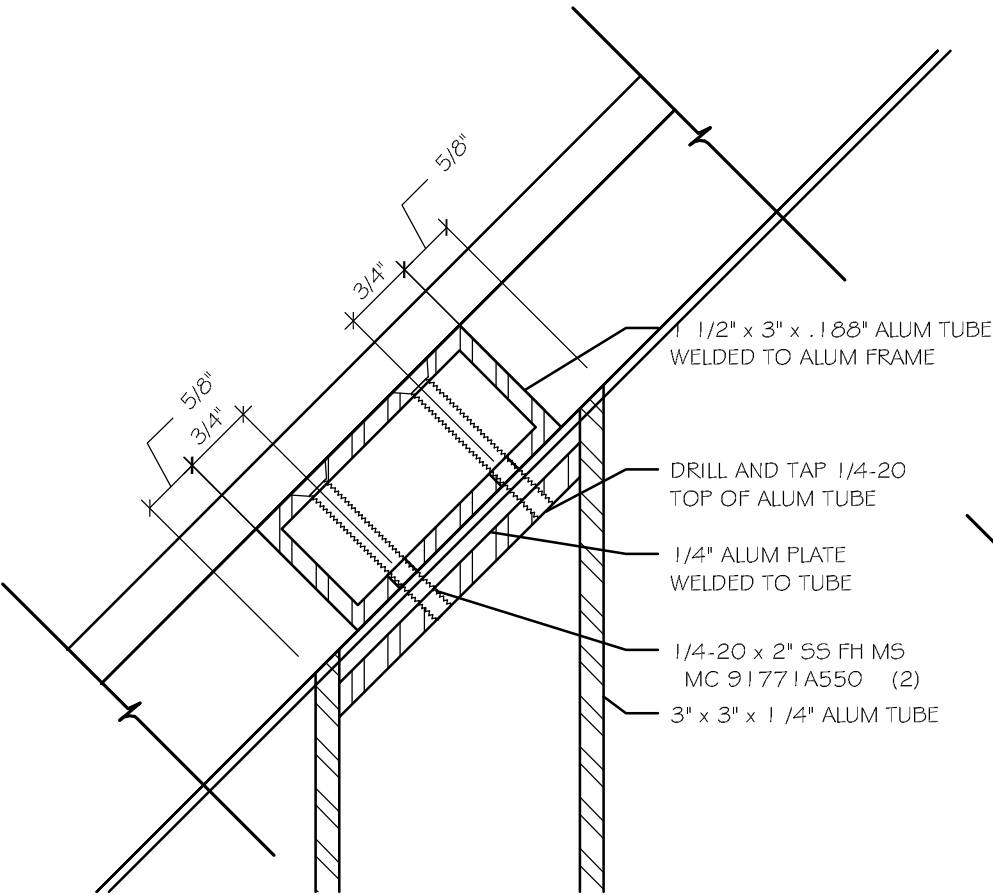

B DETAIL SECTION GRAPHIC PANEL
HALF SIZE

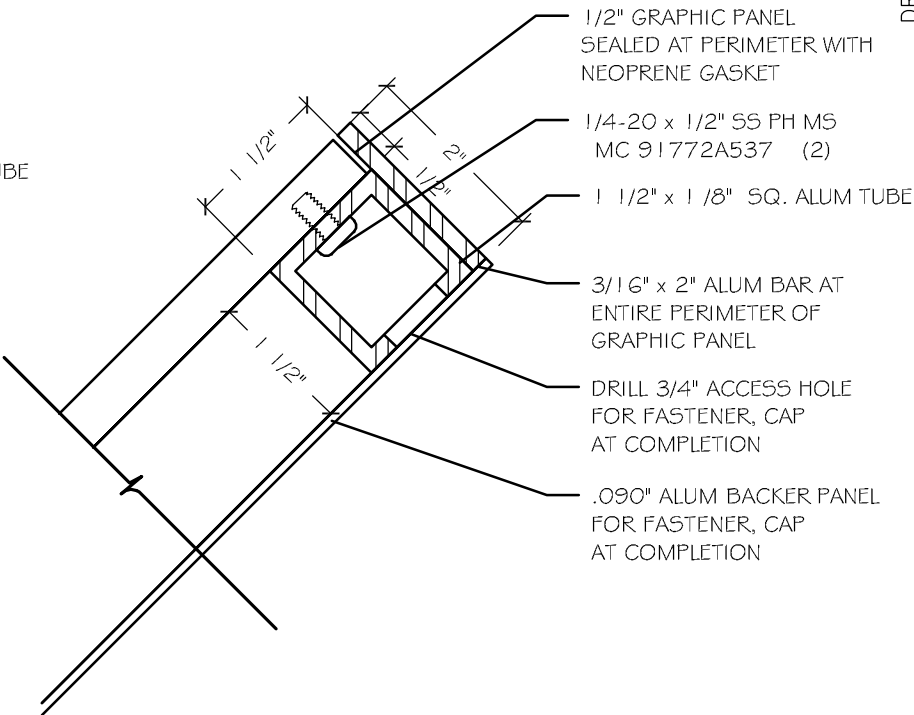


C DETAIL SECTION GRAPHIC PANEL
HALF SIZE


WHEELING WAYSIDE

SIGN TYPE TILT


DESIGN COMMUNICATIONS LTD

617 542 9620 (951 0777 FAX) Boston Orlando 407 856 9661 (856 9617 FAX)

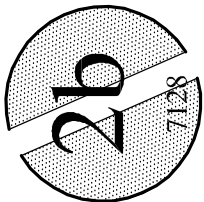


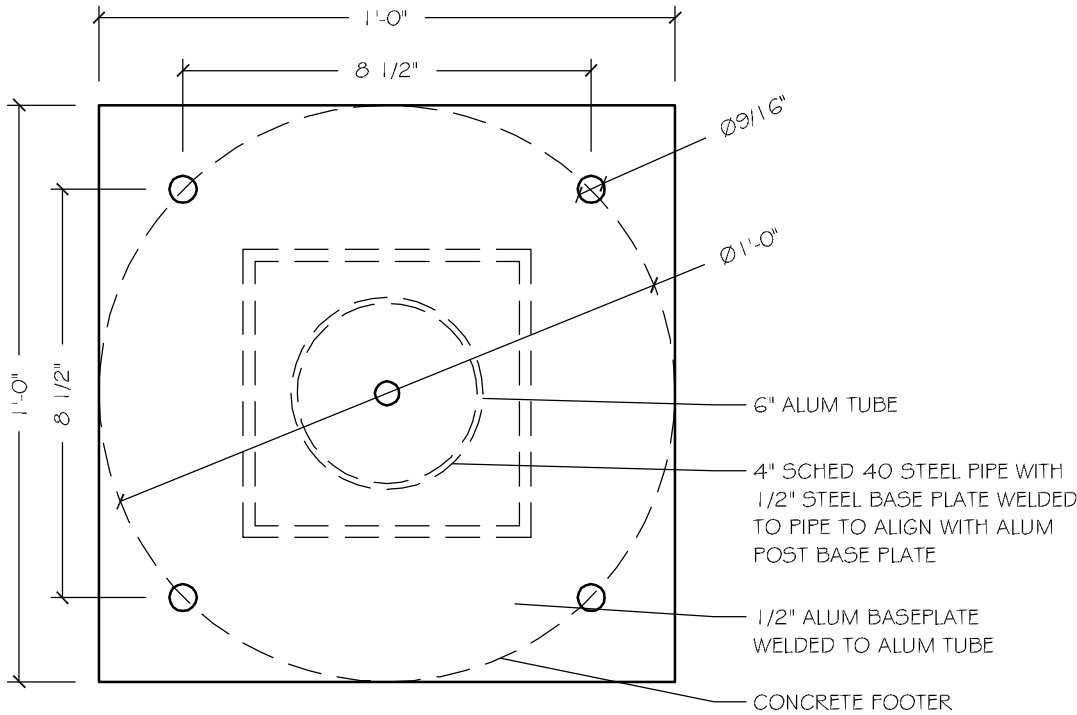


A DETAIL-BASE PLATE
3" = 1'-0"

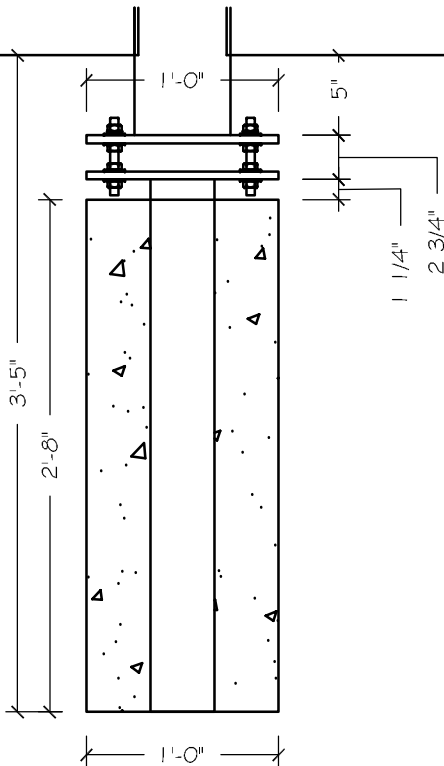

1 DETAIL CONCRETE FOOTER (6" POST)
1" = 1'-0"

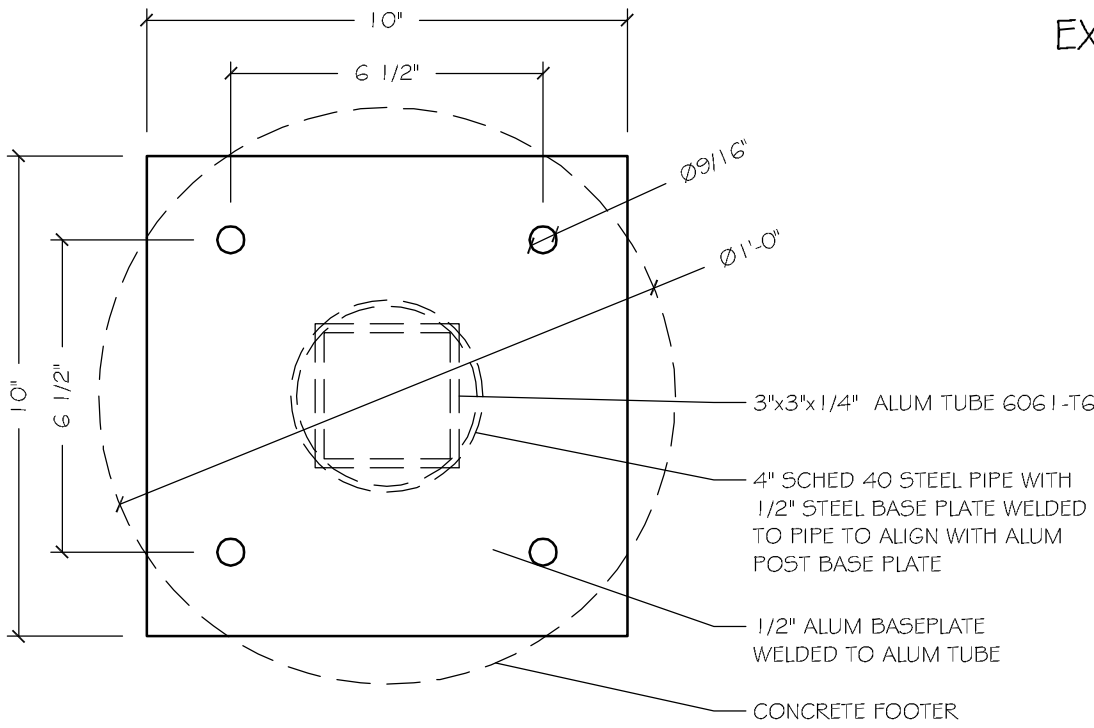

A DETAIL-BASE PLATE
3" = 1'-0"

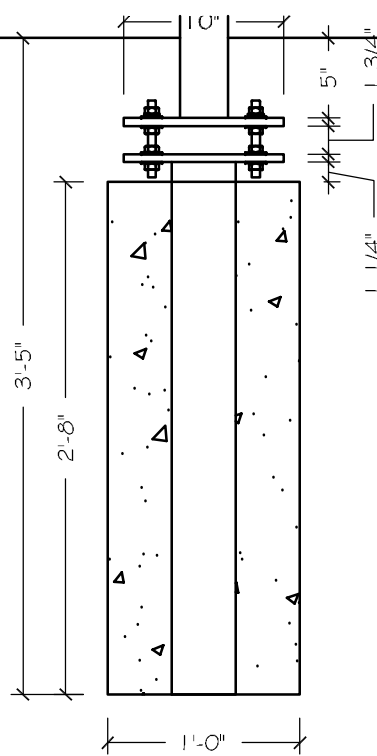

2 DETAIL CONCRETE FOOTER (3" POST)
1" = 1'-0"

EXTERIOR

CHECKED BY:

DRAWN BY:

FOR APPROVAL
16 AUG 04

FOR PRODUCTION
30 AUG 04


FOR PRODUCTION
06 JAN 05

WHEELING WAYSIDE


SIGN TYPE TILT

DESIGN COMMUNICATIONS LTD

617 542 9620 (951 0777 FAX) Boston Orlando 407 856 9661 (856 9617 FAX)

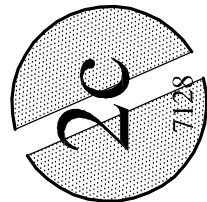

EXTERIOR

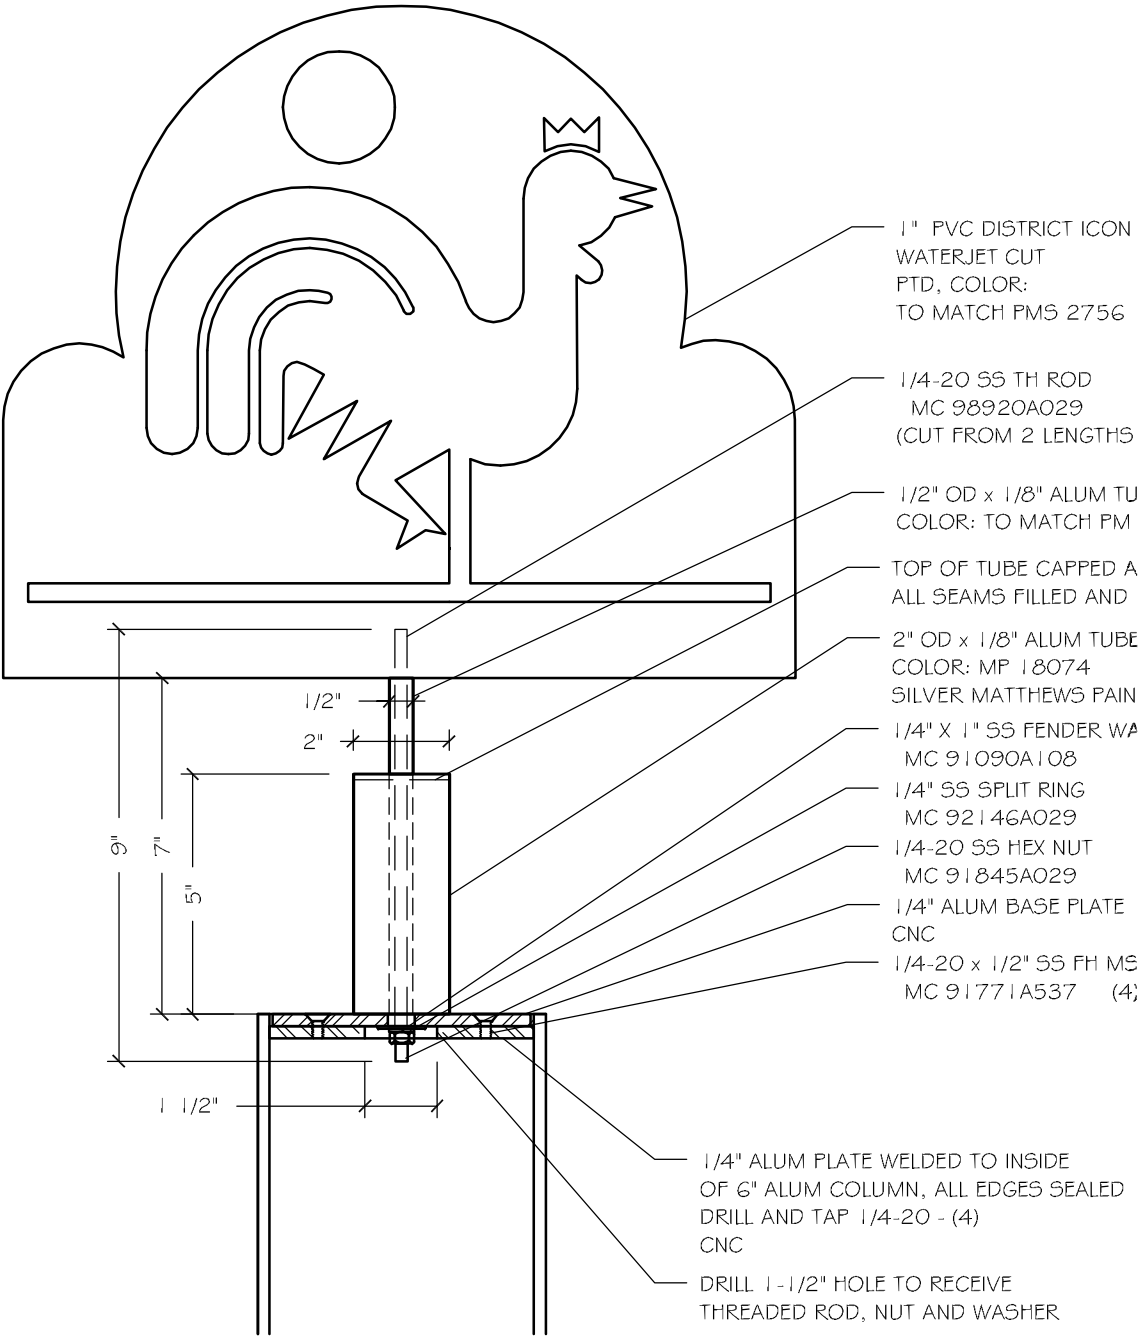

1
3" = 1'-0"

DETAIL ELEVATION ICON

DRAWN BY: CHECKED BY:

FOR APPROVAL
16 AUG 04

FOR PRODUCTION
30 AUG 04

FOR PRODUCTION
06 JAN 05

WHEELING WAYSIDE
SIGN TYPE TILT

DESIGN COMMUNICATIONS LTD
617 542 9620 (951 0777 FAX) Boston Orlando (856 9661 (856 9617 FAX)

