


EXTERIOR

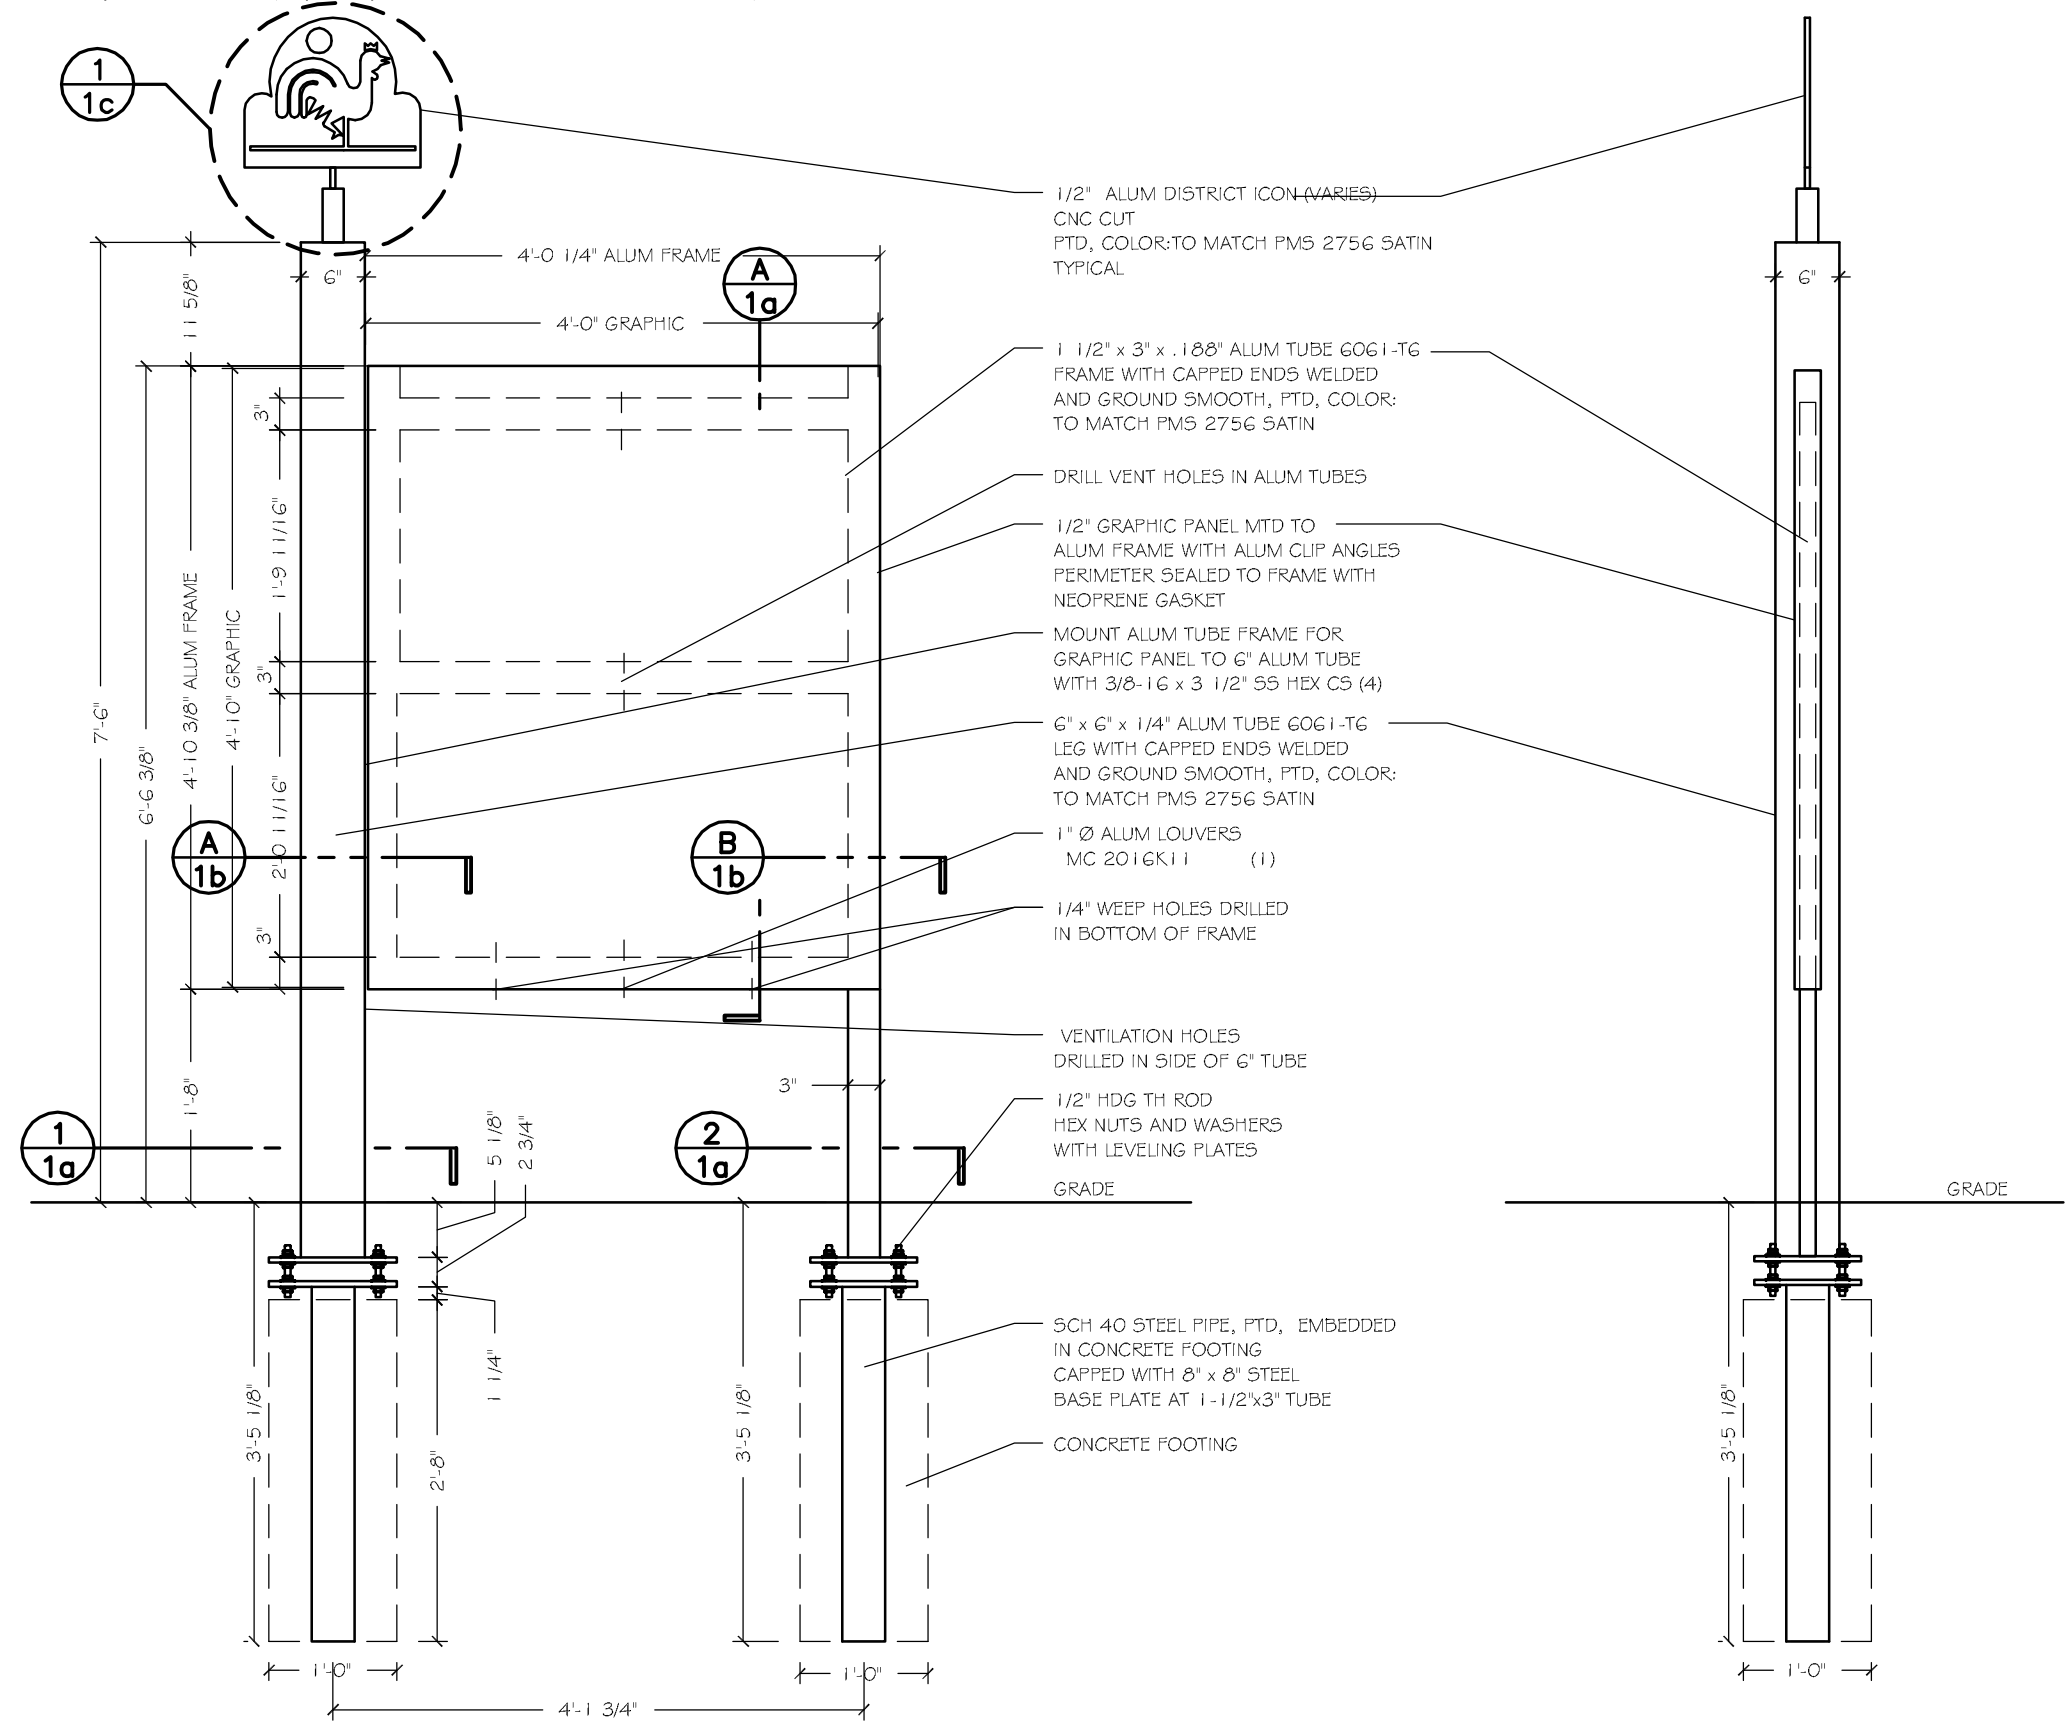

DRAWN BY: CHECKED BY:

FOR APPROVAL
16 AUG 04


FOR PRODUCTION
30 AUG 04



FOR PRODUCTION
06 JAN 05

WHEELING WAYSIDE
SIGN TYPE UPRIGHT


DESIGN COMMUNICATIONS LTD

617 542 9620 (951 0777 FAX) Boston Orlando 407 856 9661 (856 9617 FAX)

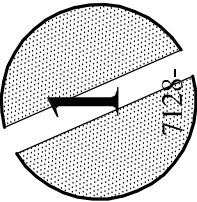


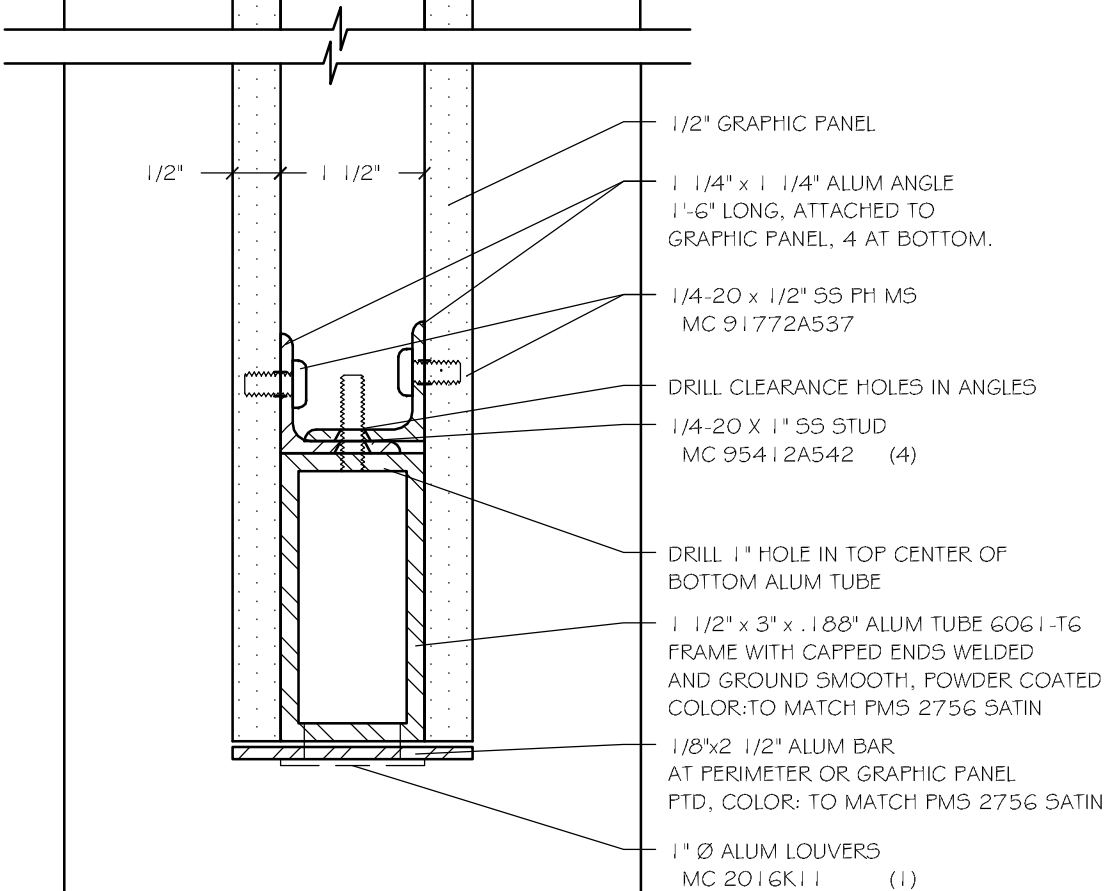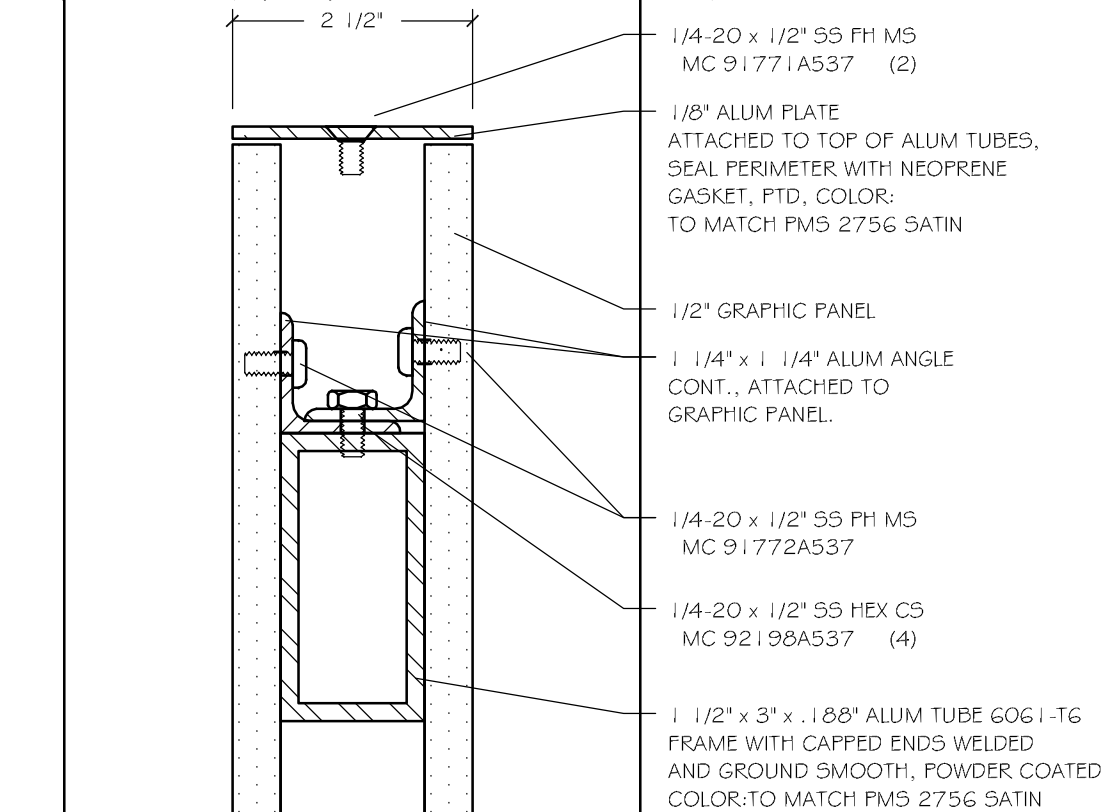

A SECTION
HALF

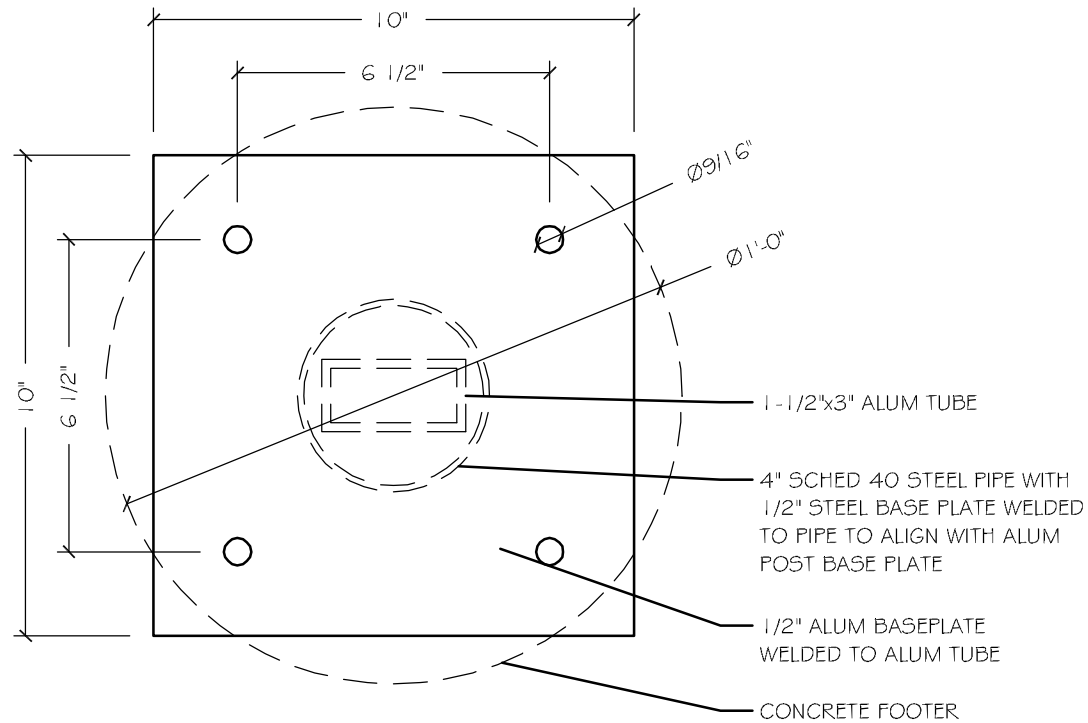

2 DETAIL-BASE PLATE
3" = 1'-0"

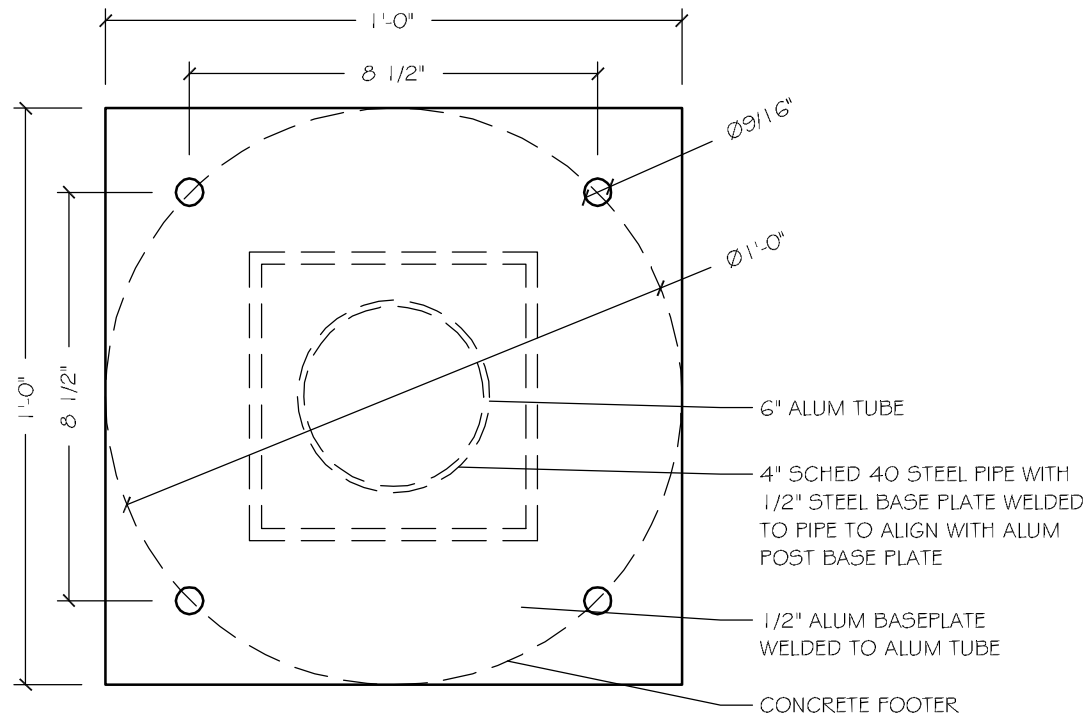

1 DETAIL-BASE PLATE
3" = 1'-0"

EXTERIOR

CHECKED BY:

DRAWN BY:

FOR APPROVAL
16 AUG 04

FOR PRODUCTION
30 AUG 04


FOR PRODUCTION
06 JAN 05

WHEELING WAYSIDE


SIGN TYPE UPRIGHT

DESIGN COMMUNICATIONS LTD


617 542 9620 (951 0777 FAX) Boston Orlando 407 856 9661 (856 9617 FAX)

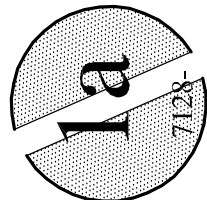

EXTERIOR

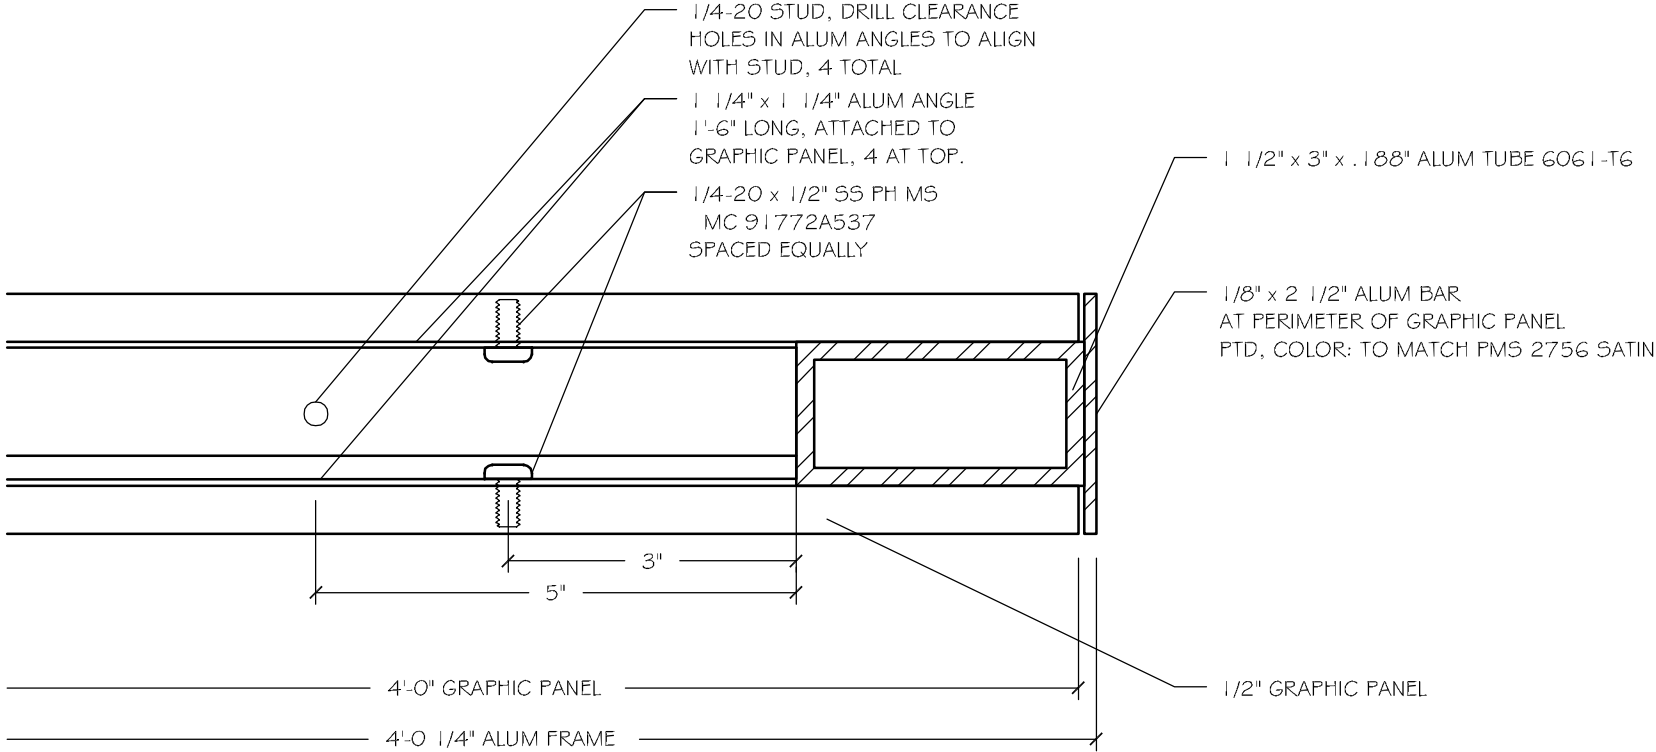

B SECTION
HALF

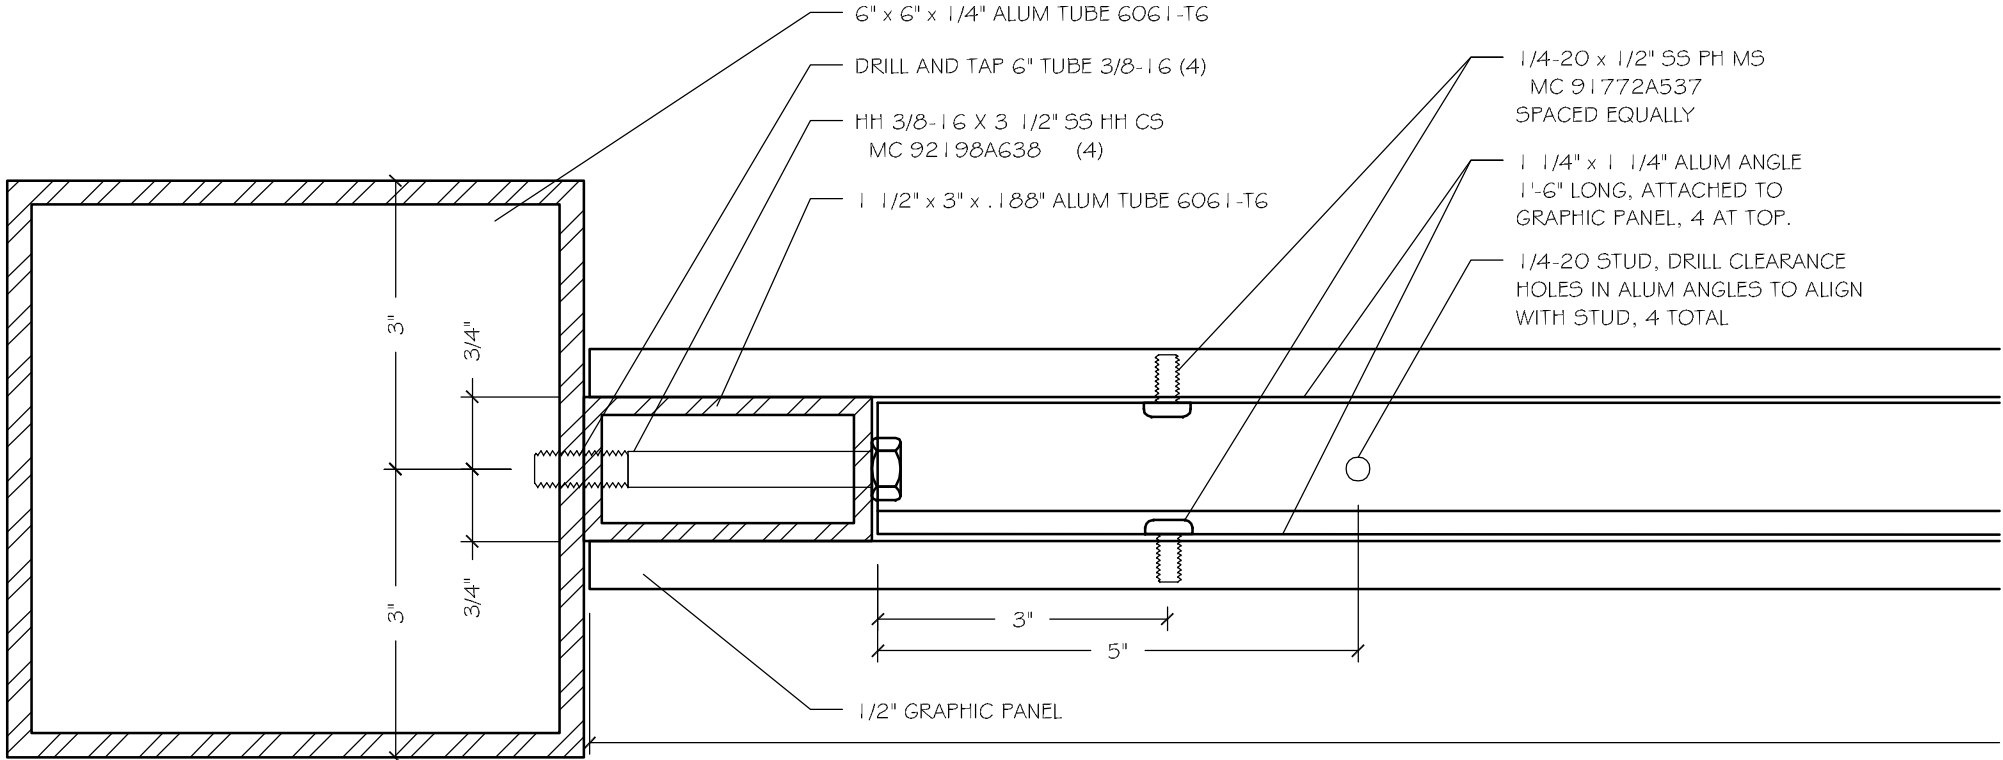

A SECTION
HALF

CHECKED BY:

DRAWN BY:

FOR APPROVAL
16 AUG 04

FOR PRODUCTION
30 AUG 04


FOR PRODUCTION
06 JAN 05

WHEELING WAYSIDE

SIGN TYPE UPRIGHT

DESIGN COMMUNICATIONS LTD

617 542 9620 (951 0777 FAX) Boston Orlando 407 856 9661 (856 9617 FAX)

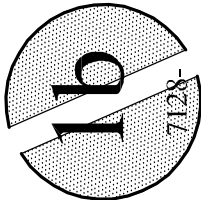

EXTERIOR


FOR APPROVAL
16 AUG 04

FOR PRODUCTION
30 AUG 04


FOR PRODUCTION
06 JAN 05

CHECKED BY:

DRAWN BY:

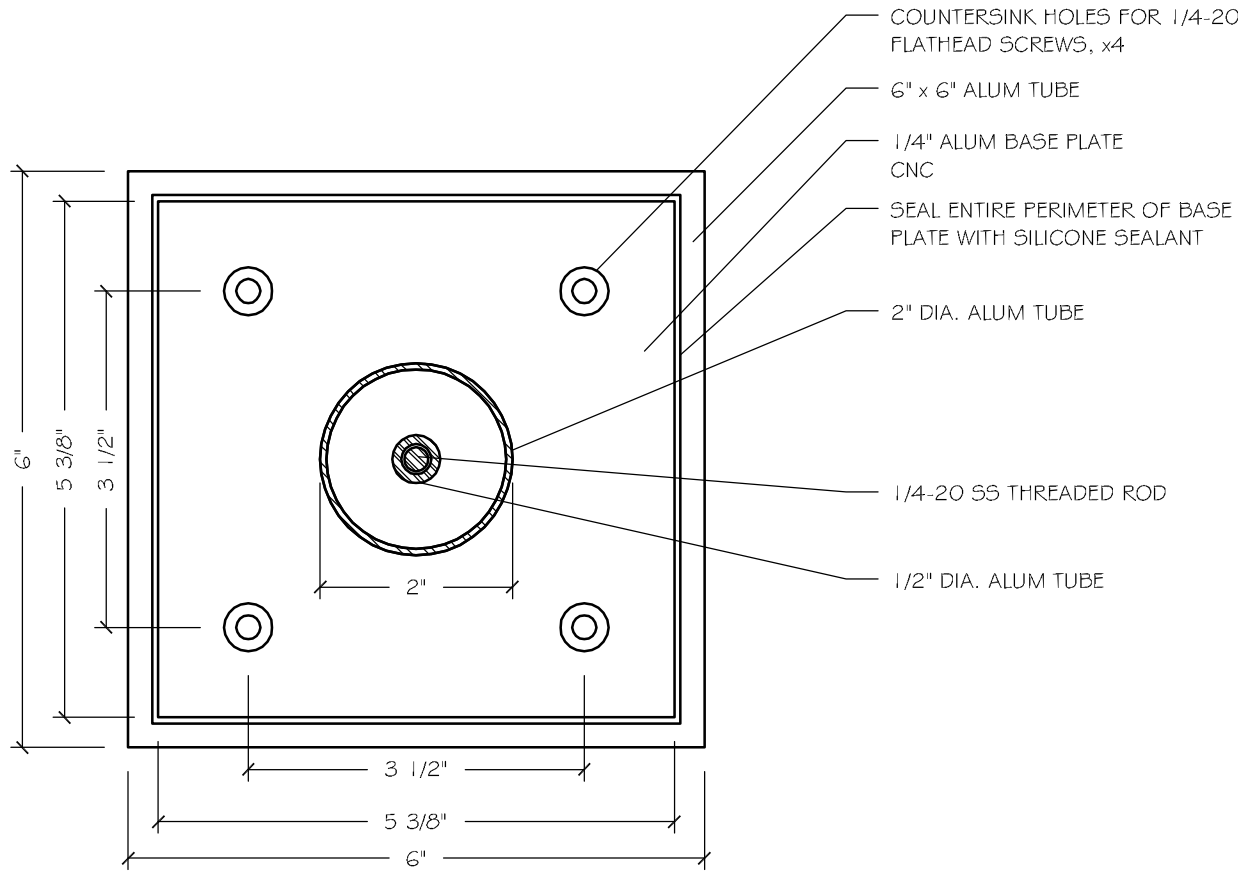


2 DETAIL - BASE PLATE DISTRICT ICON
HALF





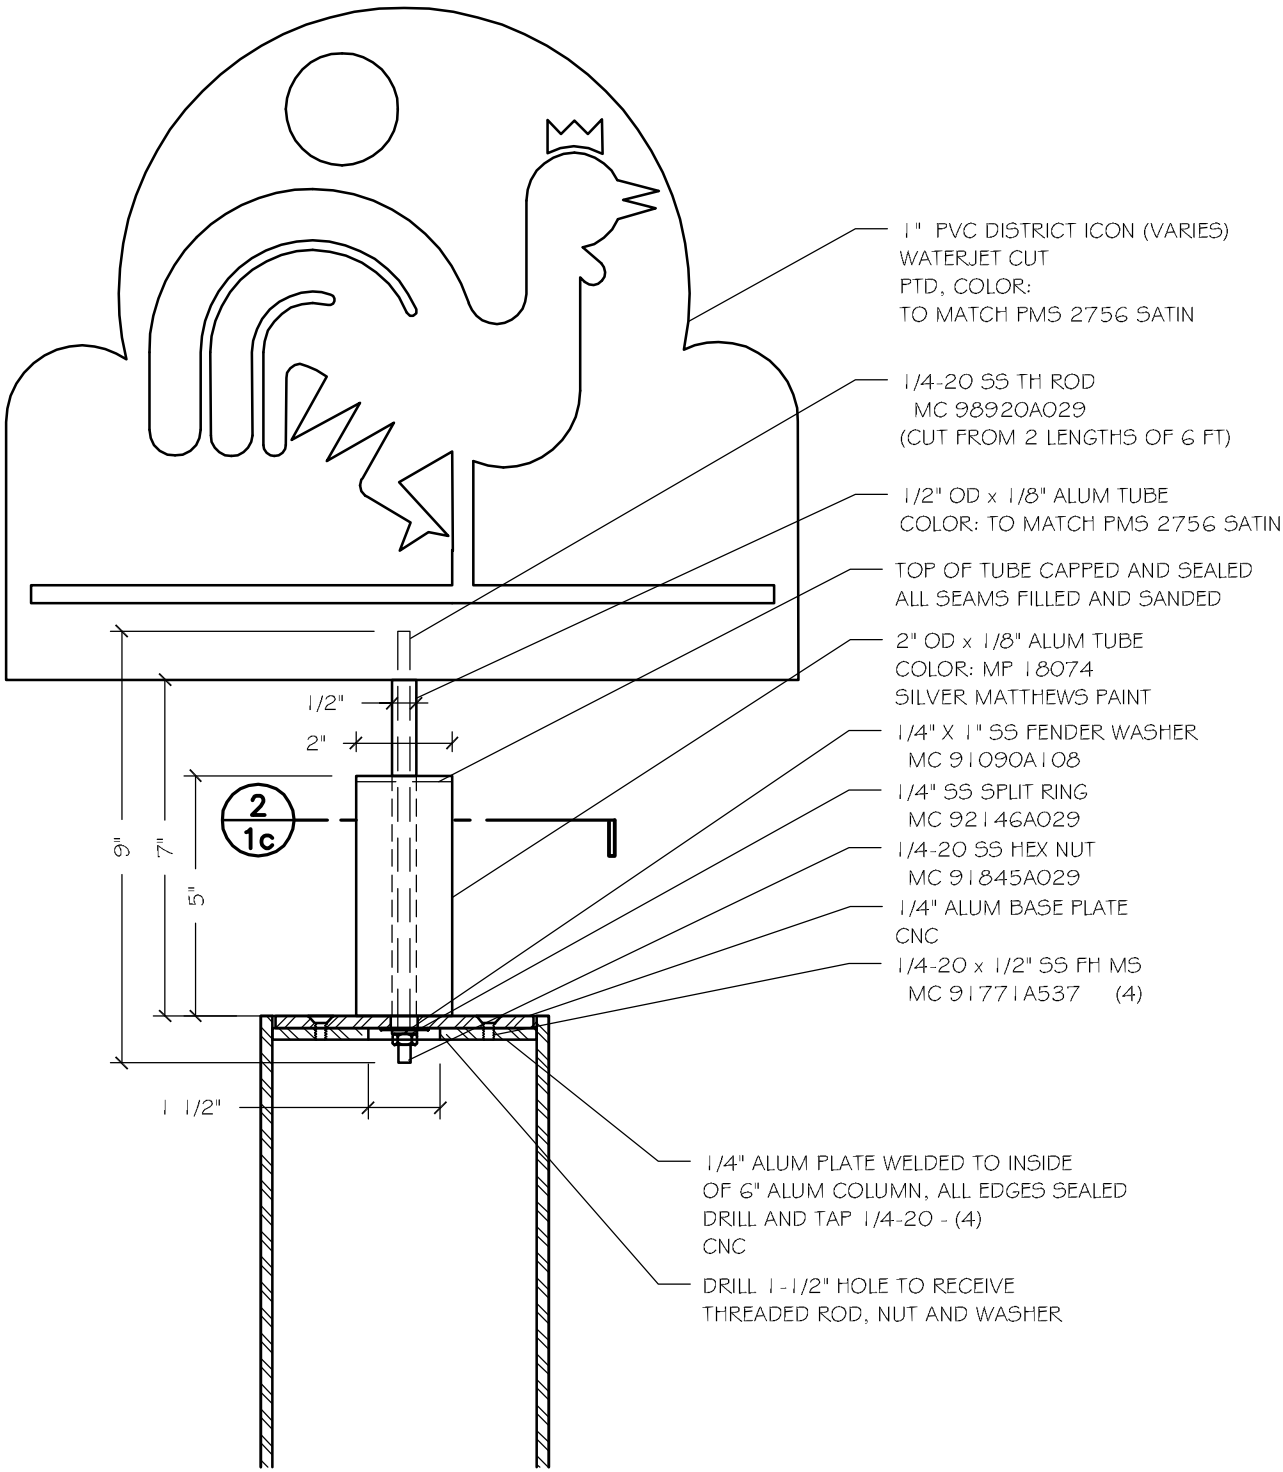


1 SECTION-ELEVATION
3" = 1'-0"

WHEELING WAYSIDE
SIGN TYPE UPRIGHT
DESIGN COMMUNICATIONS LTD
617 542 9620 (951 0777 FAX) Boston Orlando 407 856 9661 (856 9617 FAX)

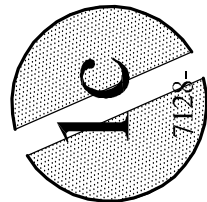

EXTERIOR

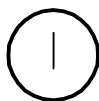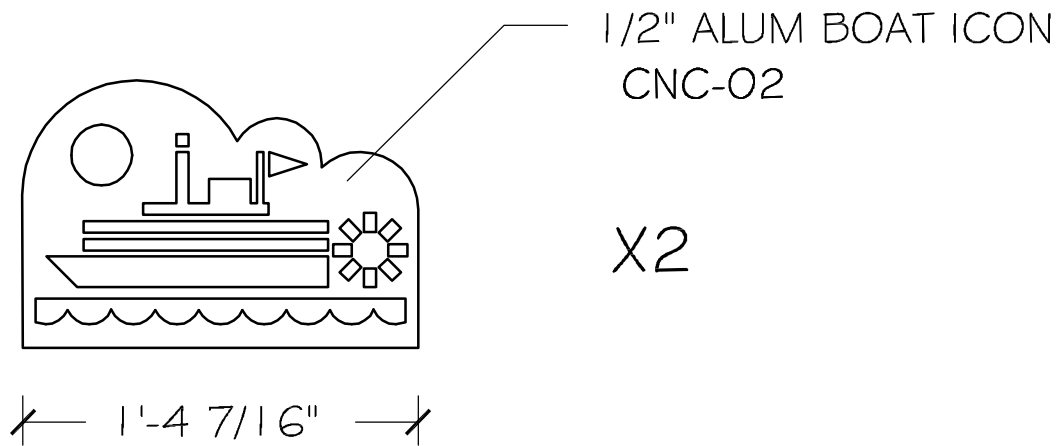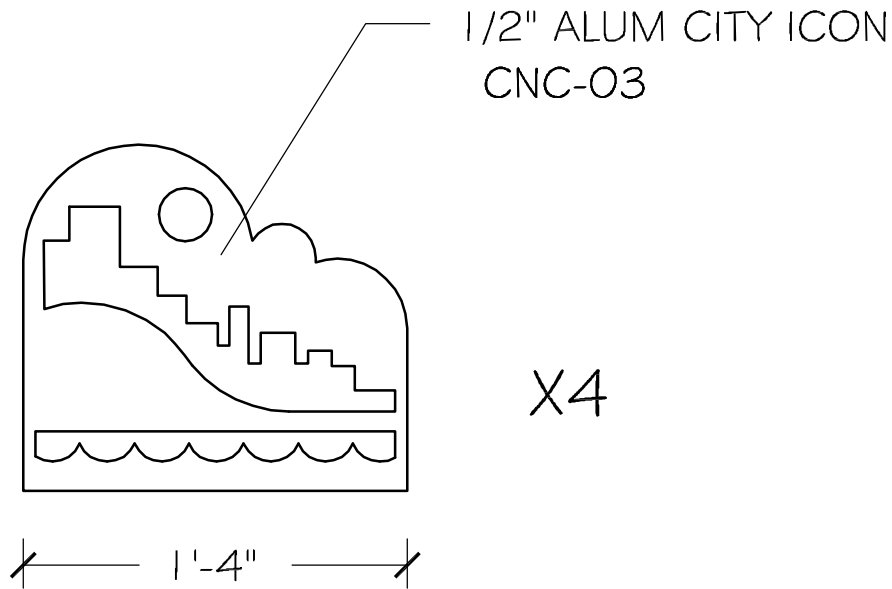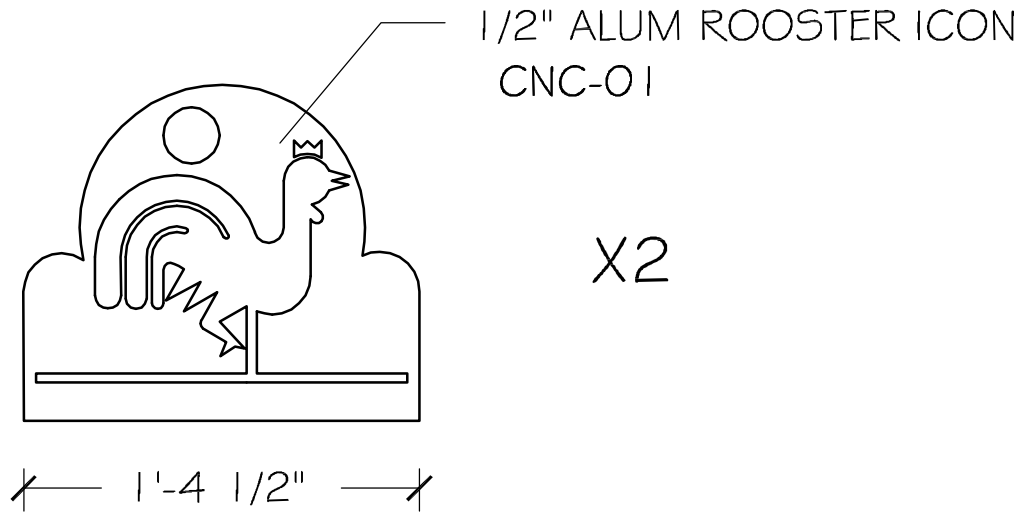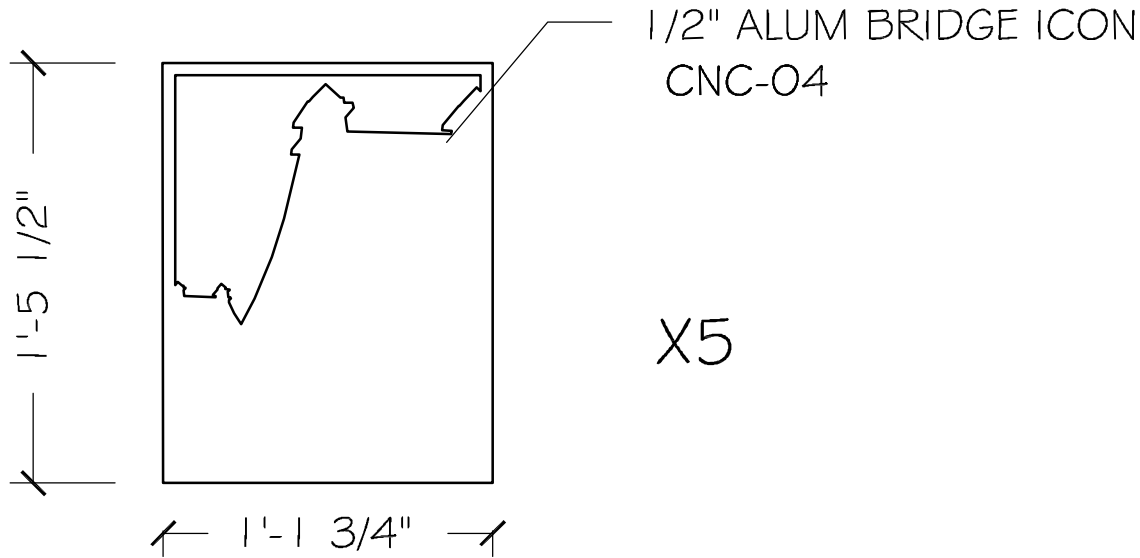

DETAIL - ICONS

1 1/2" = 1'-0"

DRAWN BY: CHECKED BY:

FOR APPROVAL
16 AUG 04

FOR PRODUCTION
30 AUG 04

06 JAN 05

WHEELING WAYSIDE

SIGN TYPE UPRIGHT

DESIGN COMMUNICATIONS LTD

617 542 9620 (951 0777 FAX) Boston Orlando 407 856 9661 (856 9617 FAX)

